




ПОЛЕСЬЕ
строительная компания

Конструктивное решение
индивидуального каркасного дома "Сударь" 9х10 метров.

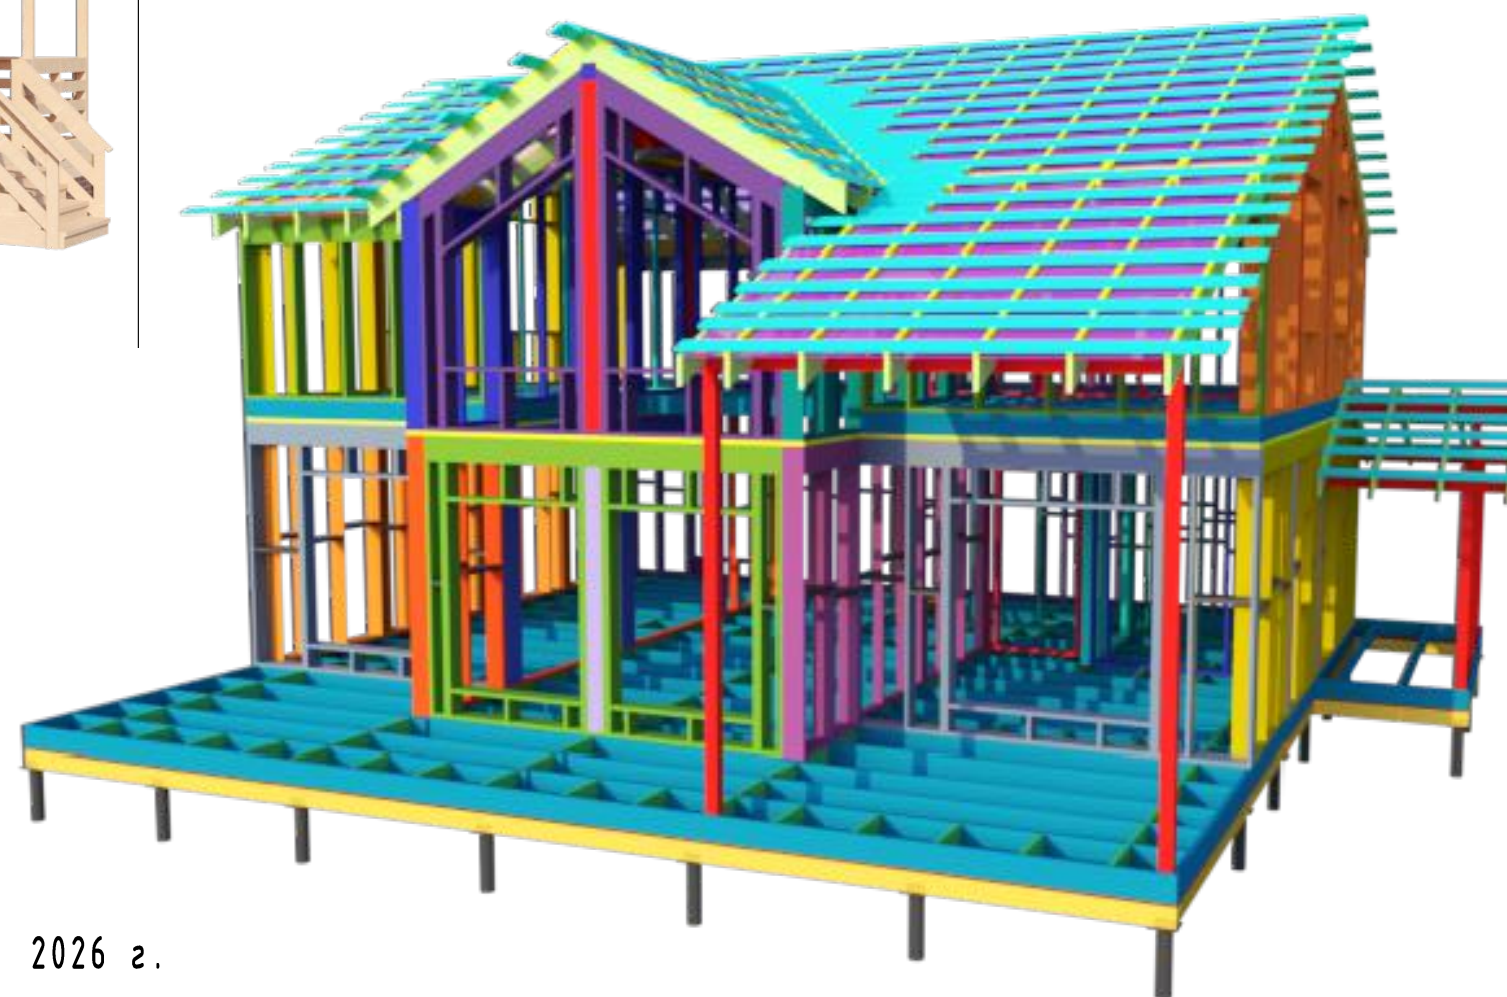

2026 г.

Объёмно-планировочные решения. Вид 1. Вид 2. Вид 3. Вид 4.



Изм.	Кол. уч.	Лист	№ док.	Подп.	Дата	Объёмно-планировочные решения. Вид 1. Вид 2. Вид 3. Вид 4.	Лист
							1

Фасад 1-4.




Фасад А-В.



Фасад 4-1.




Фасад В-А.

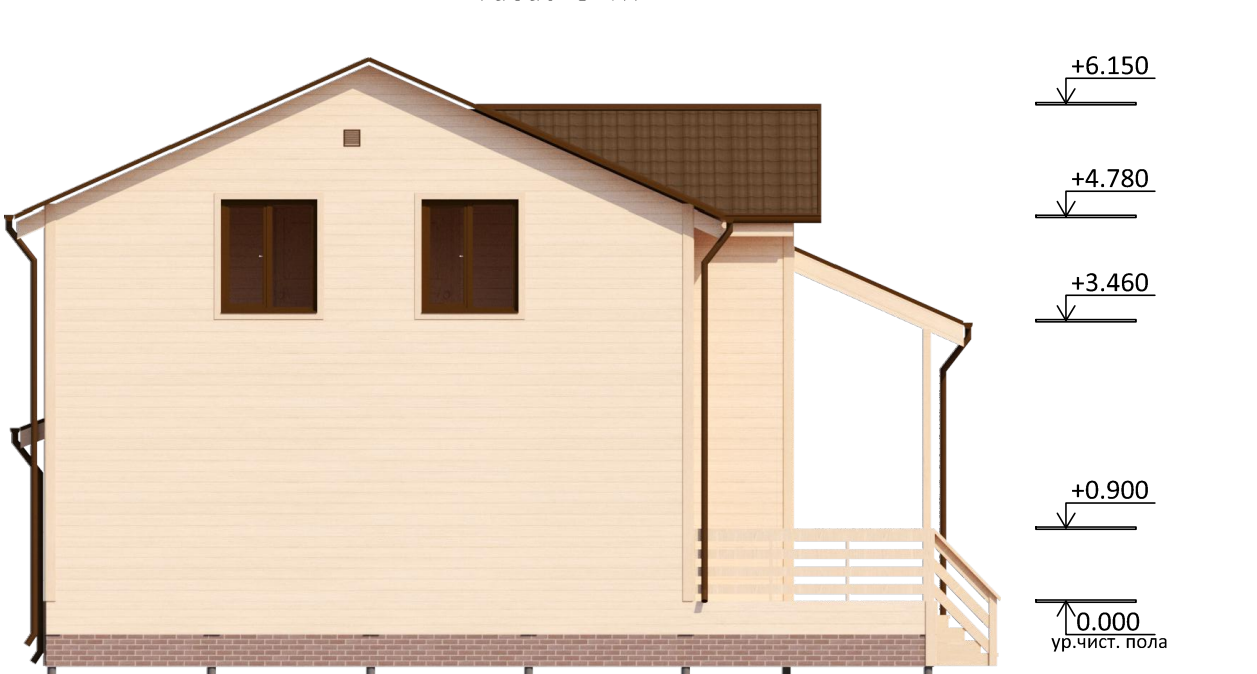


Изм.	Кол. уч.	Лист	№ док.	Подп.	Дата	Фасад 1-4. Фасад 4-1. Фасад А-В. Фасад В-А.		Лист
								2

План 1-го этажа на отм. +0,000. Планировочное решение.

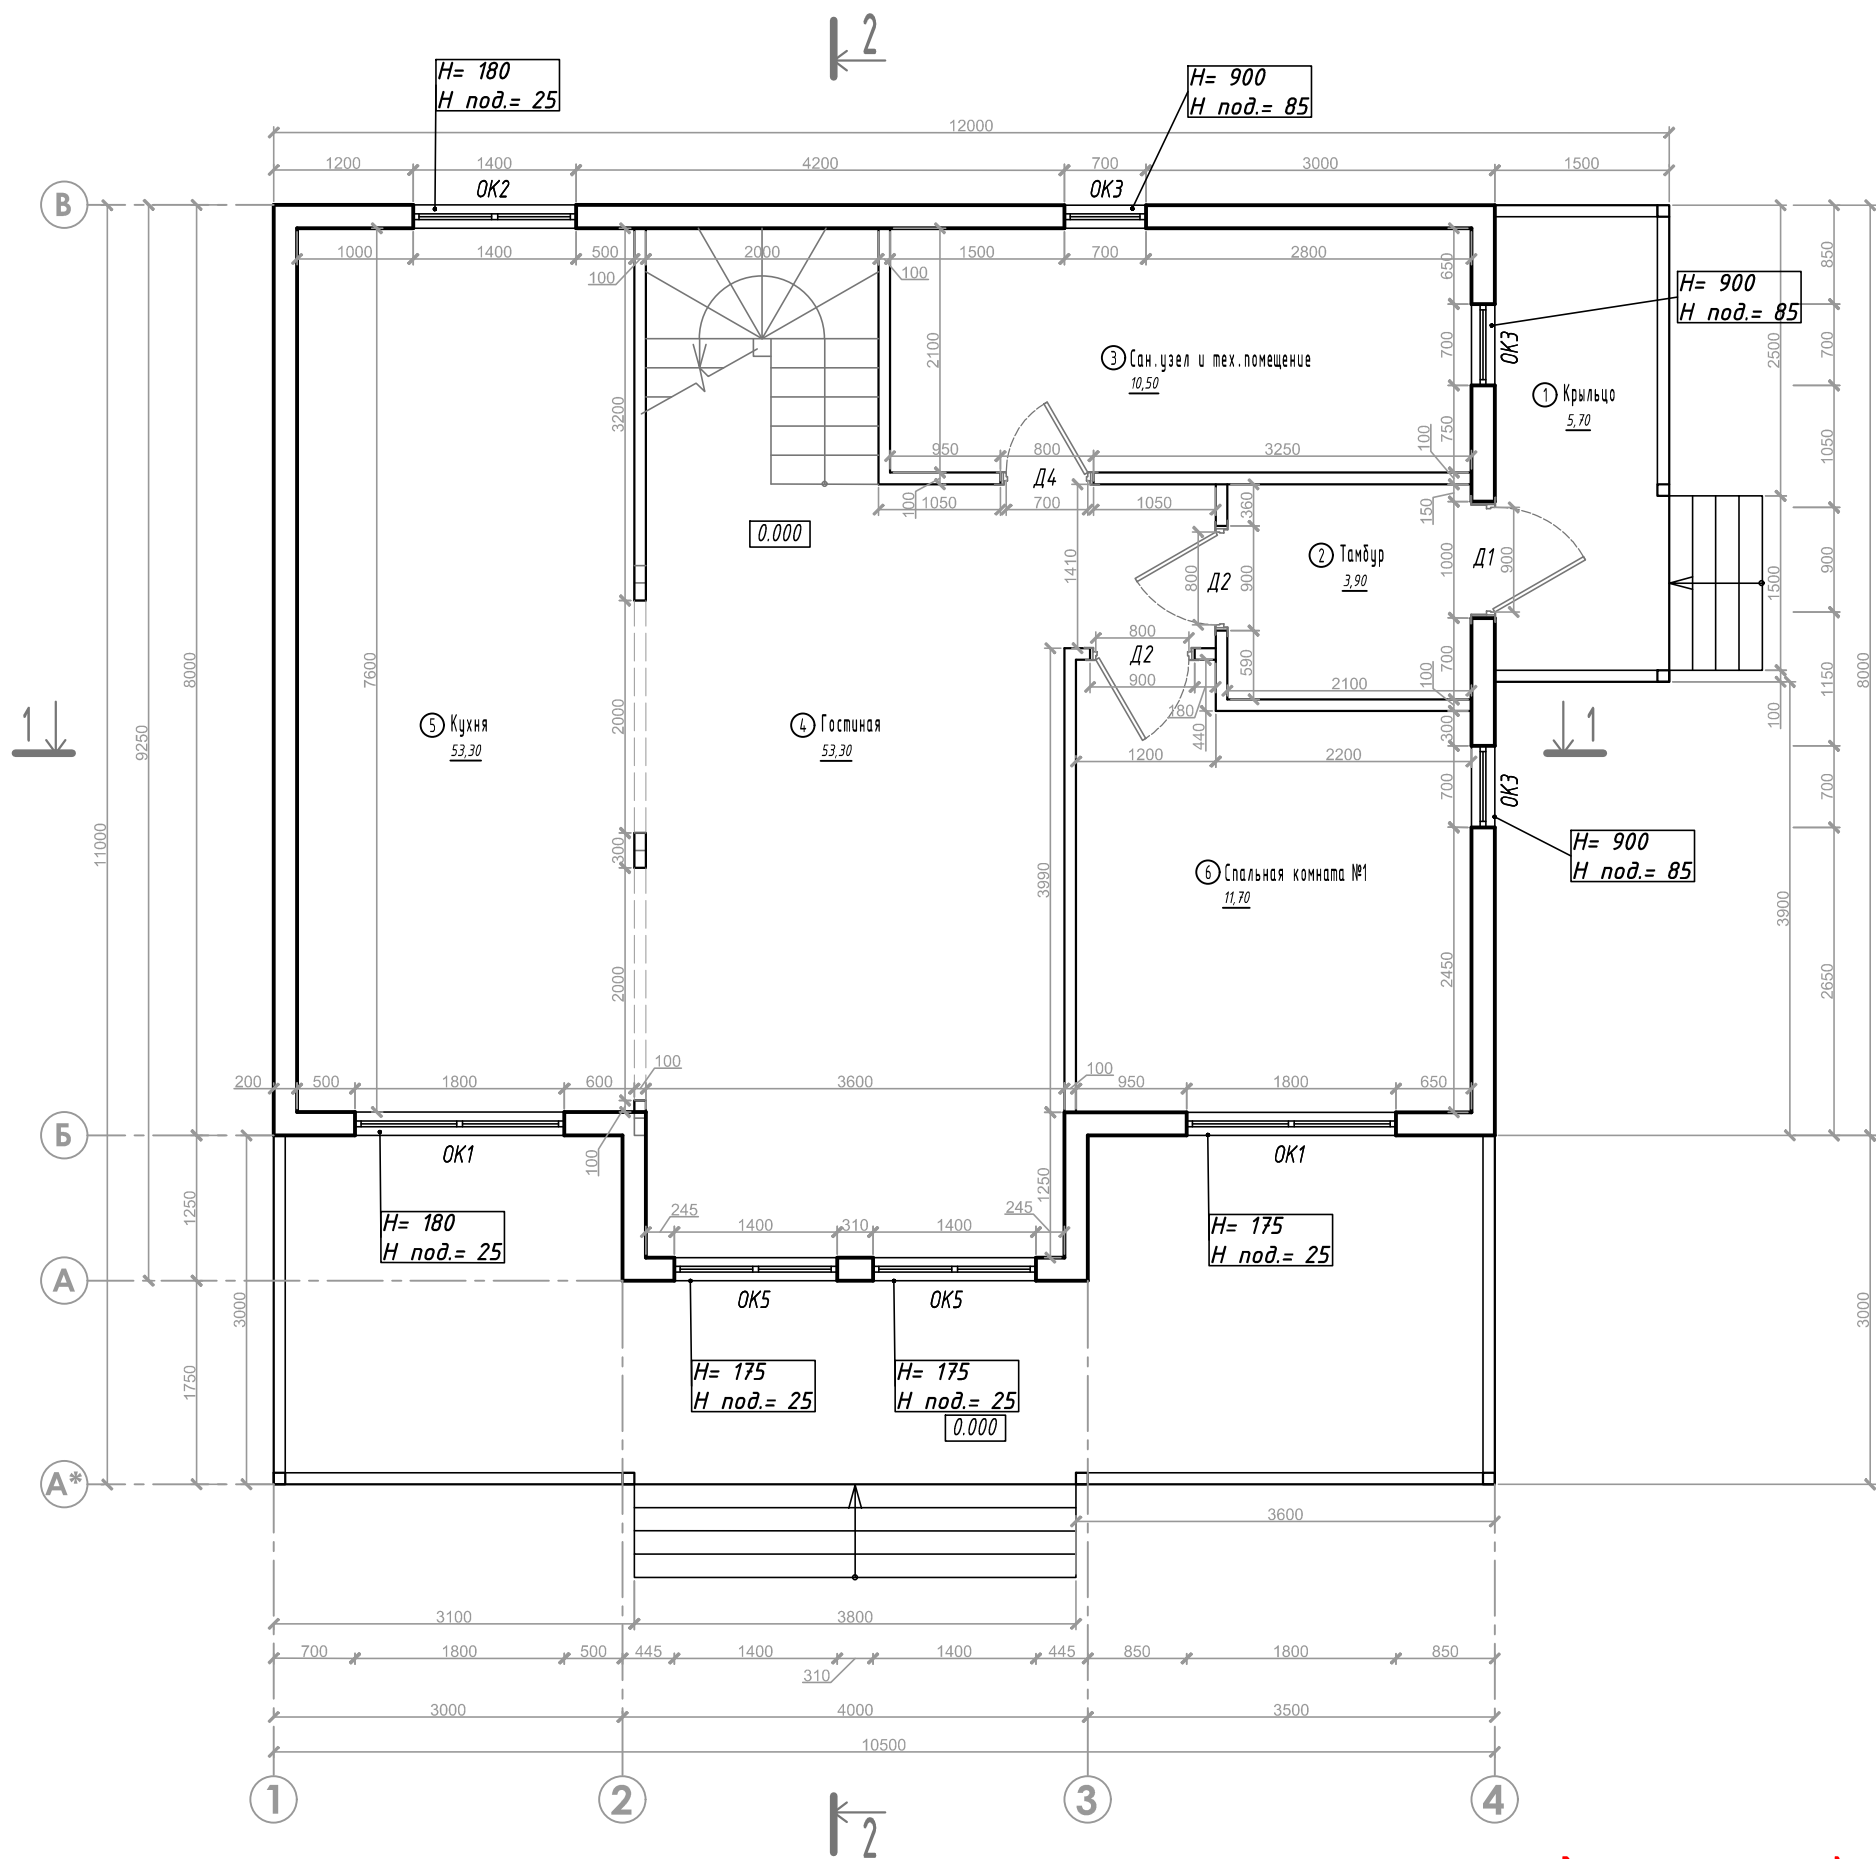


Расположение элементов каркаса.

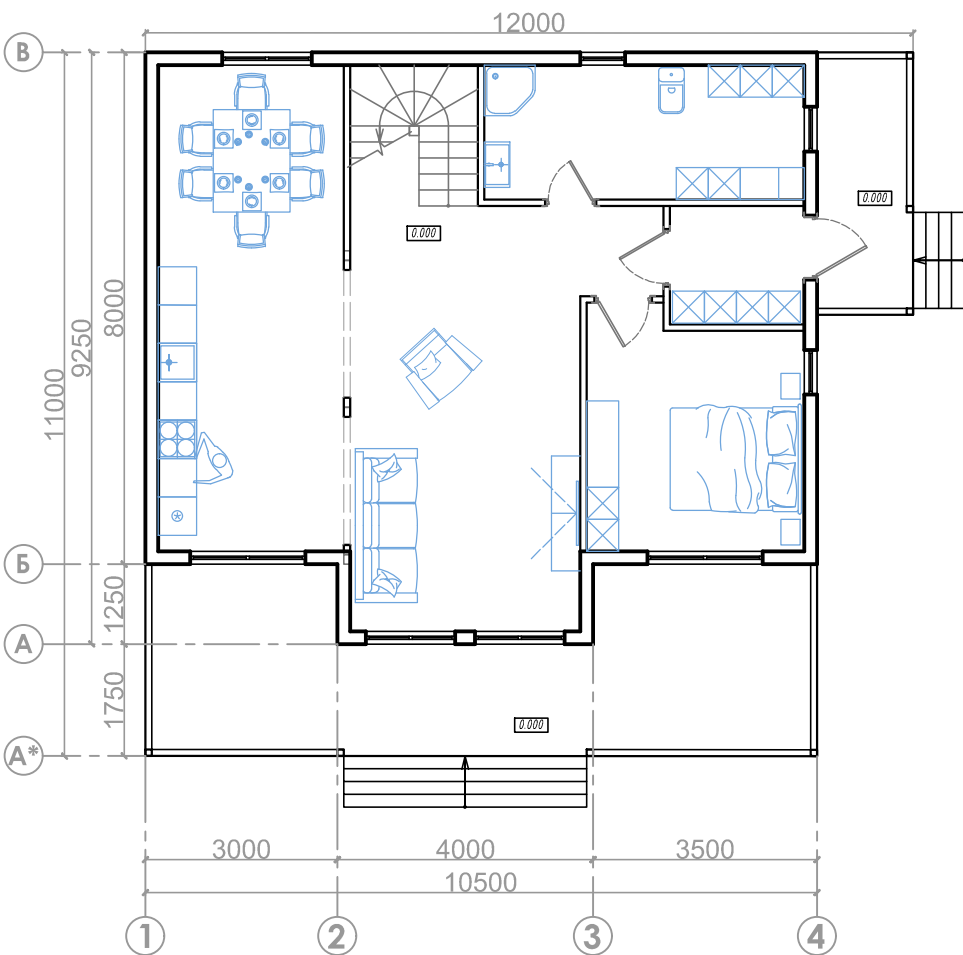


* Расстояния указаны между стенками каркаса без учёта отделки.

Изм.	Кол. уч.	Лист	№ док.	Подп.	Дата	План 1-го этажа на отм. 0,000. Планировочное решение.	Лист
							3

План 2-го мансардного этажа на отм. +2,880. Планировочное решение.

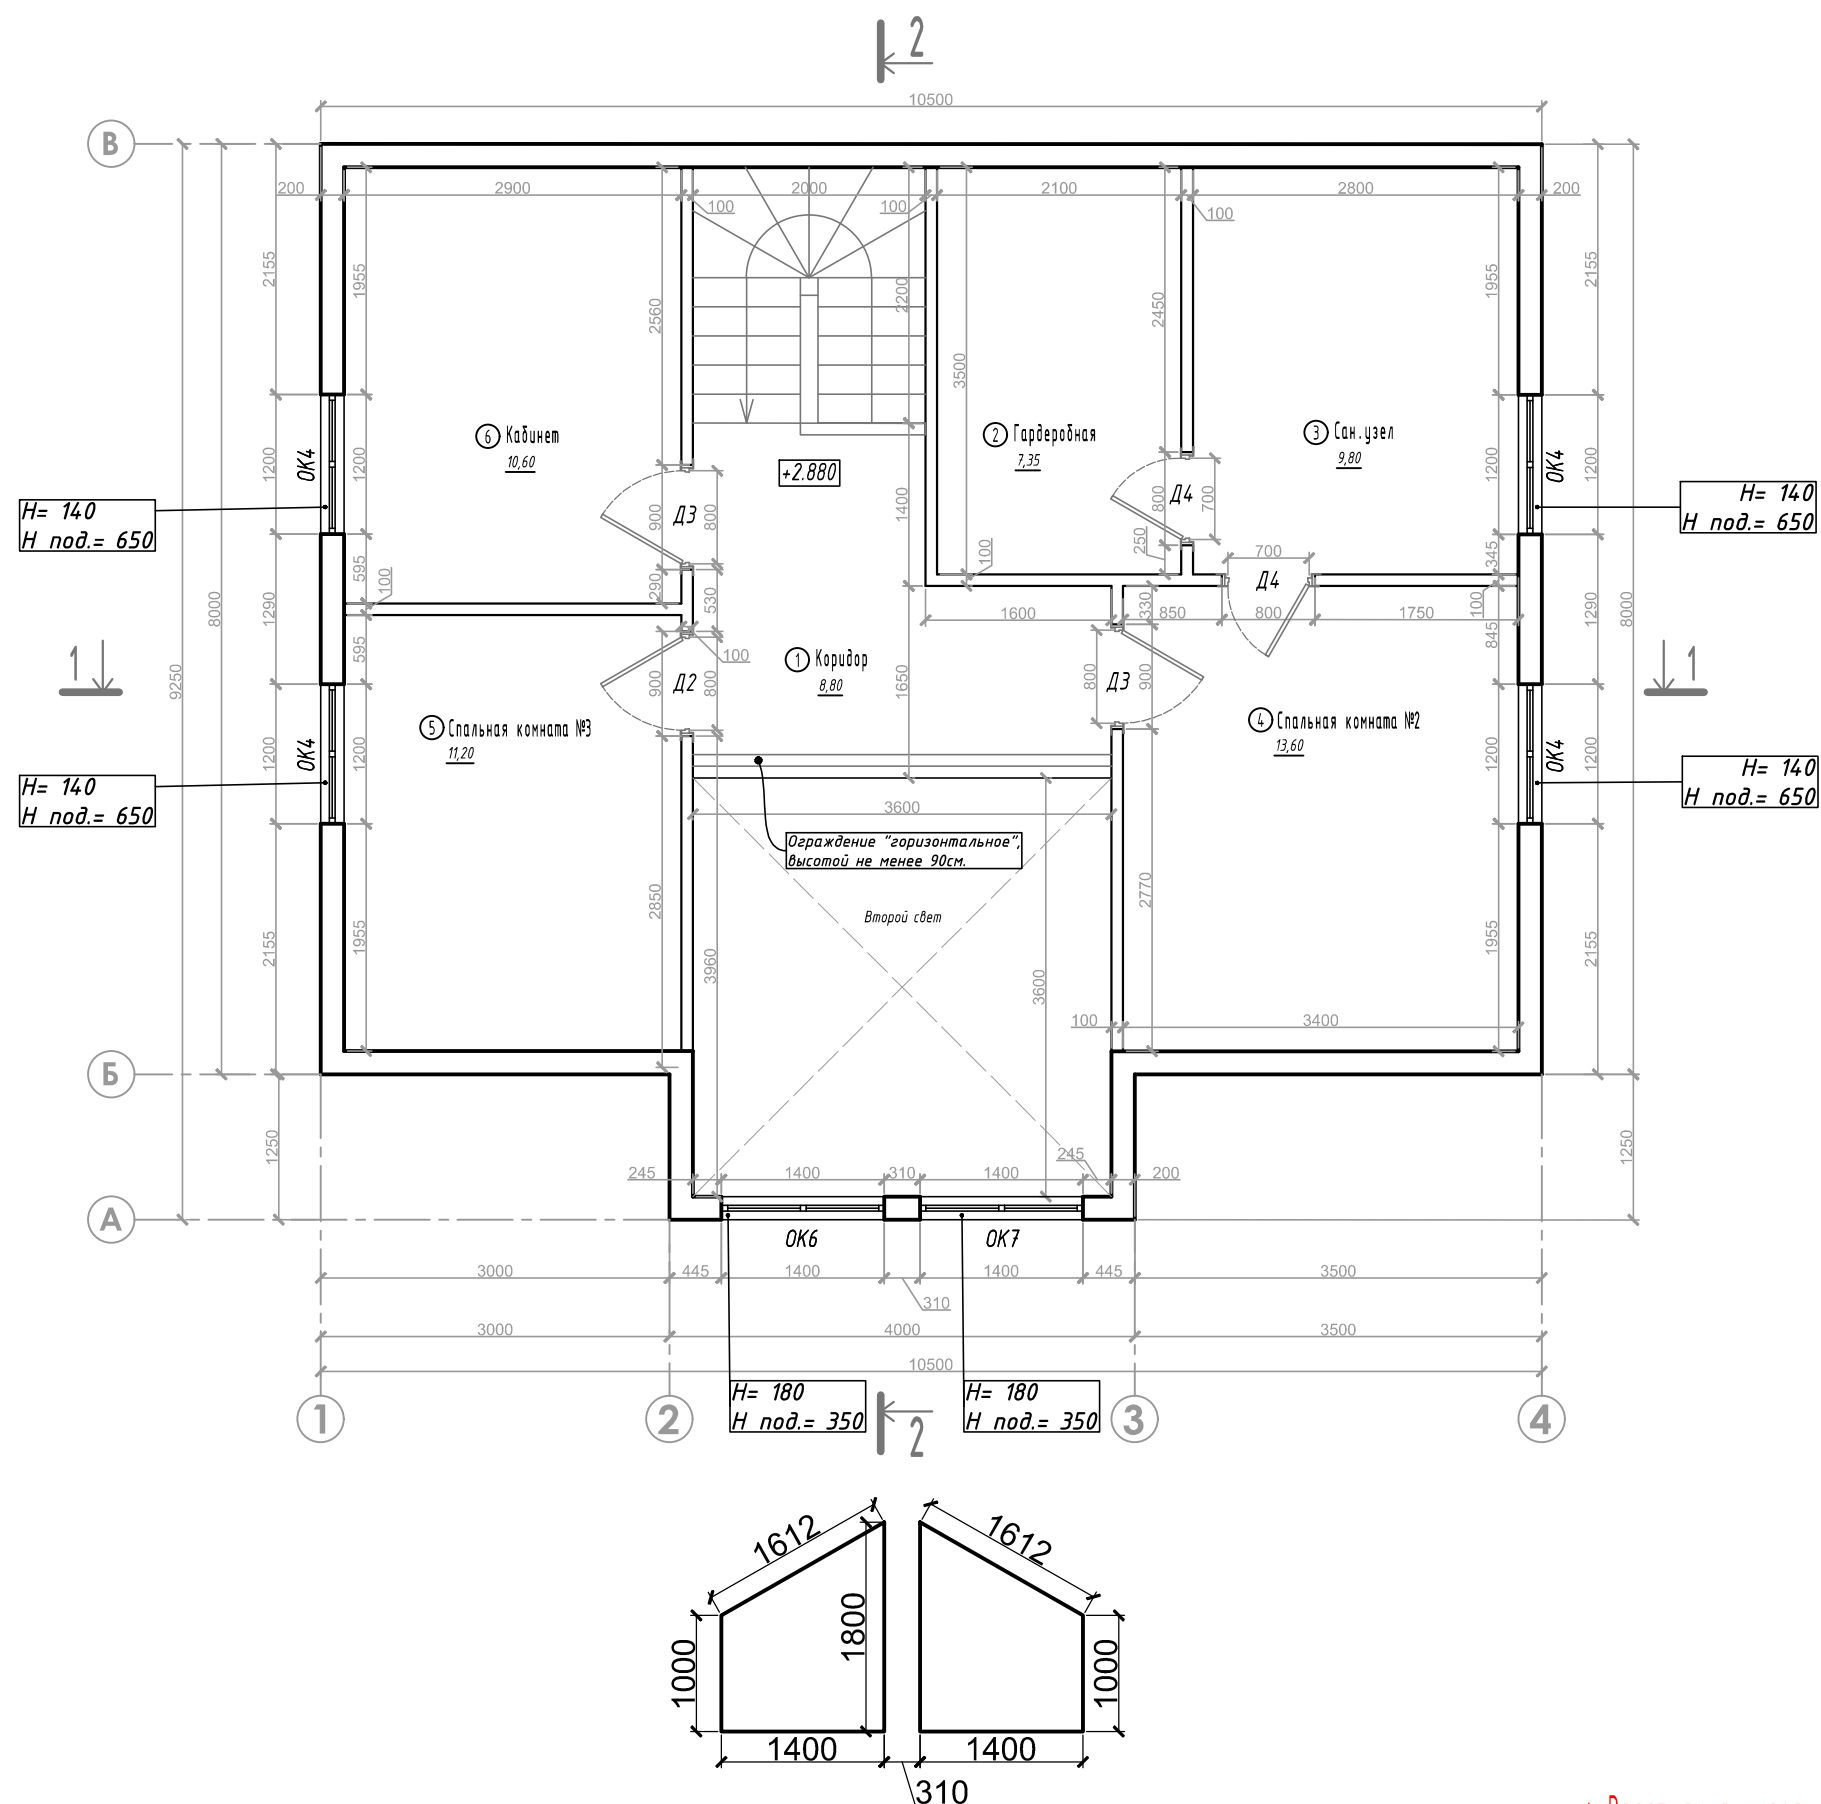



Расположение элементов каркаса.

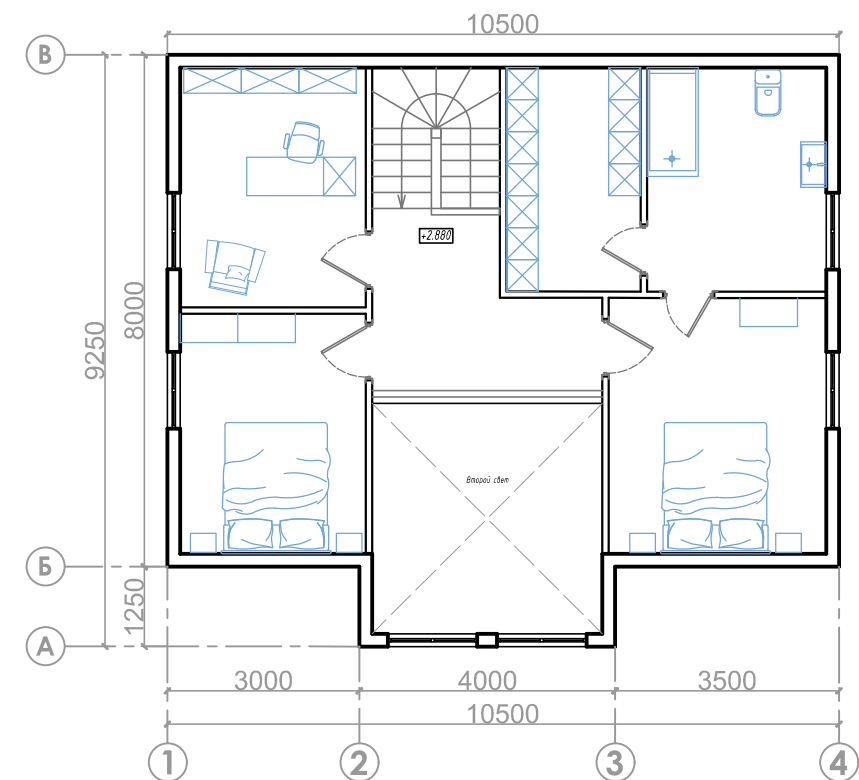

* Расстояния указаны между стенками каркаса без учёта отделки.

Изм.	Кол. уч.	Лист	№ док.	Подп.	Дата	План 2-го мансардного этажа на отм. 2,880. Планировочное решение.	Лист
							4

Общий вид каркаса дома.

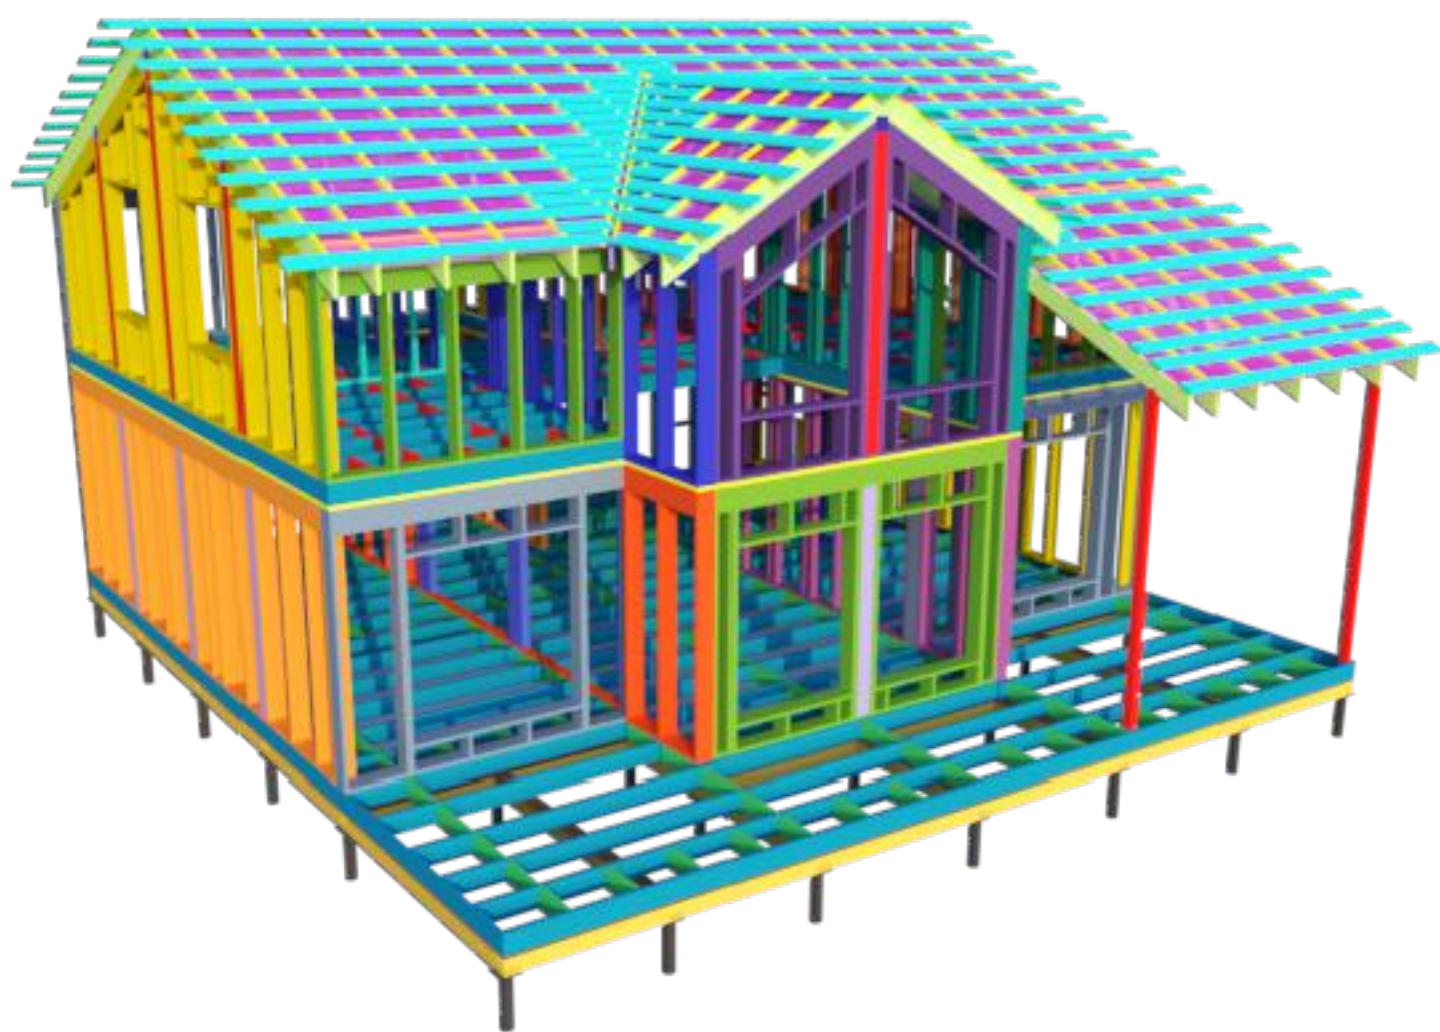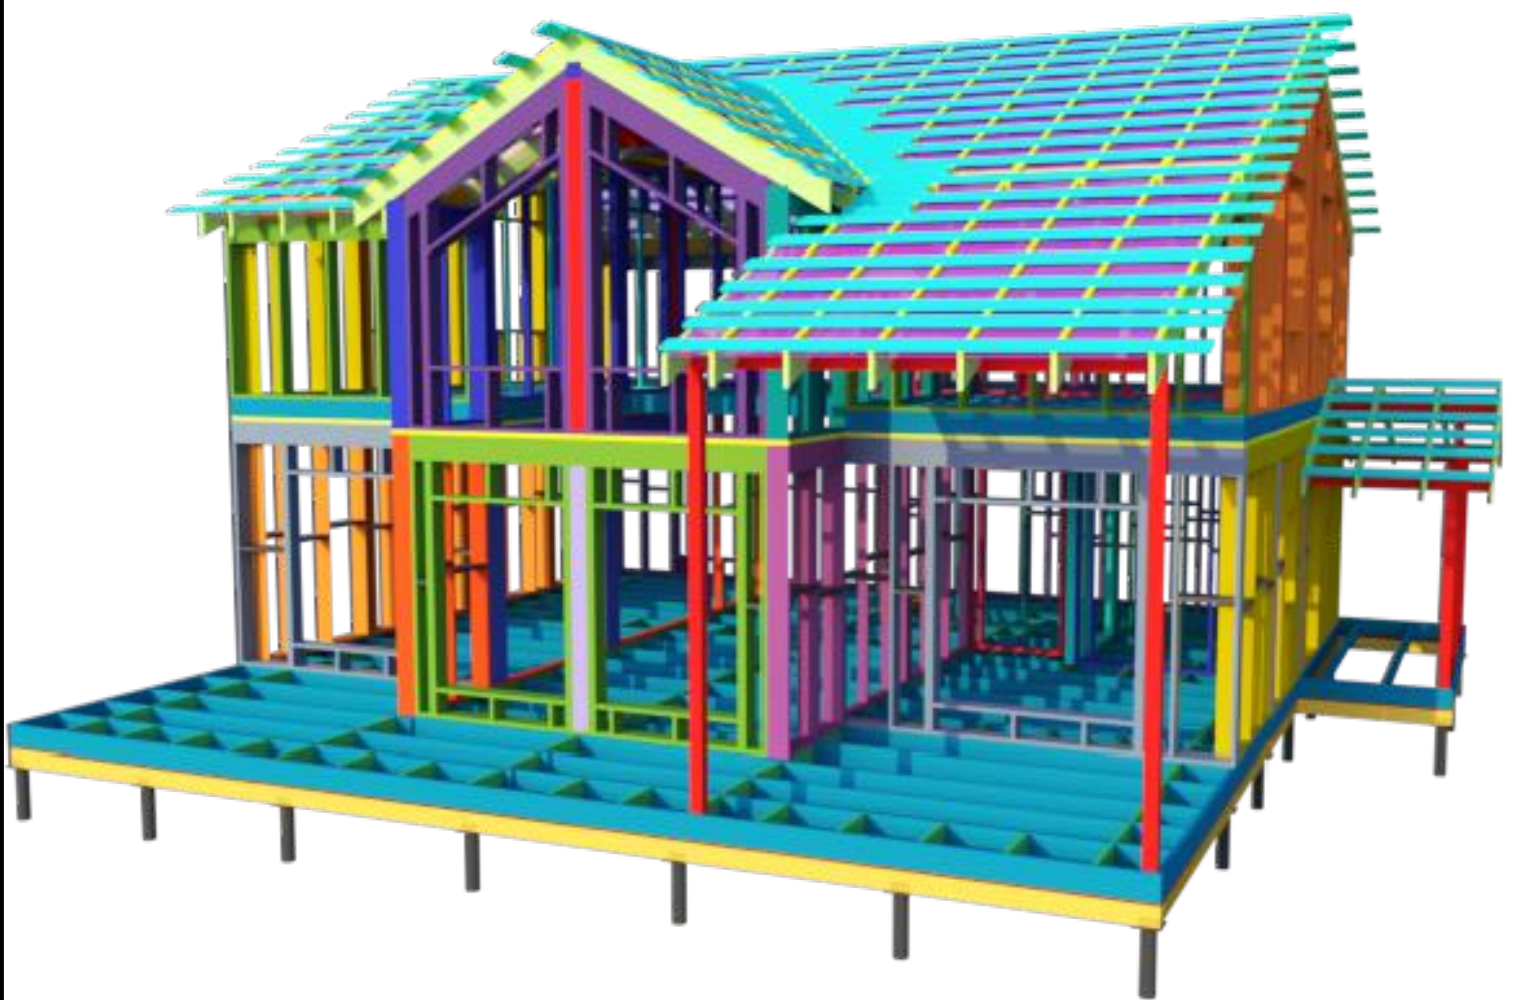


Изм.	Кол. уч.	Лист	№ док.	Подп.	Дата

Общий вид каркаса дома.

Лист
5

Свайное поле.

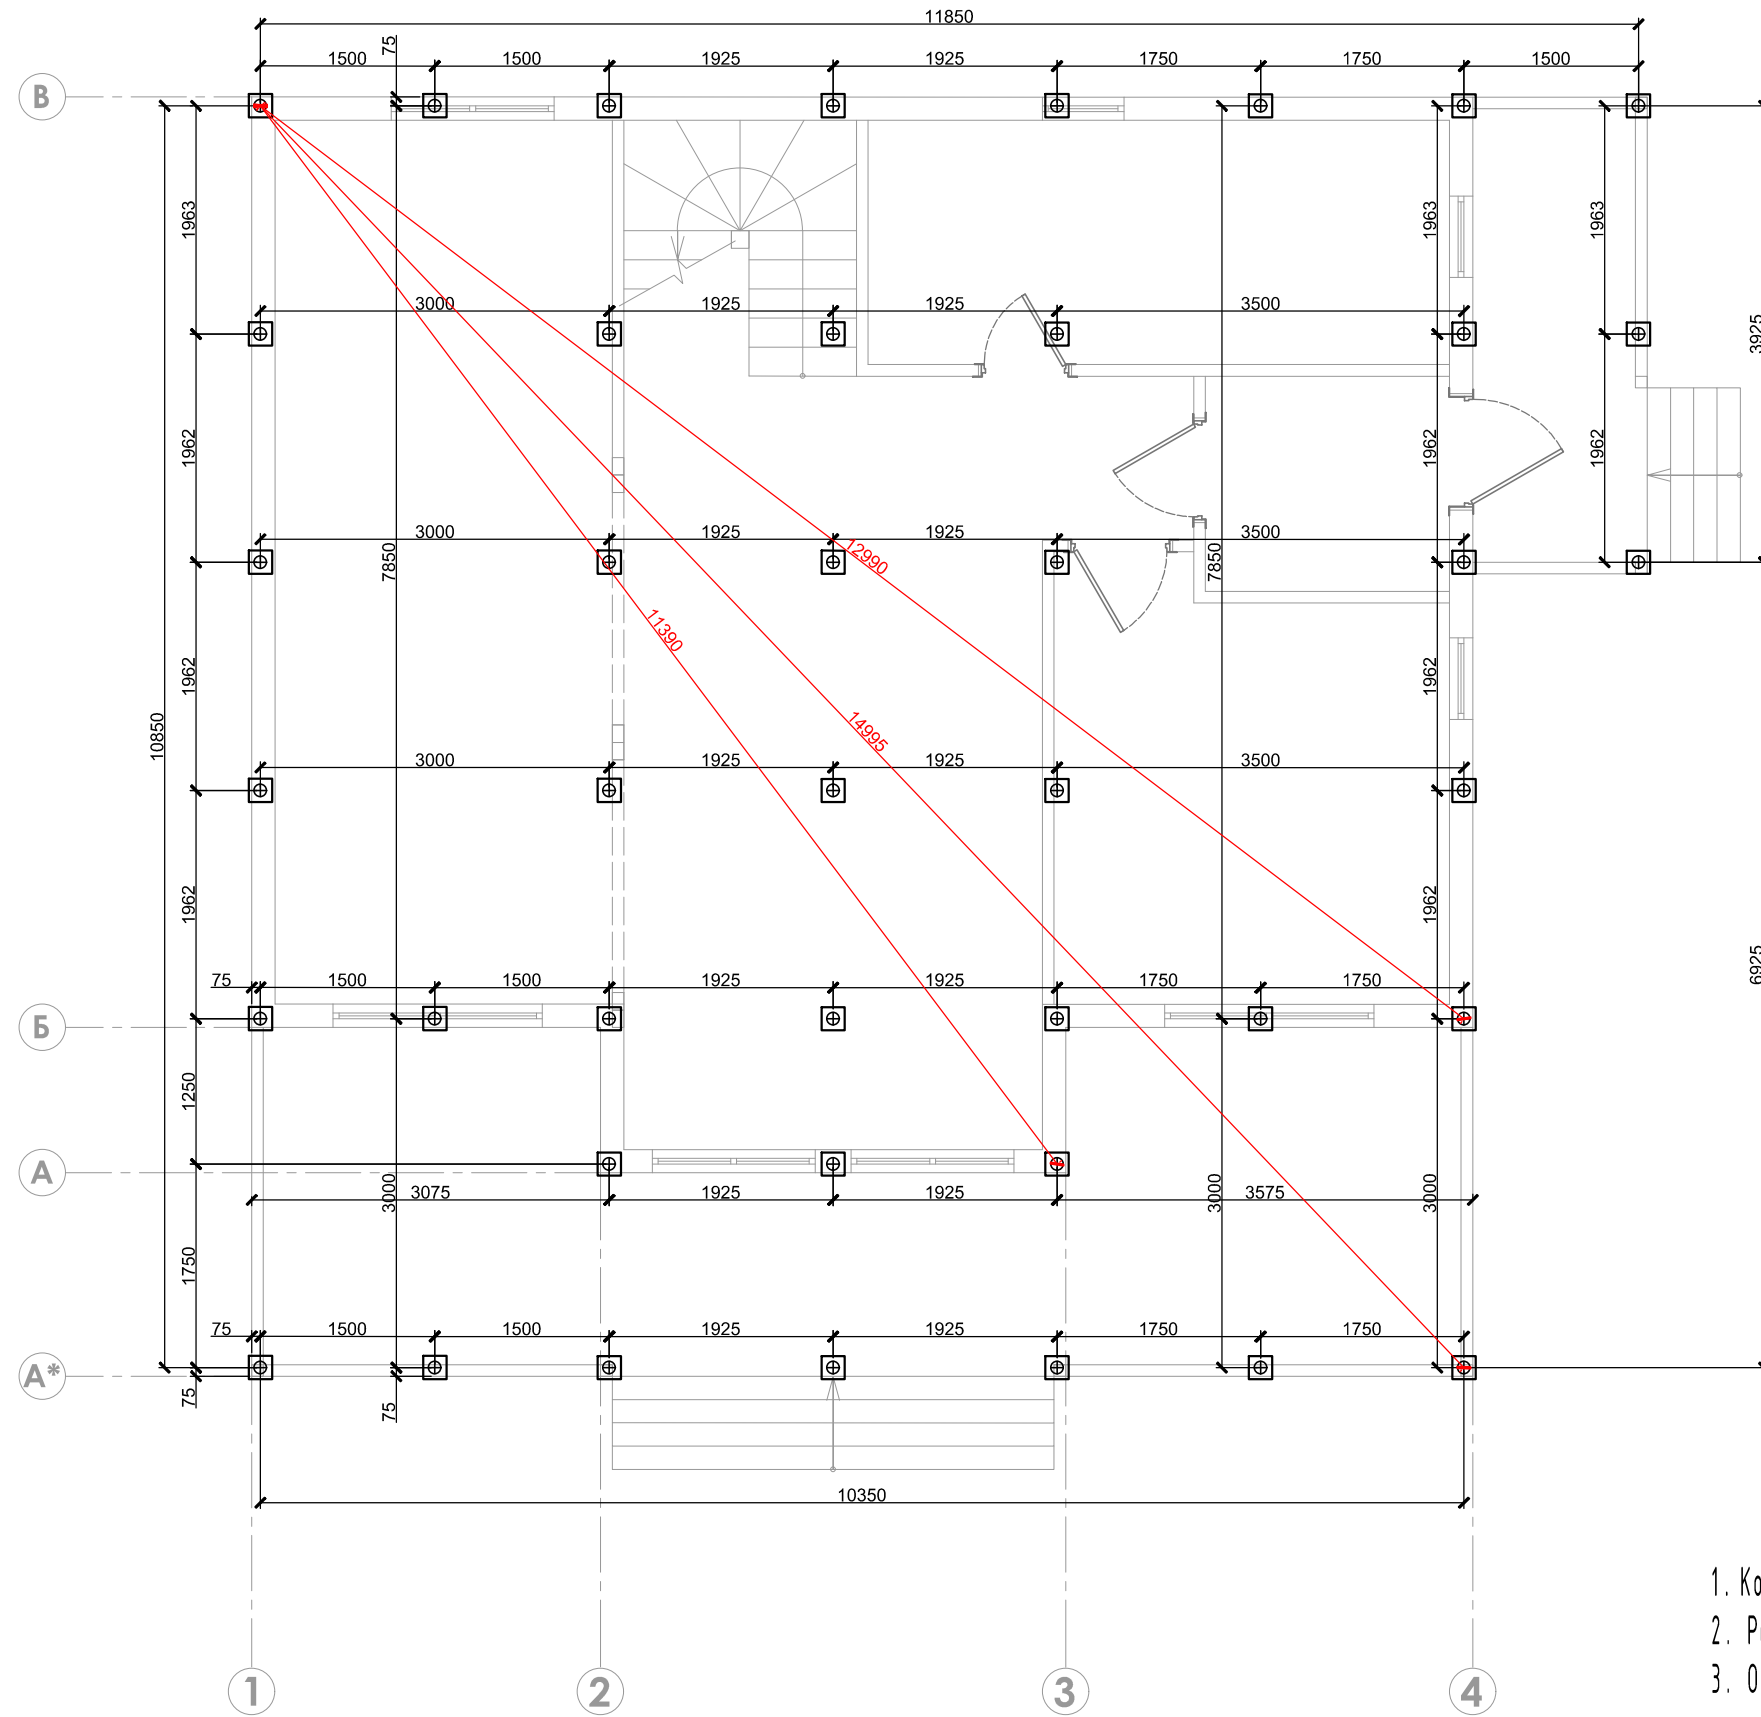

1. Кол-во свай - 42.
2. Расстояние п центрам свай.
3. Оголовок квадратный min 200x200мм.

Изм.	Кол. уч.	Лист	№ док.	Подп.	Дата

Свайное поле.

lucm

6

Обвязка свай.

Экспликация:

Маркировка	Длина	Ширина	Толщина	Кол-во
Б 5000	5000	150	150	6
Б 5500	5500	150	150	3
Б 5425	5425	150	150	3
Б 1575	1575	150	150	3
Б 4000	4000	150	150	1
Б 4075	4075	150	150	1
Б 5962	5962	150	150	5
Б 5038	5038	150	150	5
Б 3150	3150	150	150	2

Расположение элементов.

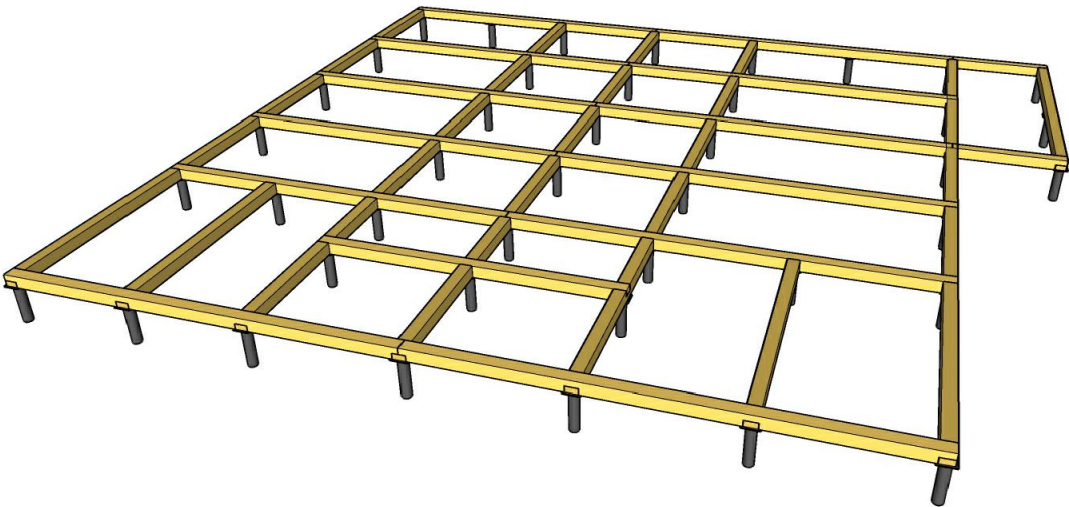


Схема углового соединения доски.



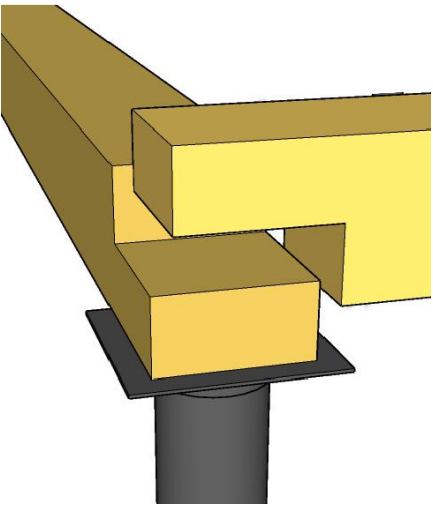


Схема Т-образного соединения доски.

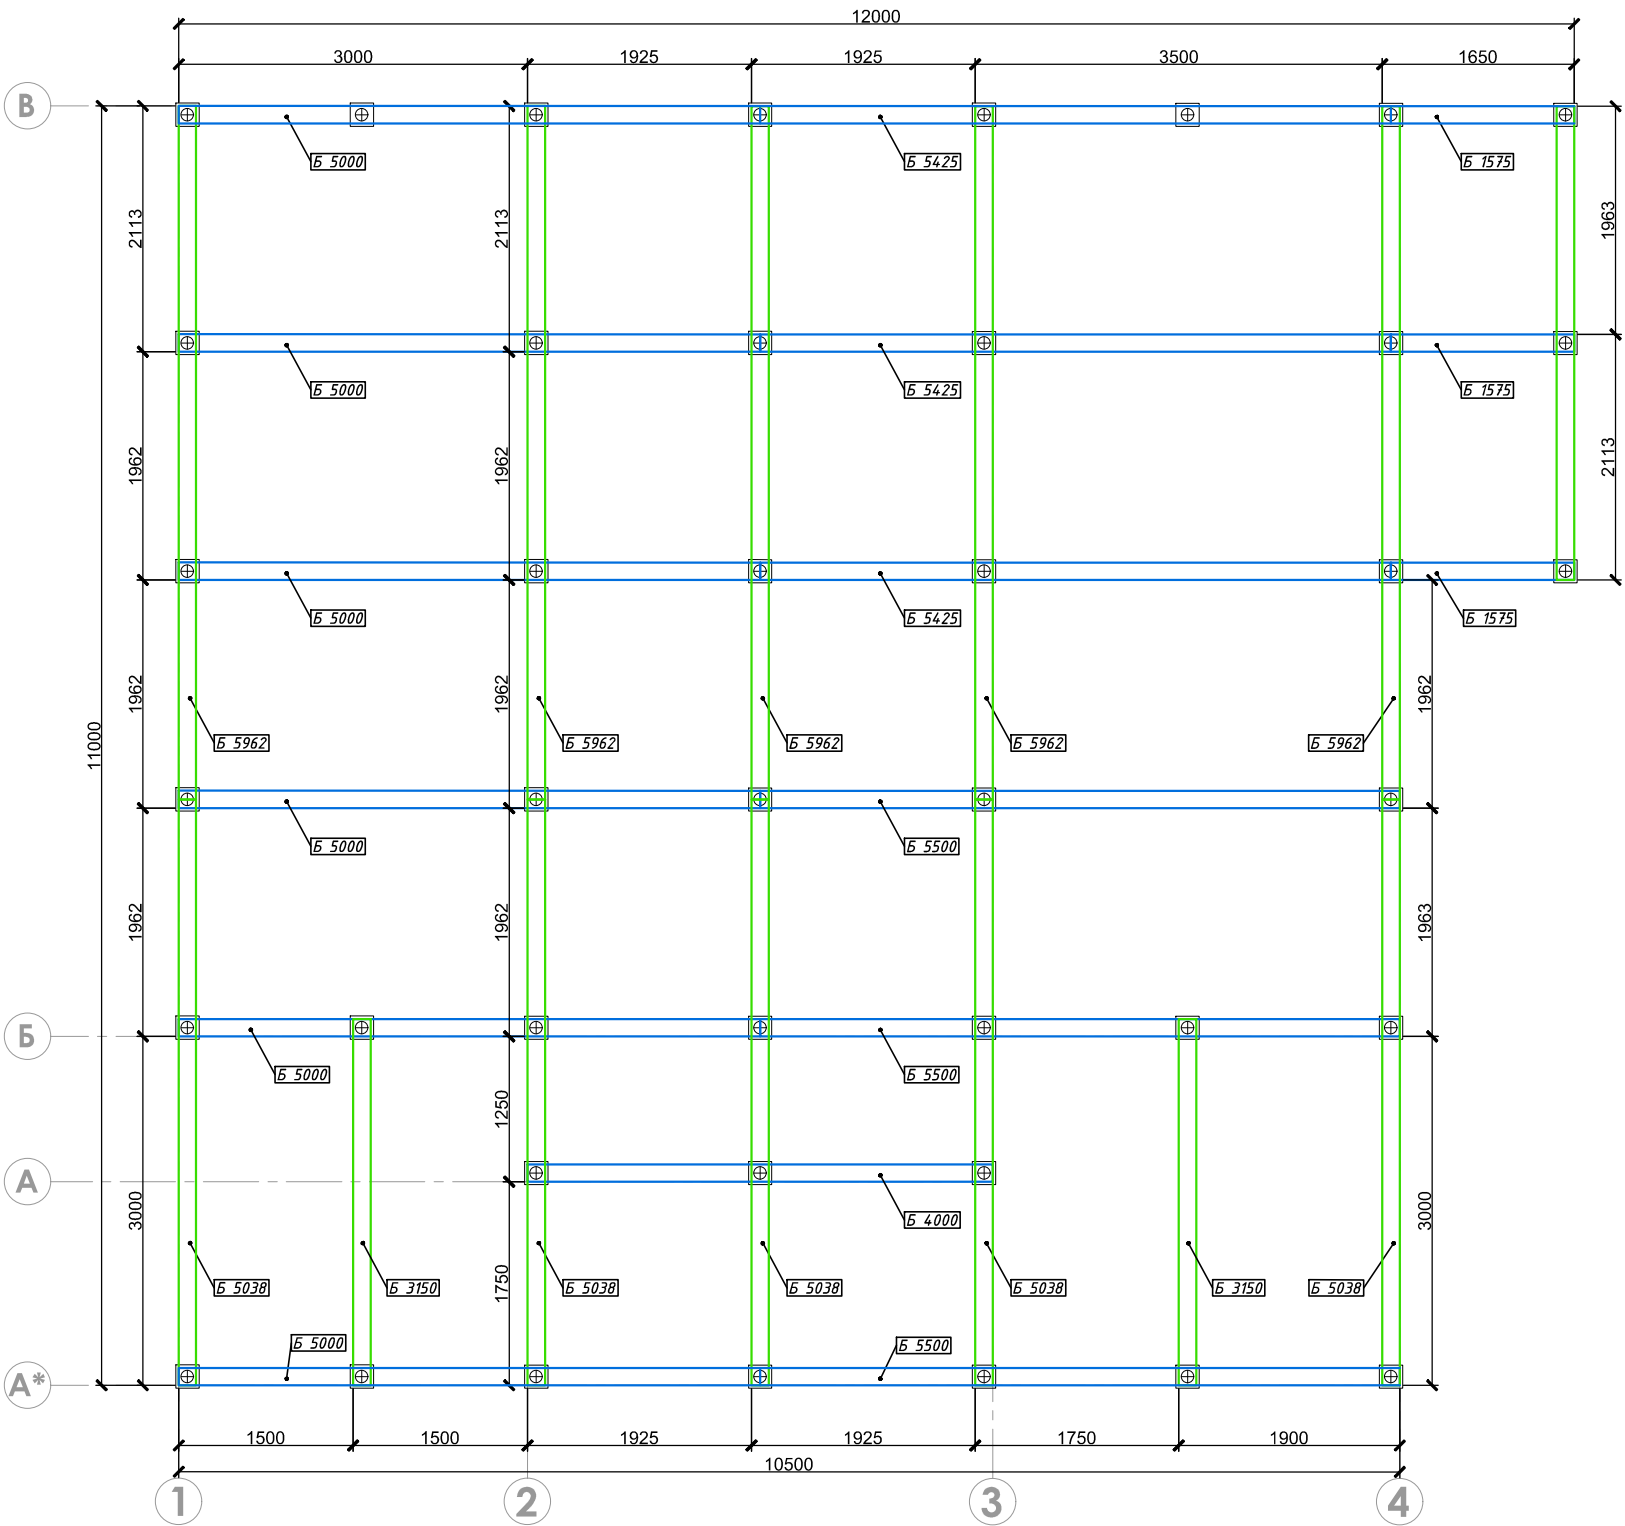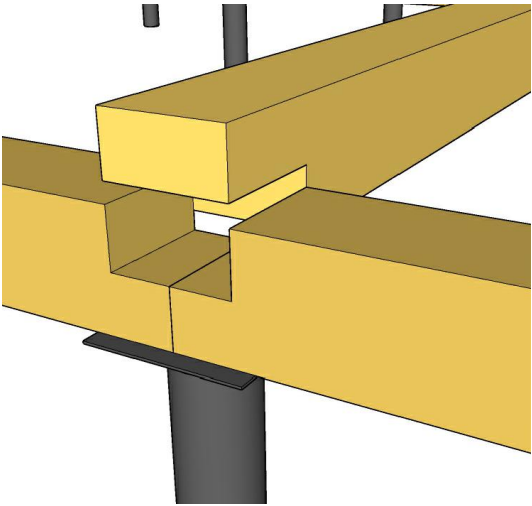

1. Обвязка свай из бруса общим сечением 150х150мм.
2. Обвязка на сваи укладывается через гидроизоляцию.
3. Крепление обвязки к свае осуществить анкерами.

Изм.	Кол. уч.	Лист	№ док.	Подп.	Дата	Лист
						7

Обвязка свай.

Платформа. Общий вид: обрешетка низа лаг пола 1-го, лаги пола 1-го этажа, бриджинги.




- 1. Перед установкой лаг пола 1-го этажа, по цокольной обвязке произвести обрешетку из строганой доски 150х25 мм.
- 2. Поверх обрешетки установить сетку от грызунов.
- 3. По сетке проложить пароизоляцию. После чего приступить к установке лаг пола 1-го этажа.
- 4. Уложить утеплитель по всему периметру "платформы" перекрытий пола 1-го этажа, с последующим слоем гидроизоляции и черновым полом (напольная доска 150х36 мм).

Кол. уч.	Лист	№ док.	Подп.	Дата	Платформа. Общий вид: обрешетка низа лаг пола 1-го, лаги пола 1-го этажа, бриджинги.	Лист
						8

Платформа 1-го этажа. Лаги пола.

Экспликация:


Маркировка	Длина	Ширина	Толщина	Кол-во
Д 5037	5037	200	40	2
Д 5963	5963	200	40	1
Д 3035	3035	200	40	1
Д 3850	3850	200	40	1
Д 5075	5075	200	40	1
Д 3995	3995	200	40	3
Д 1500	1500	200	40	1
Д 5923	5923	200	40	1
Д 5037	5037	200	40	1
Д 4960	4960	200	40	1
Д 5460	5460	200	40	1
Д 5035	5035	200	40	2
Д 5535	5535	200	40	2
Д 3110	3110	200	40	8
Д 4000	4000	200	40	8
Д 3920	3920	200	40	1
Д 3610	3610	200	40	8
Д 5035	5035	200	40	7
Д 5535	5535	200	40	7

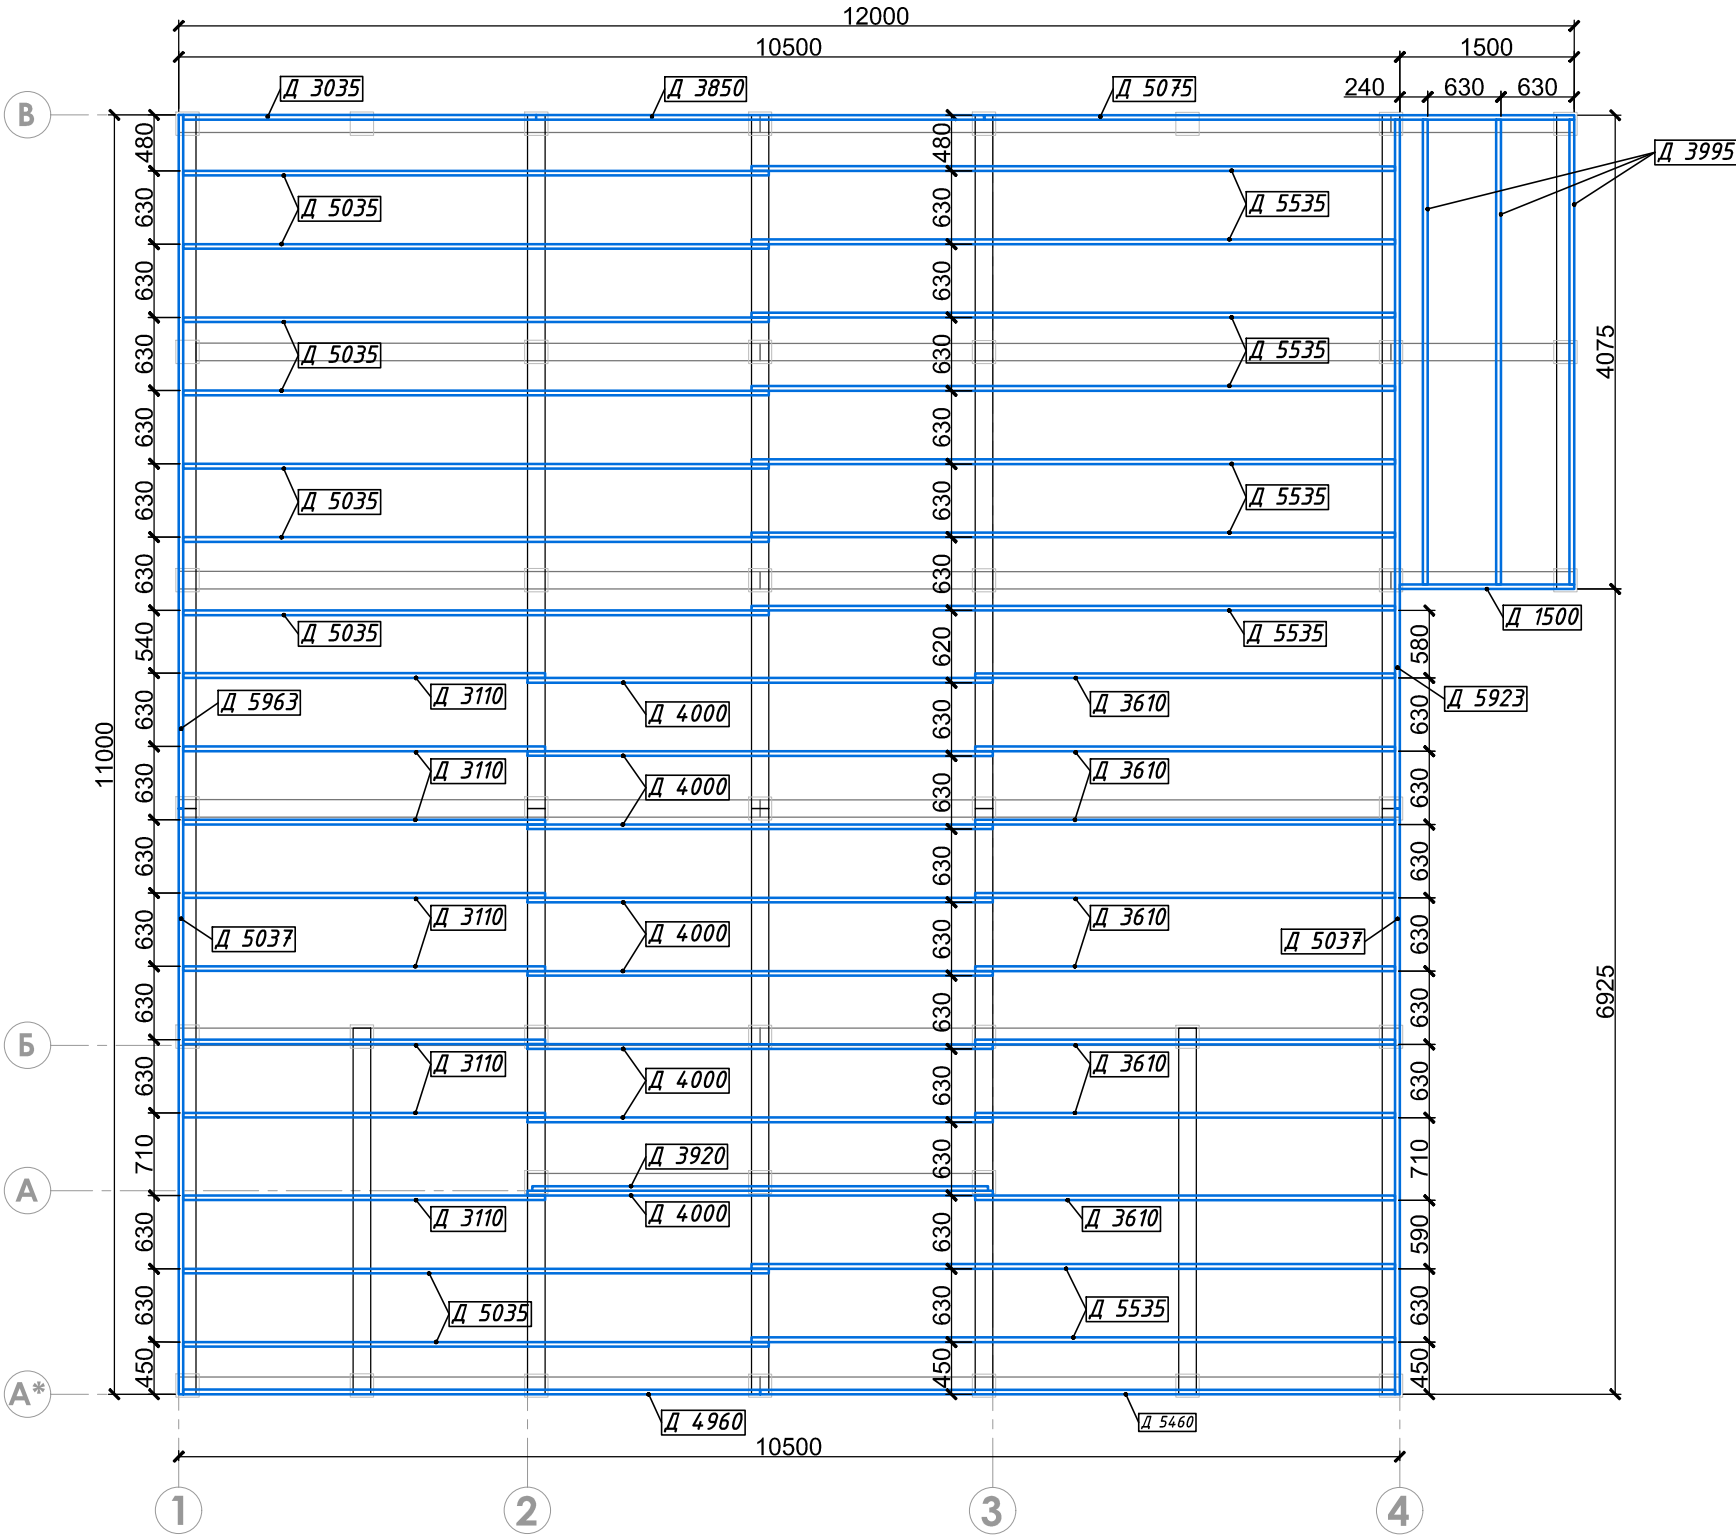

1. Каркасы перекрытий и стен собираются на гвозди не менее 88 мм.
2. Для соединения досок в каркасе стен и перекрытий рекомендуется использовать не менее 1-го гвоздя на каждые 5 см ширины доски.
3. Использование чёрных (калёных) саморезов в качестве основного крепежа во всех элементах каркаса НЕ ДОПУСКАЕТСЯ!

Изм.	Кол. уч.	Лист	№ док.	Подп.	Дата	Платформа 1-го этажа. Лаги пола.	Лист
							9

Стены 1-го этажа. Общий вид.

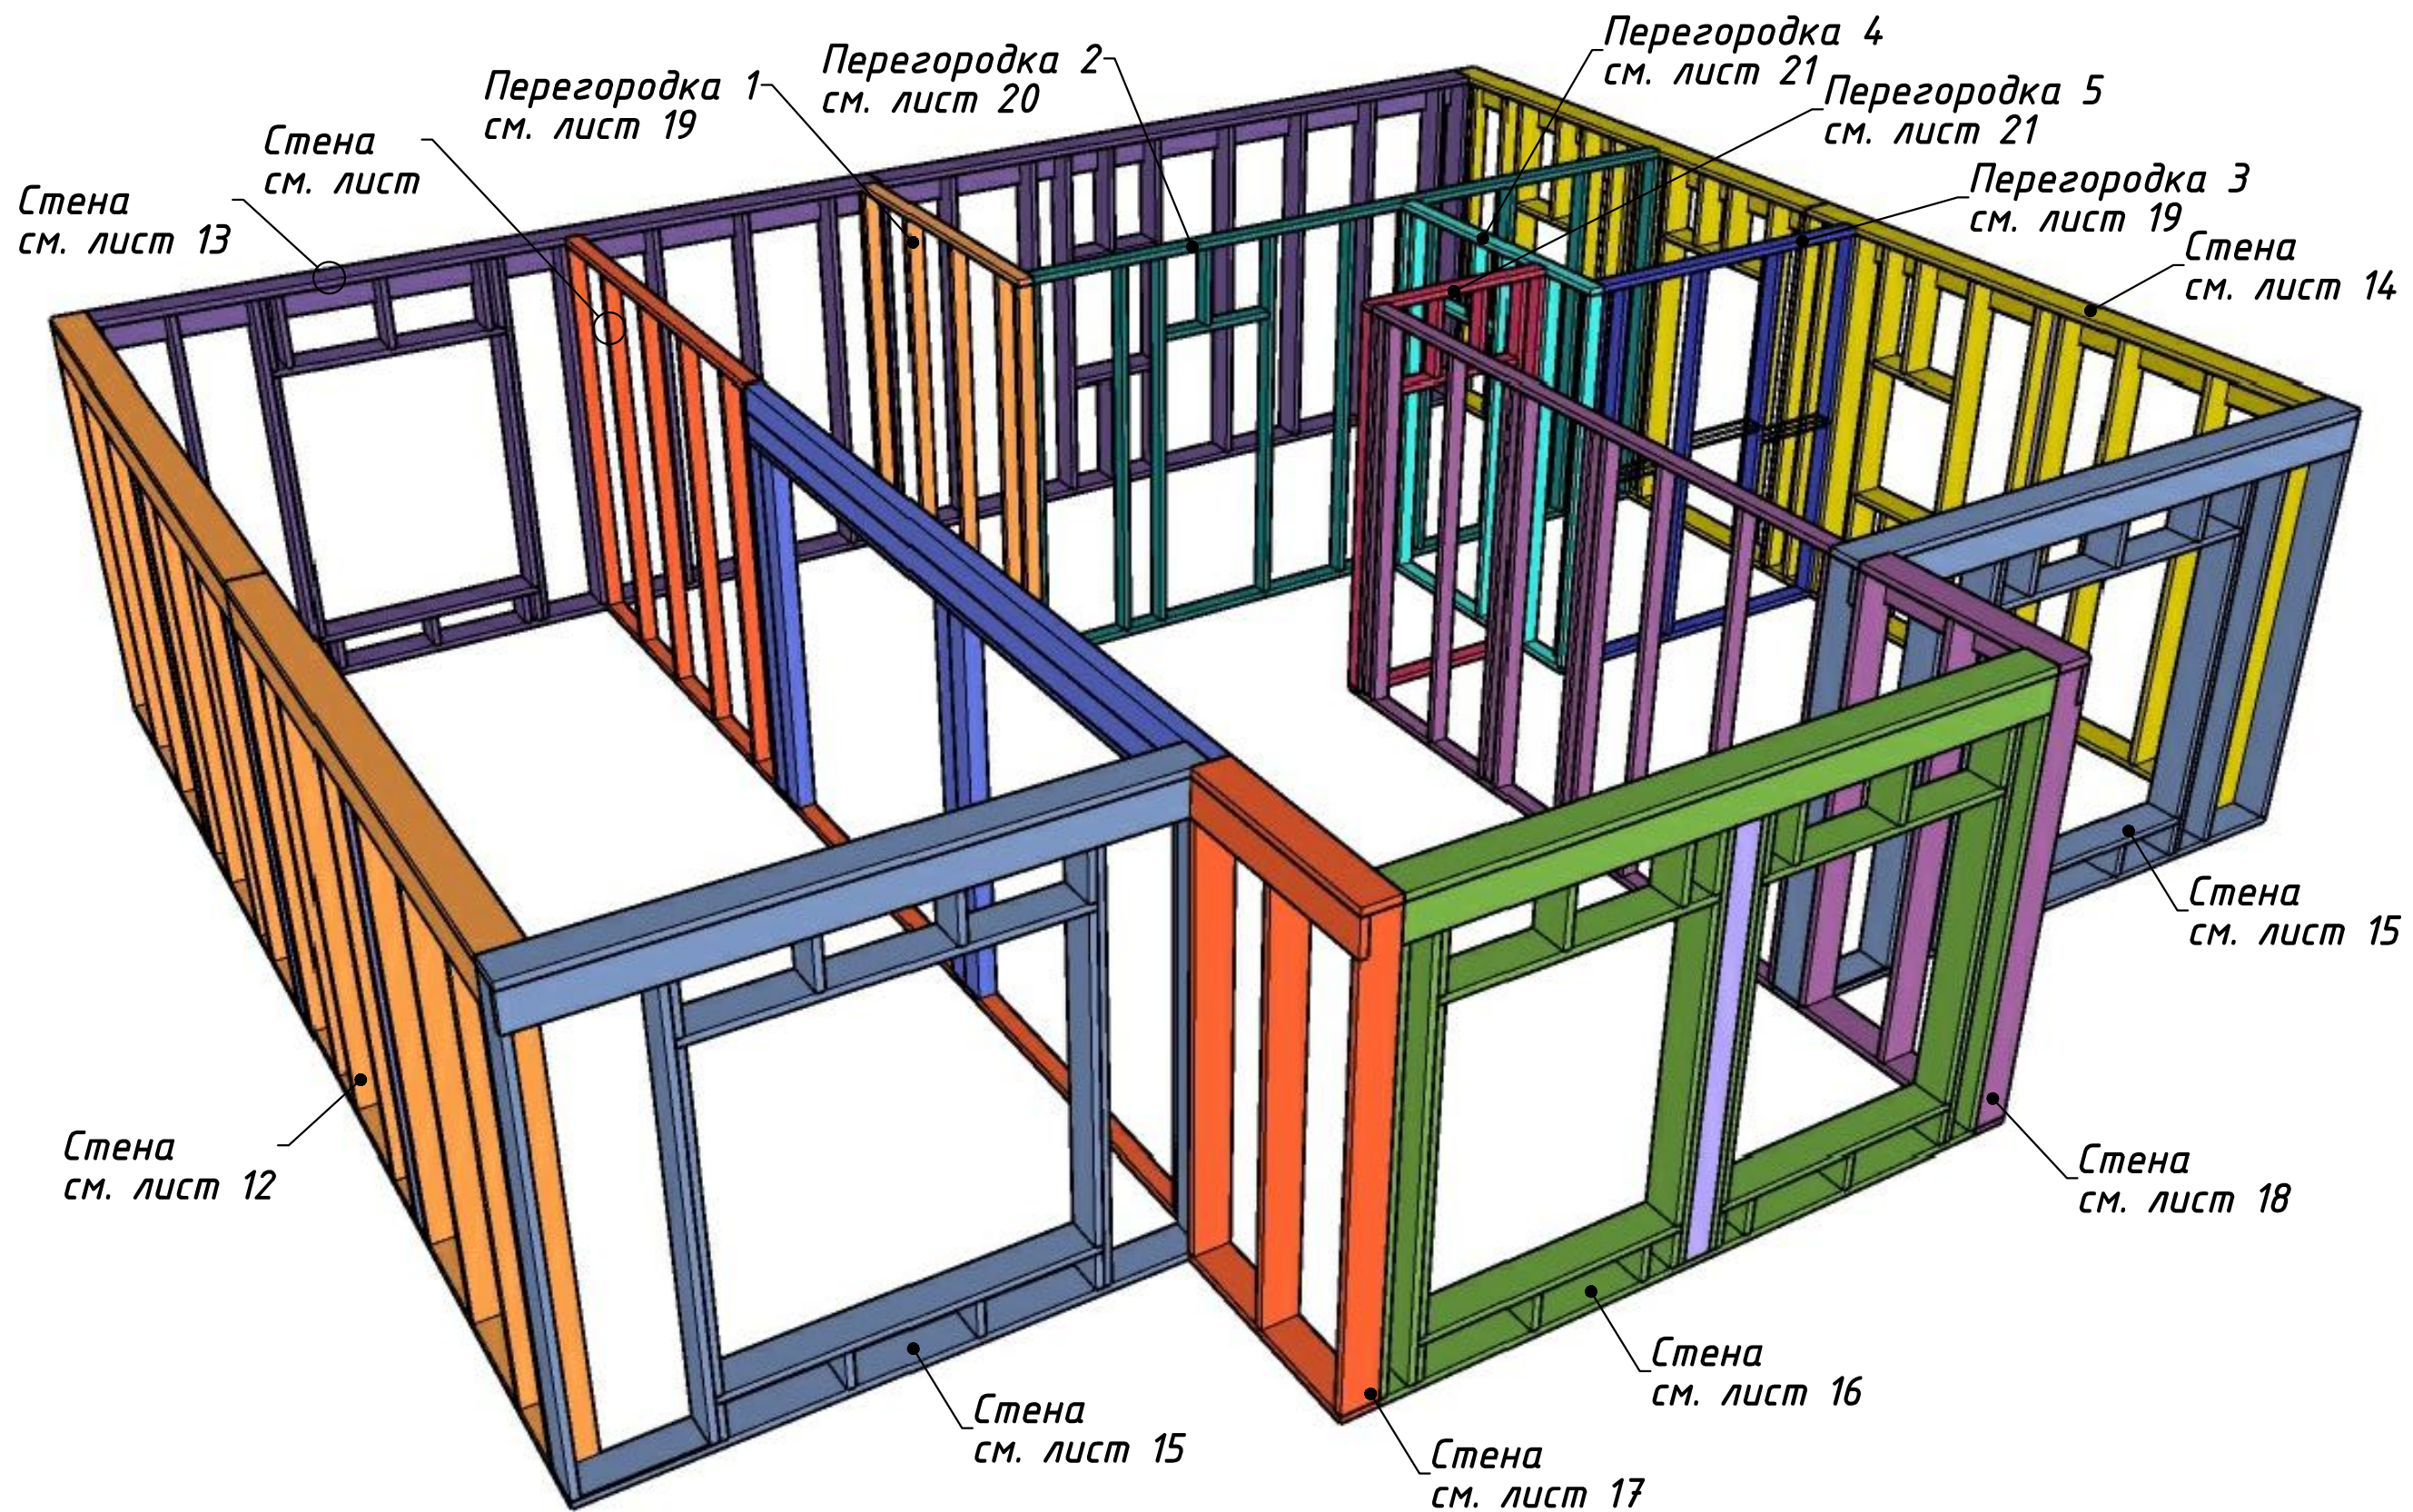

Рекомендация!

После установки внешних стен - закрепить полосы пароизоляции в места примыкания внутренних стен (с выпуском 4-5 см), для дальнейшего монтажа непрерывного контура пароизоляции дома.

Для возведения 2-х этажного мансардного дома проектом рекомендуется установка бриджингов в каркасе стен и перегородок. Возможно заменить на цкосины с врезкой.


Изм.	Кол. уч.	Лист	№ док.	Подп.	Дата

Стены 1-го этажа. Общий вид.


Луст

11

Стена по оси 1 (1-й этаж).

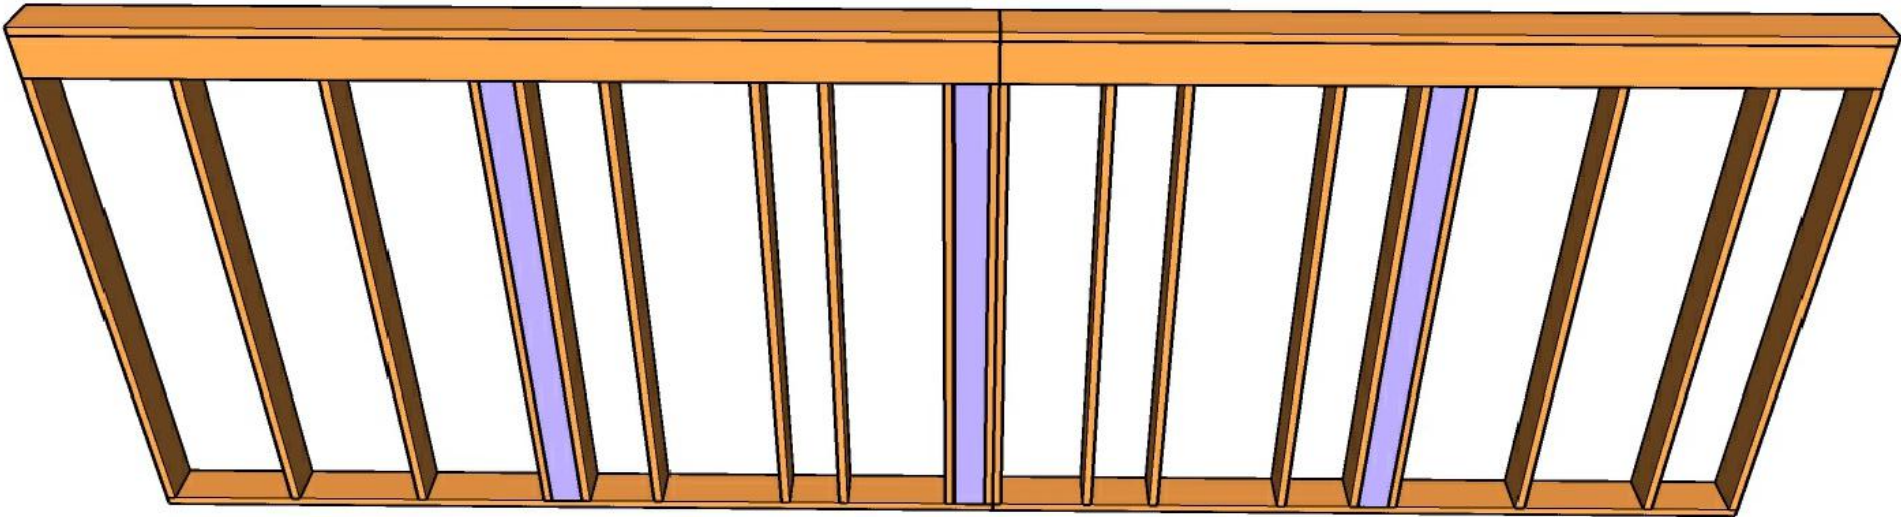


Расположение элементов каркаса.

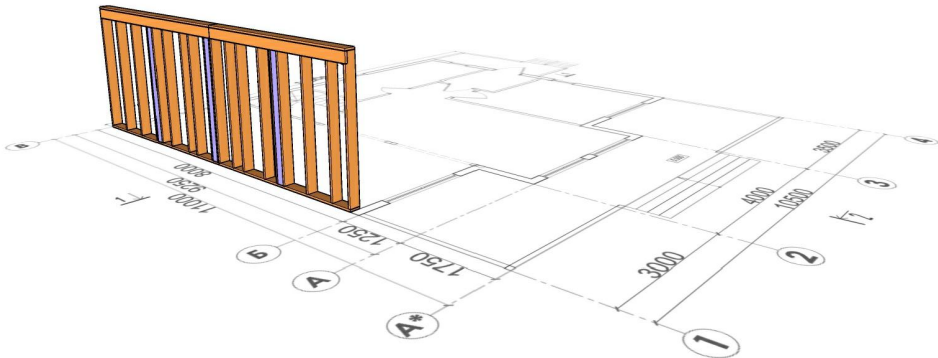


Экспликация:

Маркировка	Длина	Ширина	Толщина	Кол-во
Д 4115	4115	200	40	3
Д 3685	3685	200	40	3
Д 2560	2560	200	40	19
Д 2560	2560	150	40	3
Д 2400	2600	150	40	3

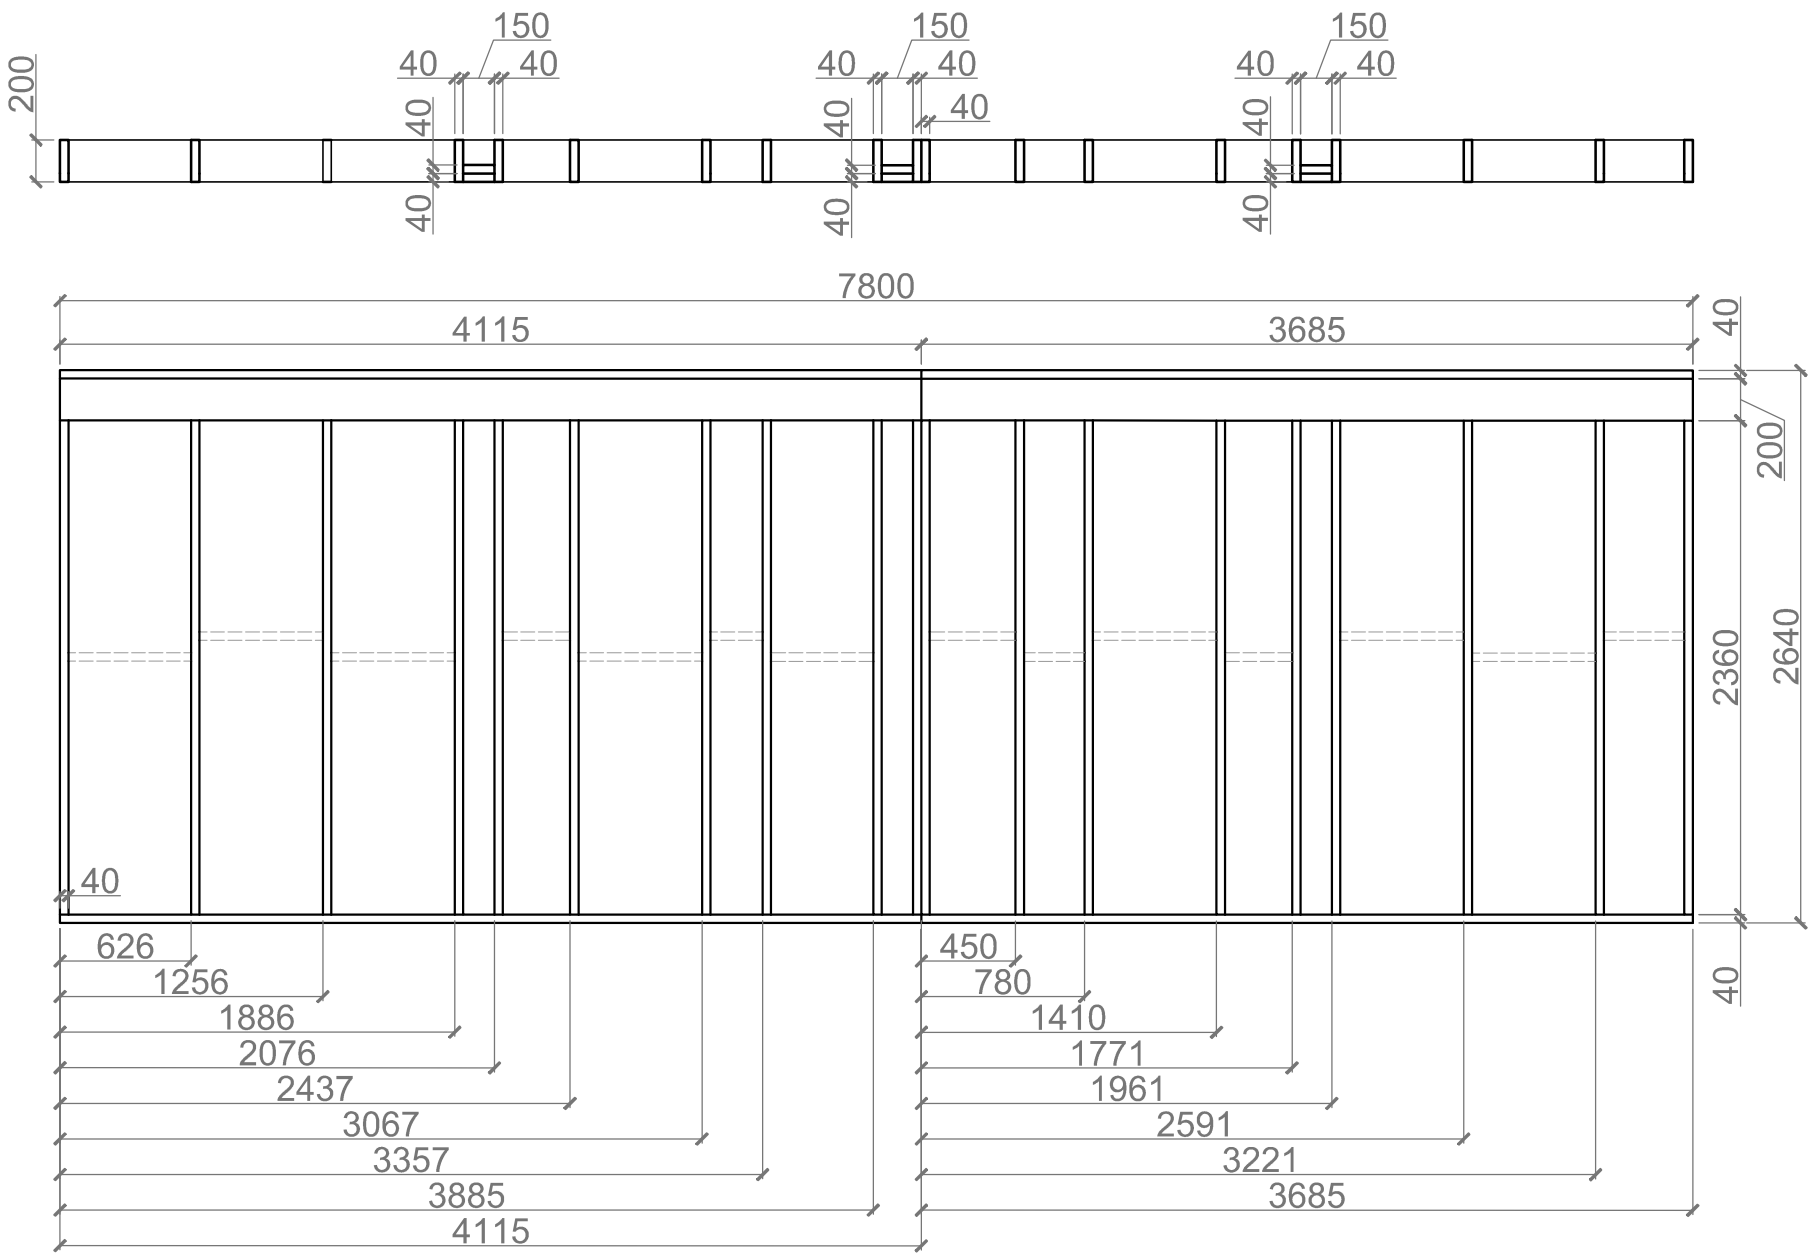

Изм.	Кол. уч.	Лист	№ док.	Подп.	Дата	Стена по оси 1 (1-й этаж).	Лист
							12

Расположение элементов каркаса.

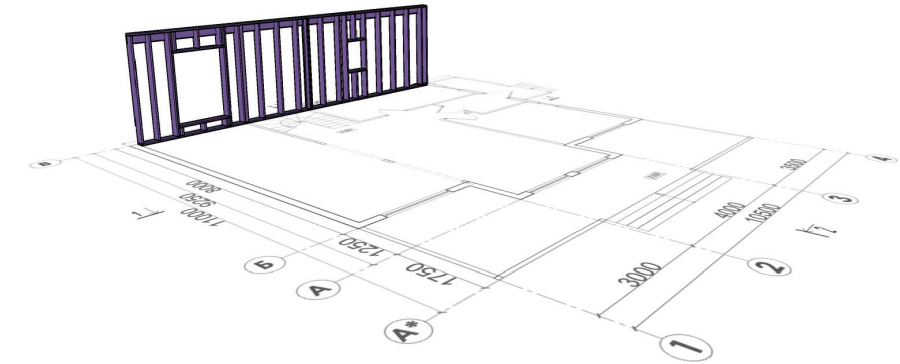

This architectural drawing shows a detailed elevation of a building facade. The drawing includes a top section with a height of 200 units and a main section with a height of 2640 units. The total width is 10100 units, divided into two main sections: 4960 units on the left and 5140 units on the right. The drawing features a central vertical axis and a horizontal axis. The left section contains a large rectangular opening with a width of 700 units and a height of 900 units. The right section contains a large rectangular opening with a width of 1400 units and a height of 1800 units. The drawing also includes various structural elements, such as columns and beams, and is annotated with numerous dimensions and labels.

Top Section Dimensions:

- Overall height: 200
- Overall width: 10100
- Left section width: 4960
- Right section width: 5140

Main Section Dimensions:

- Overall height: 2640
- Overall width: 10100
- Left section width: 4960
- Right section width: 5140

Structural Elements and Annotations:


- Central vertical axis: 10100
- Horizontal axis: 2640
- Left section opening: 700 (width) x 900 (height)
- Right section opening: 1400 (width) x 1800 (height)
- Dimensions along the bottom: 870, 1500, 2130, 2760, 3150, 3500, 3780, 4410, 4960 (left); 350, 980, 1610, 2240, 2660, 2780, 3410, 4040, 4140, 4670, 5140 (right)
- Dimensions along the right side: 40, 2360, 2640, 40
- Dimensions along the top: 40, 40, 100, 100, 40, 80, 40, 40, 40, 60, 80

Маркировка	Длина	Ширина	Толщина	Кол-во
Д 5140	5140	200	40	3
Д 4960	4960	200	40	3
Д 2560	2560	200	40	19
Д 2560	2560	100	40	2
Д 1800	1800	200	40	2
Д 1480	1480	200	40	2
Д 850	850	200	40	1
Д 770	770	200	40	1
Д 700	700	200	40	2
Д 470	470	200	40	5
Д 210	210	200	40	5


Изм.	Кол. уч.	Лист	№ док.	Подп.	Дата

Лист
13

Стена по оси 4 (1-й этаж).

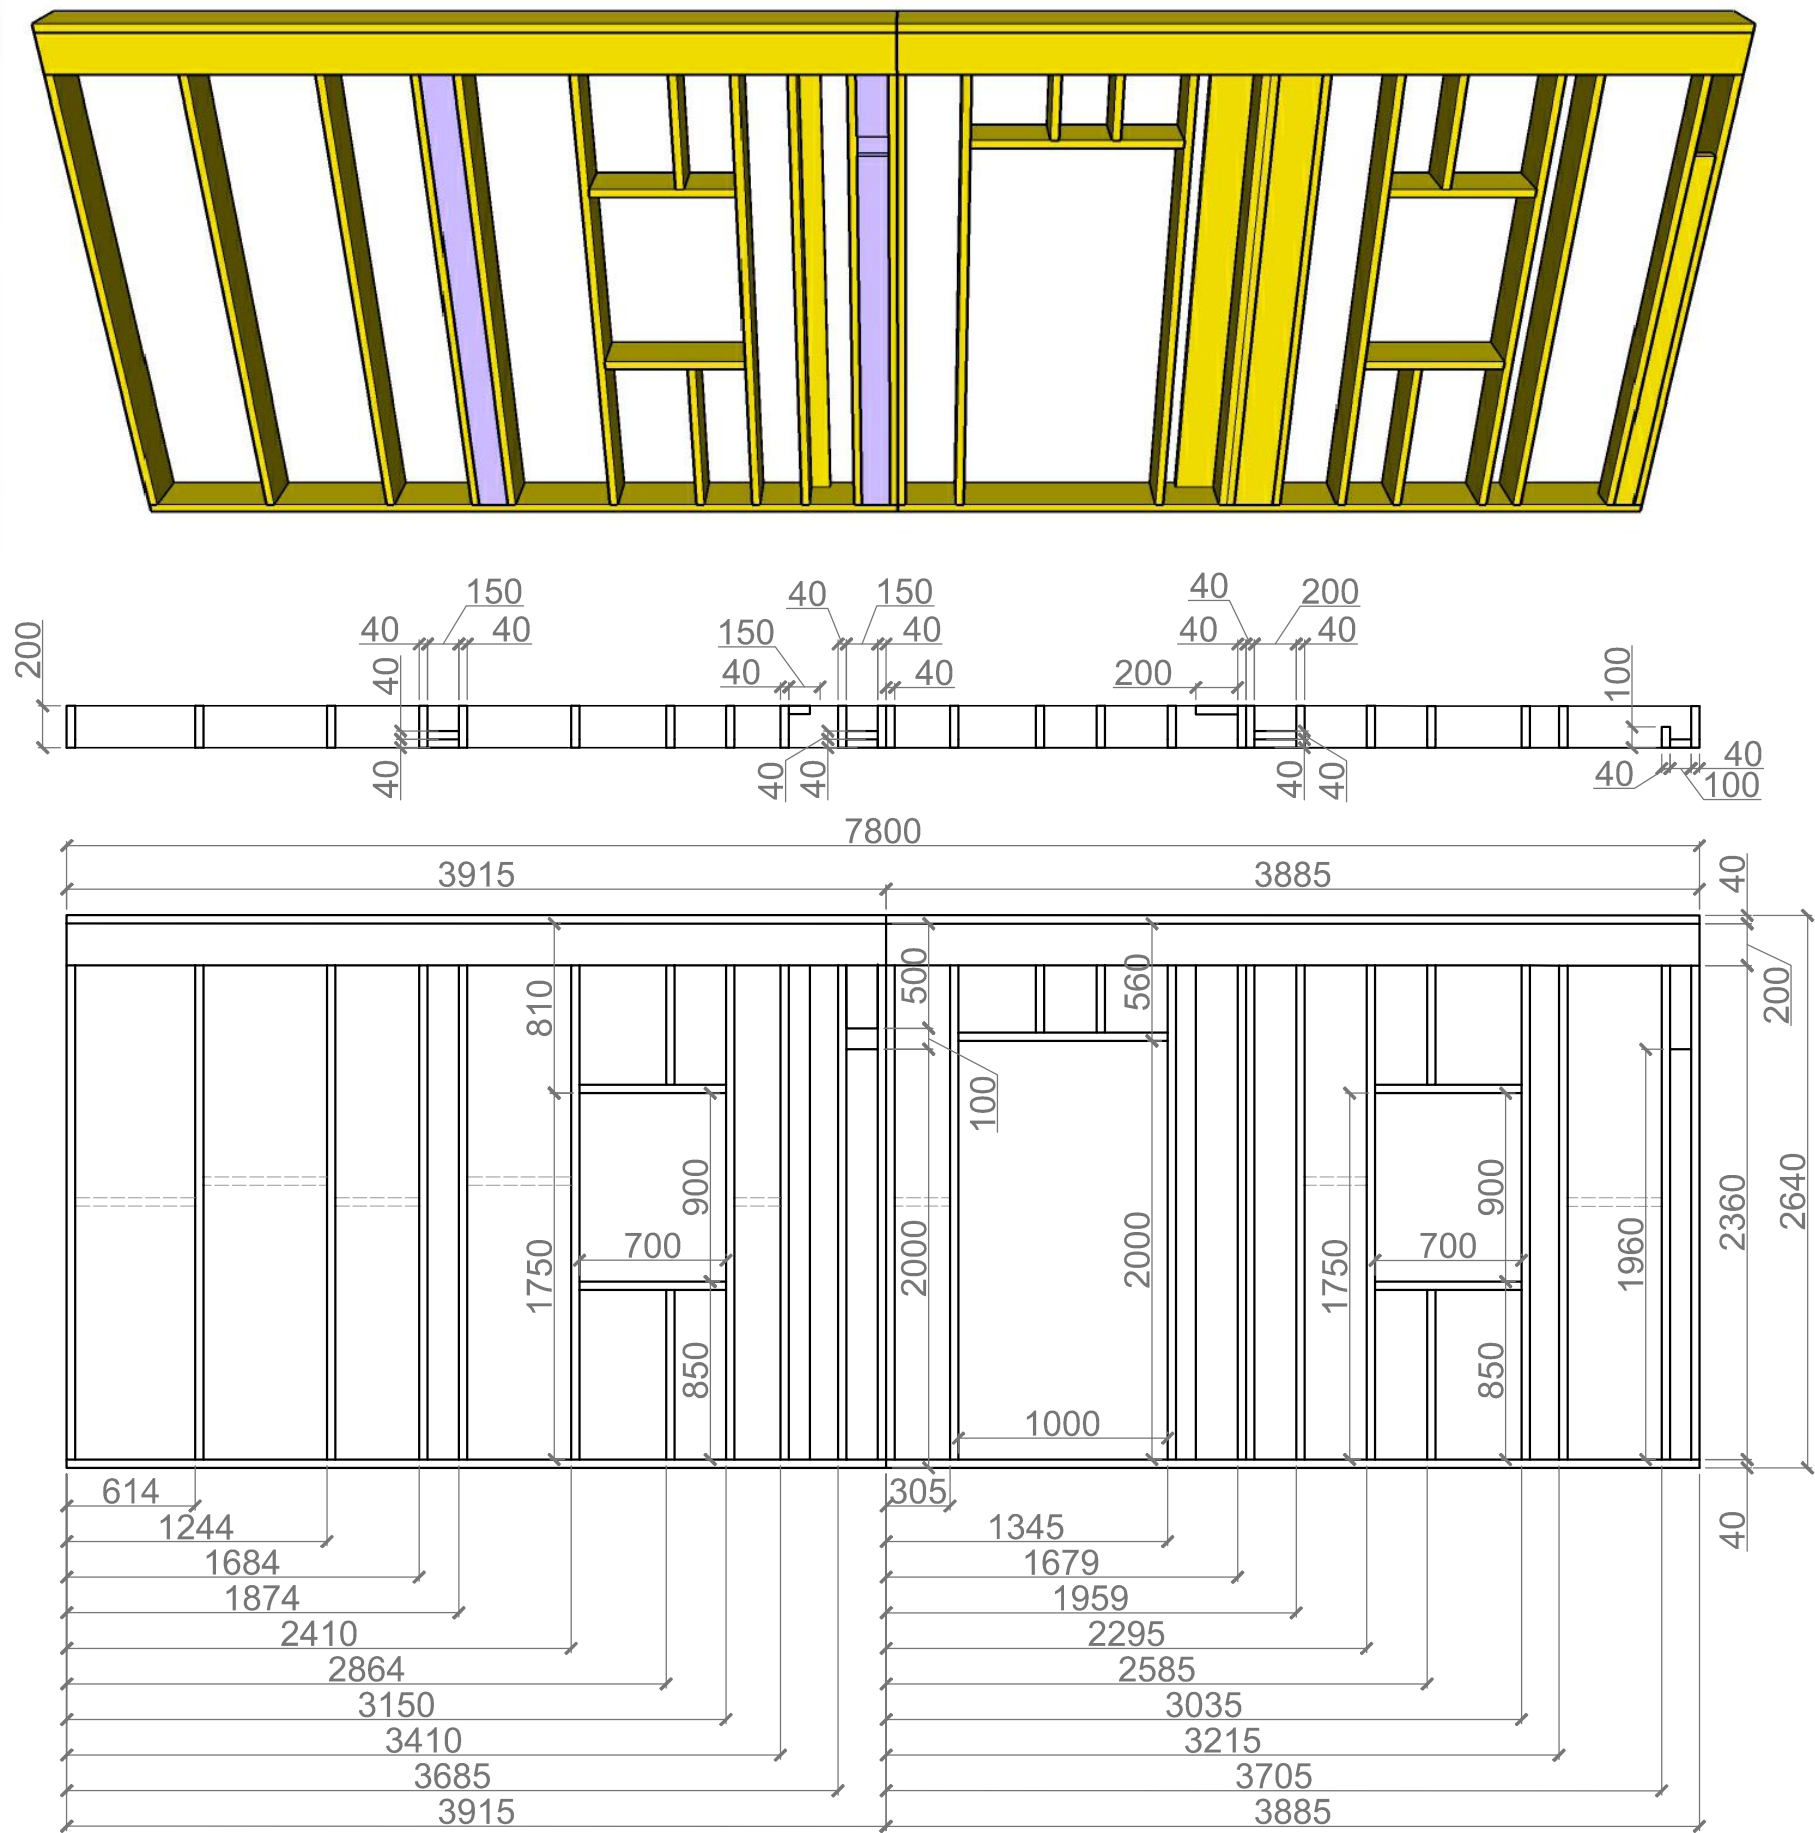

Расположение элементов каркаса.

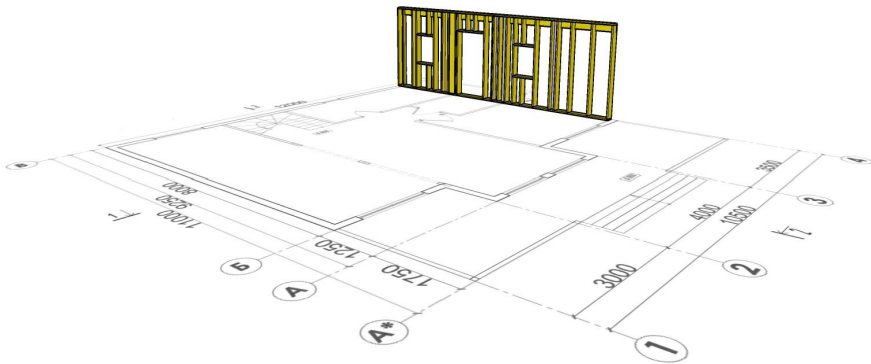


Экспликация:


Маркировка	Длина	Ширина	Толщина	Кол-во
Д 3915	3915	200	40	3
Д 3885	3885	200	40	3
Д 2560	2560	200	40	23
Д 2560	2560	150	40	2
Д 2360	2360	150	40	1
Д 2000	2000	150	40	1
Д 300	300	150	40	1
Д 2560	2560	100	40	2
Д 1960	1960	100	40	1
Д 1000	1000	200	40	1
Д 850	850	200	40	2
Д 770	770	200	40	2
Д 520	520	200	40	2

Изм.	Кол. уч.	Лист	№ док.	Подп.	Дата	Стена по оси 4 (1-й этаж).	Лист
							14

Стена по оси Б (1-й этаж).

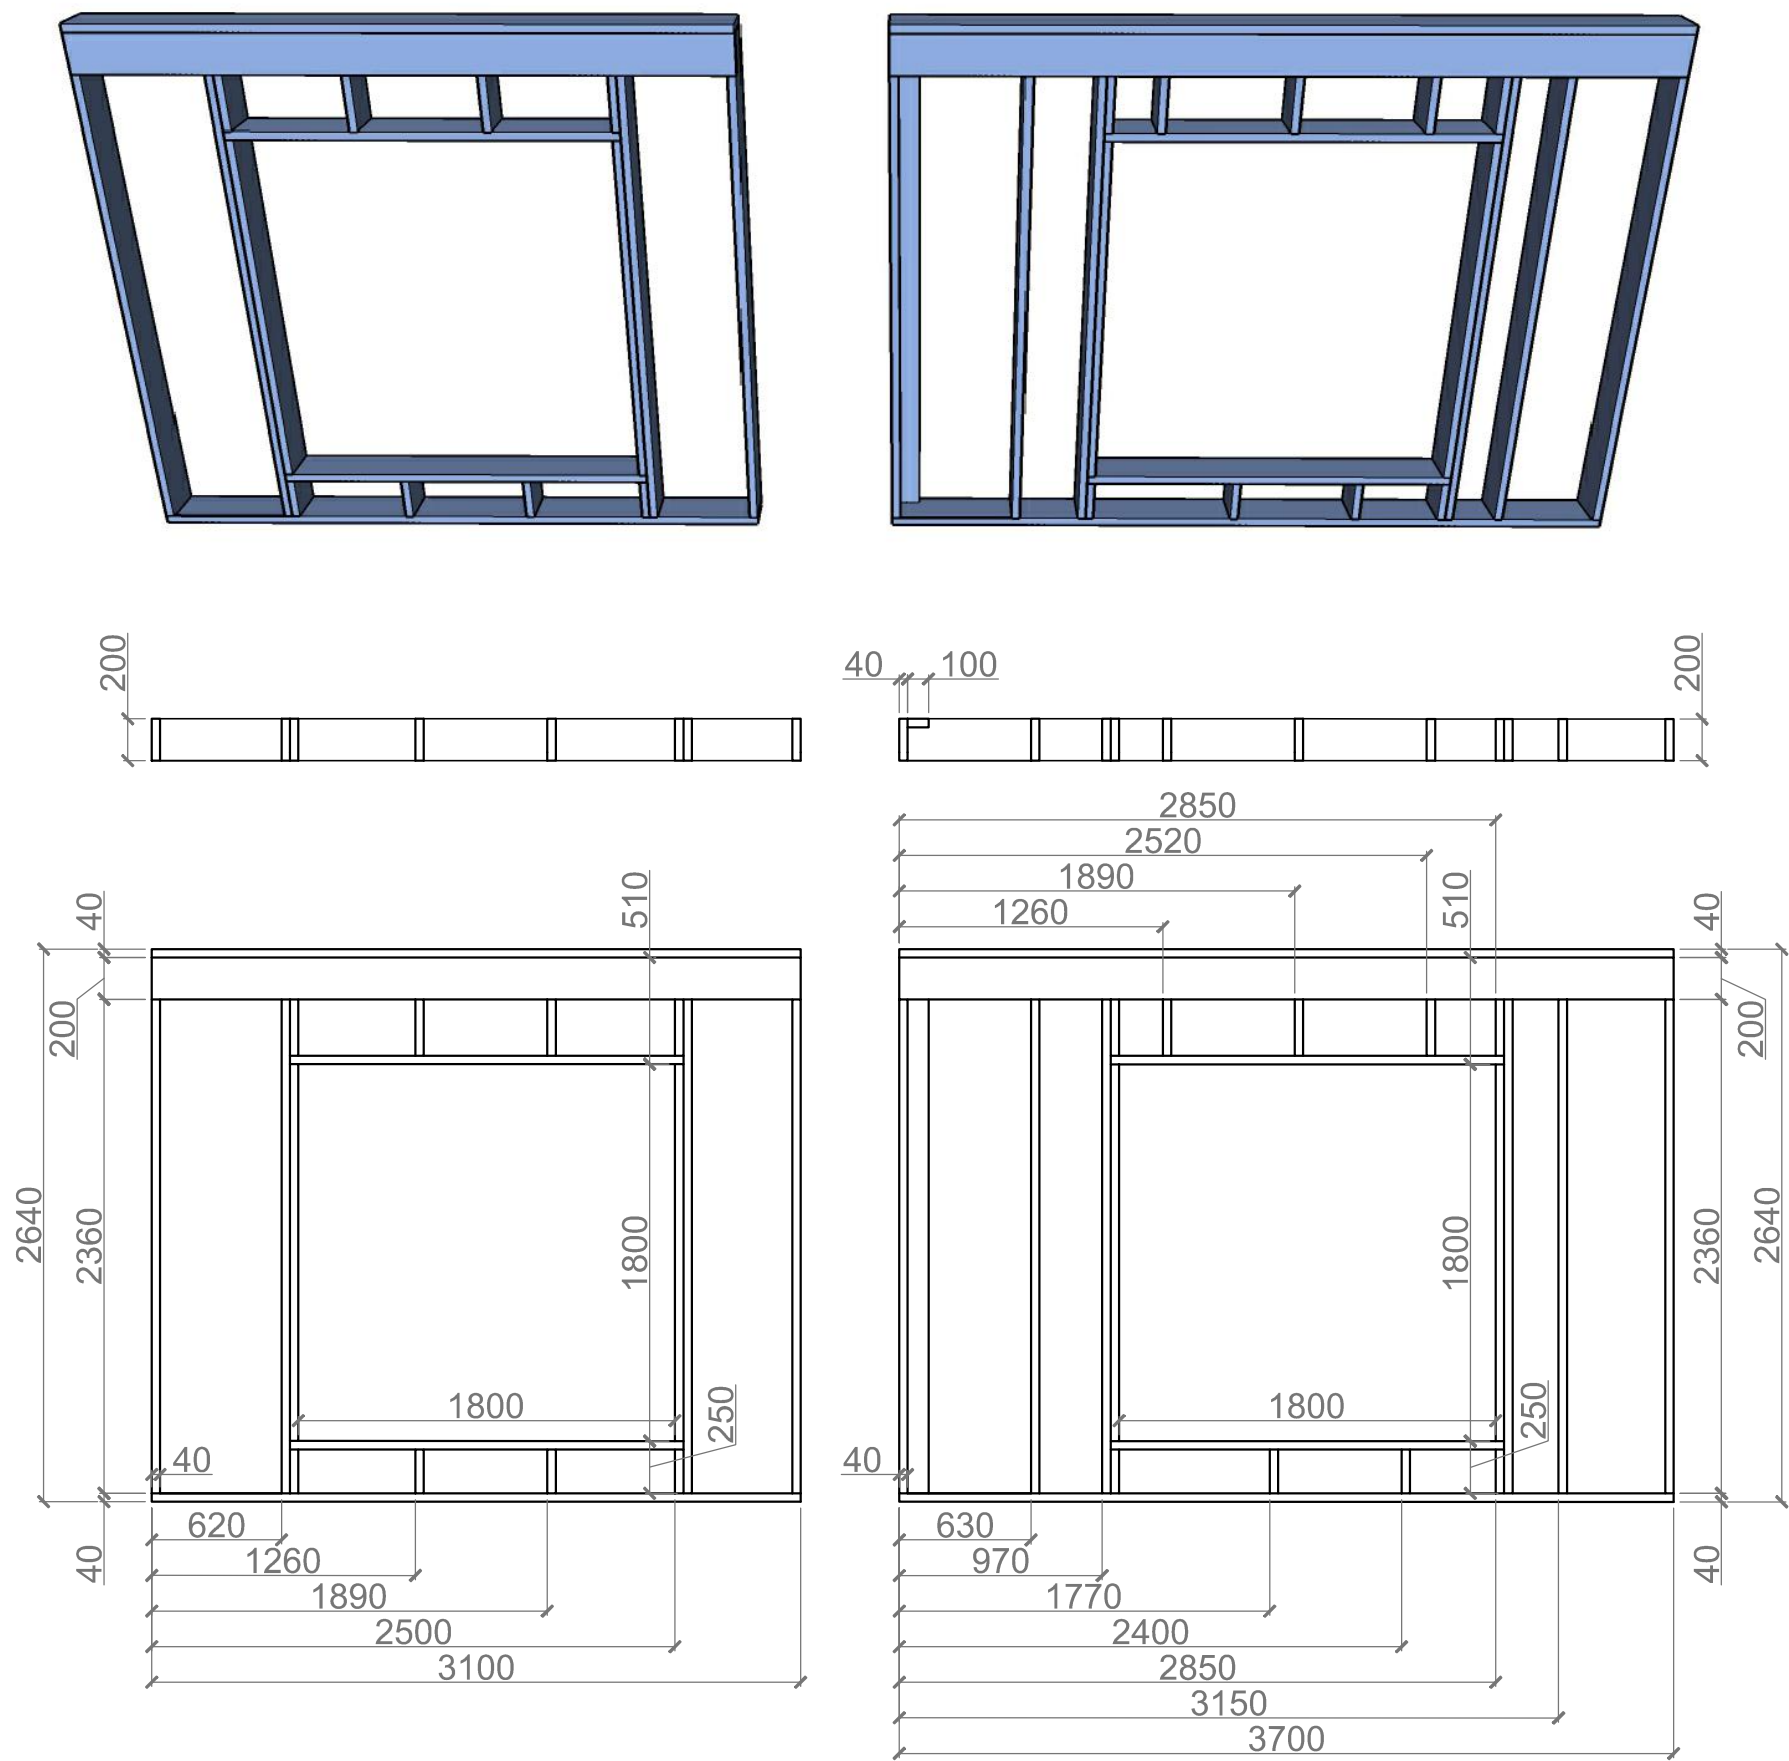




Расположение элементов каркаса.

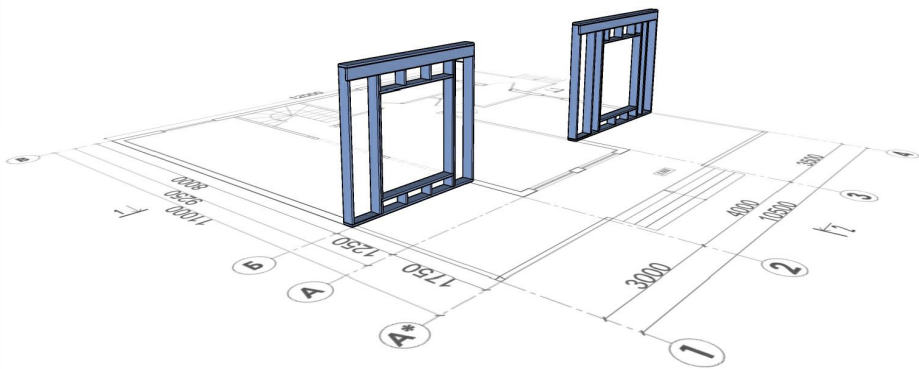


Экспликация:

Маркировка	Длина	Ширина	Толщина	Кол-во
Д 3700	3700	200	40	3
Д 3100	3100	200	40	3
Д 2560	2560	200	40	10
Д 1880	1880	200	40	4
Д 1800	1800	200	40	4
Д 470	470	200	40	9
Д 210	210	200	40	8
Д 2560	2560	100	40	1

Стена по оси А (1-й этаж).

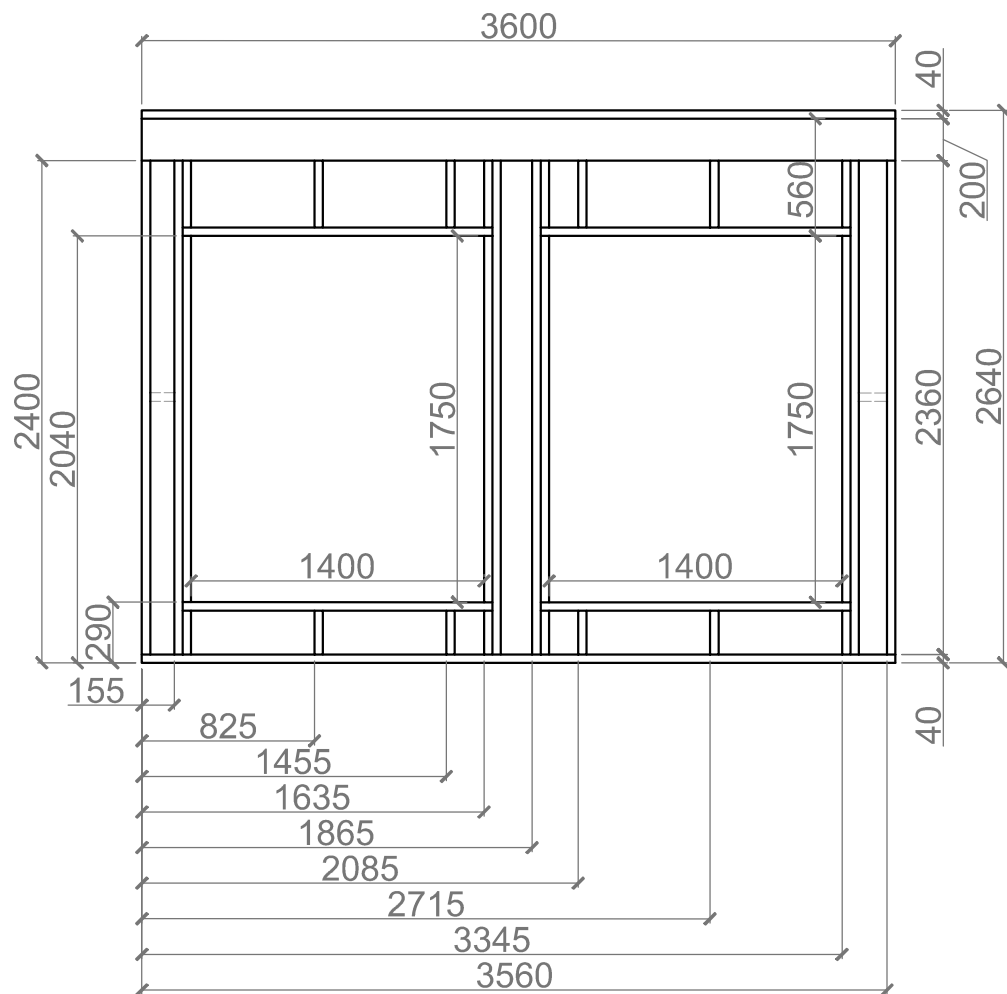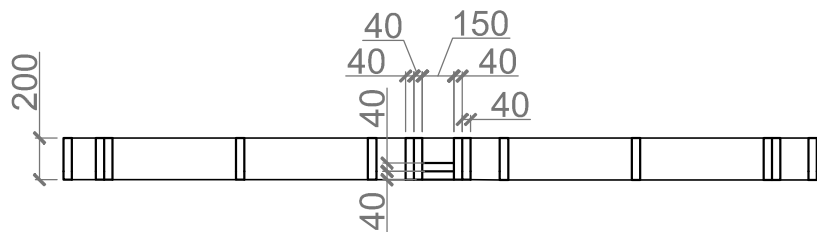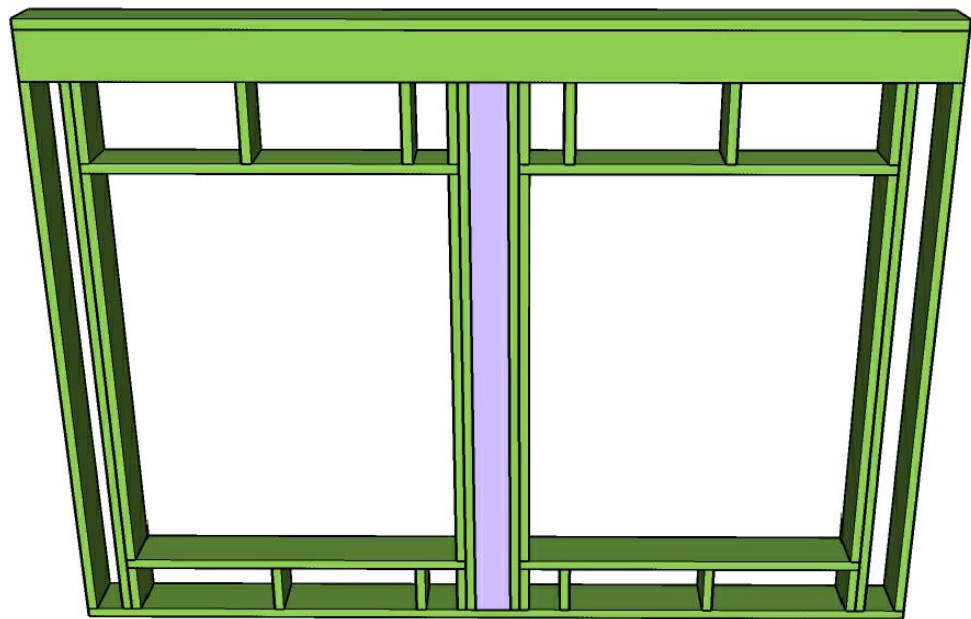

Расположение элементов каркаса.

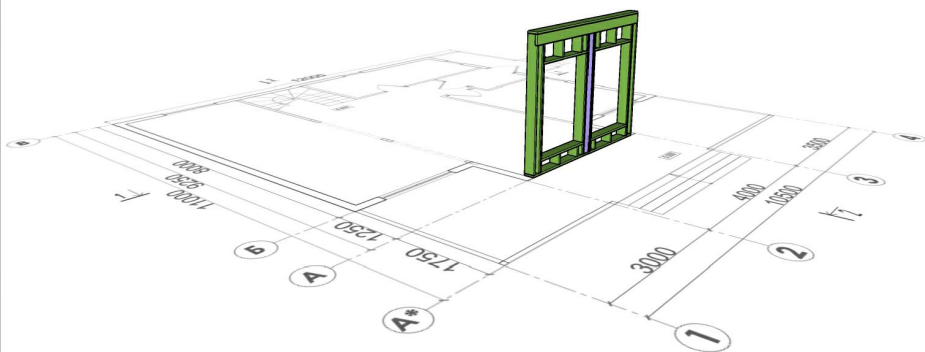


Экспликация:


Маркировка	Длина	Ширина	Толщина	Кол-во
Д 3600	3600	200	40	3
Д 2560	2560	200	40	6
Д 2560	2560	150	40	1
Д 2360	2360	150	40	1
Д 1750	1750	200	40	4
Д 1480	1480	200	40	4
Д 520	520	200	40	8
Д 210	210	200	40	8

Изм.	Кол. уч.	Лист	№ док.	Подп.	Дата	Стена по оси А (1-й этаж).	Лист
							16

Стена по оси 2 (1-й этаж).

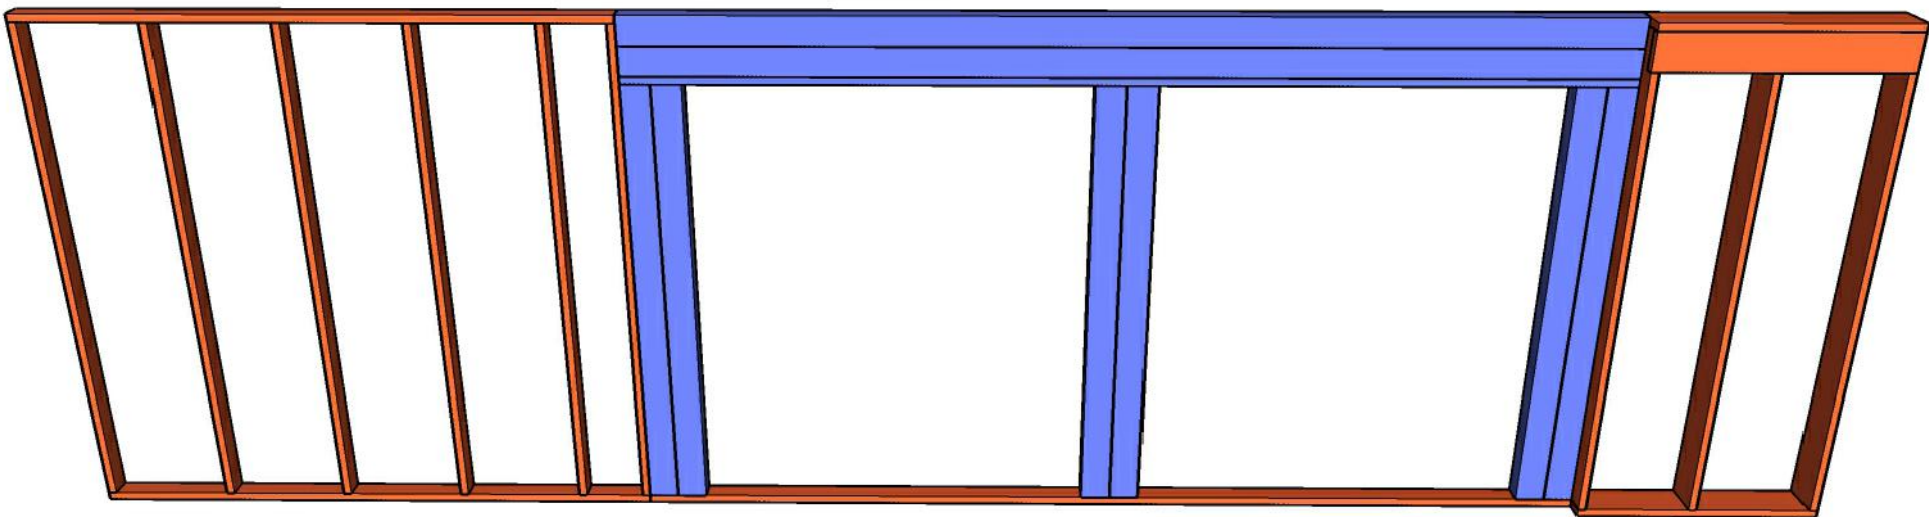


Расположение элементов каркаса.


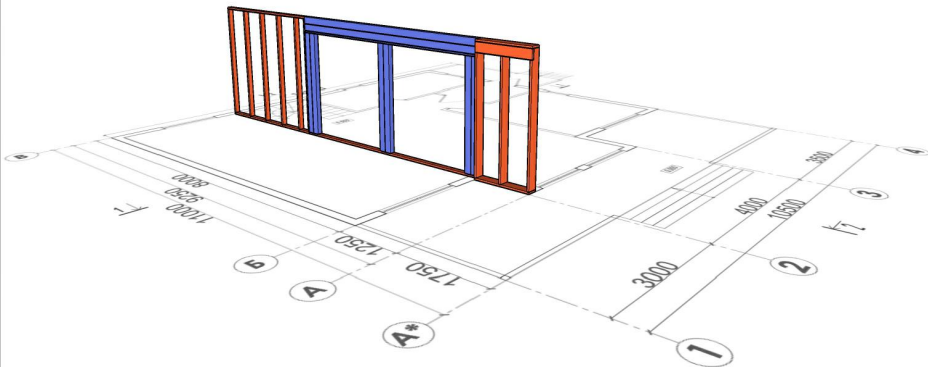


Экспликация:


Маркировка	Длина	Ширина	Толщина	Кол-во
Д 1250	1250	200	40	3
Д 2560	2560	200	40	3
Д 4900	4900	100	40	2
Б 4900	4900	100	150	2
Б 2260	2260	100	150	6
Д 2900	2900	100	40	2
Д 2560	2560	100	40	6

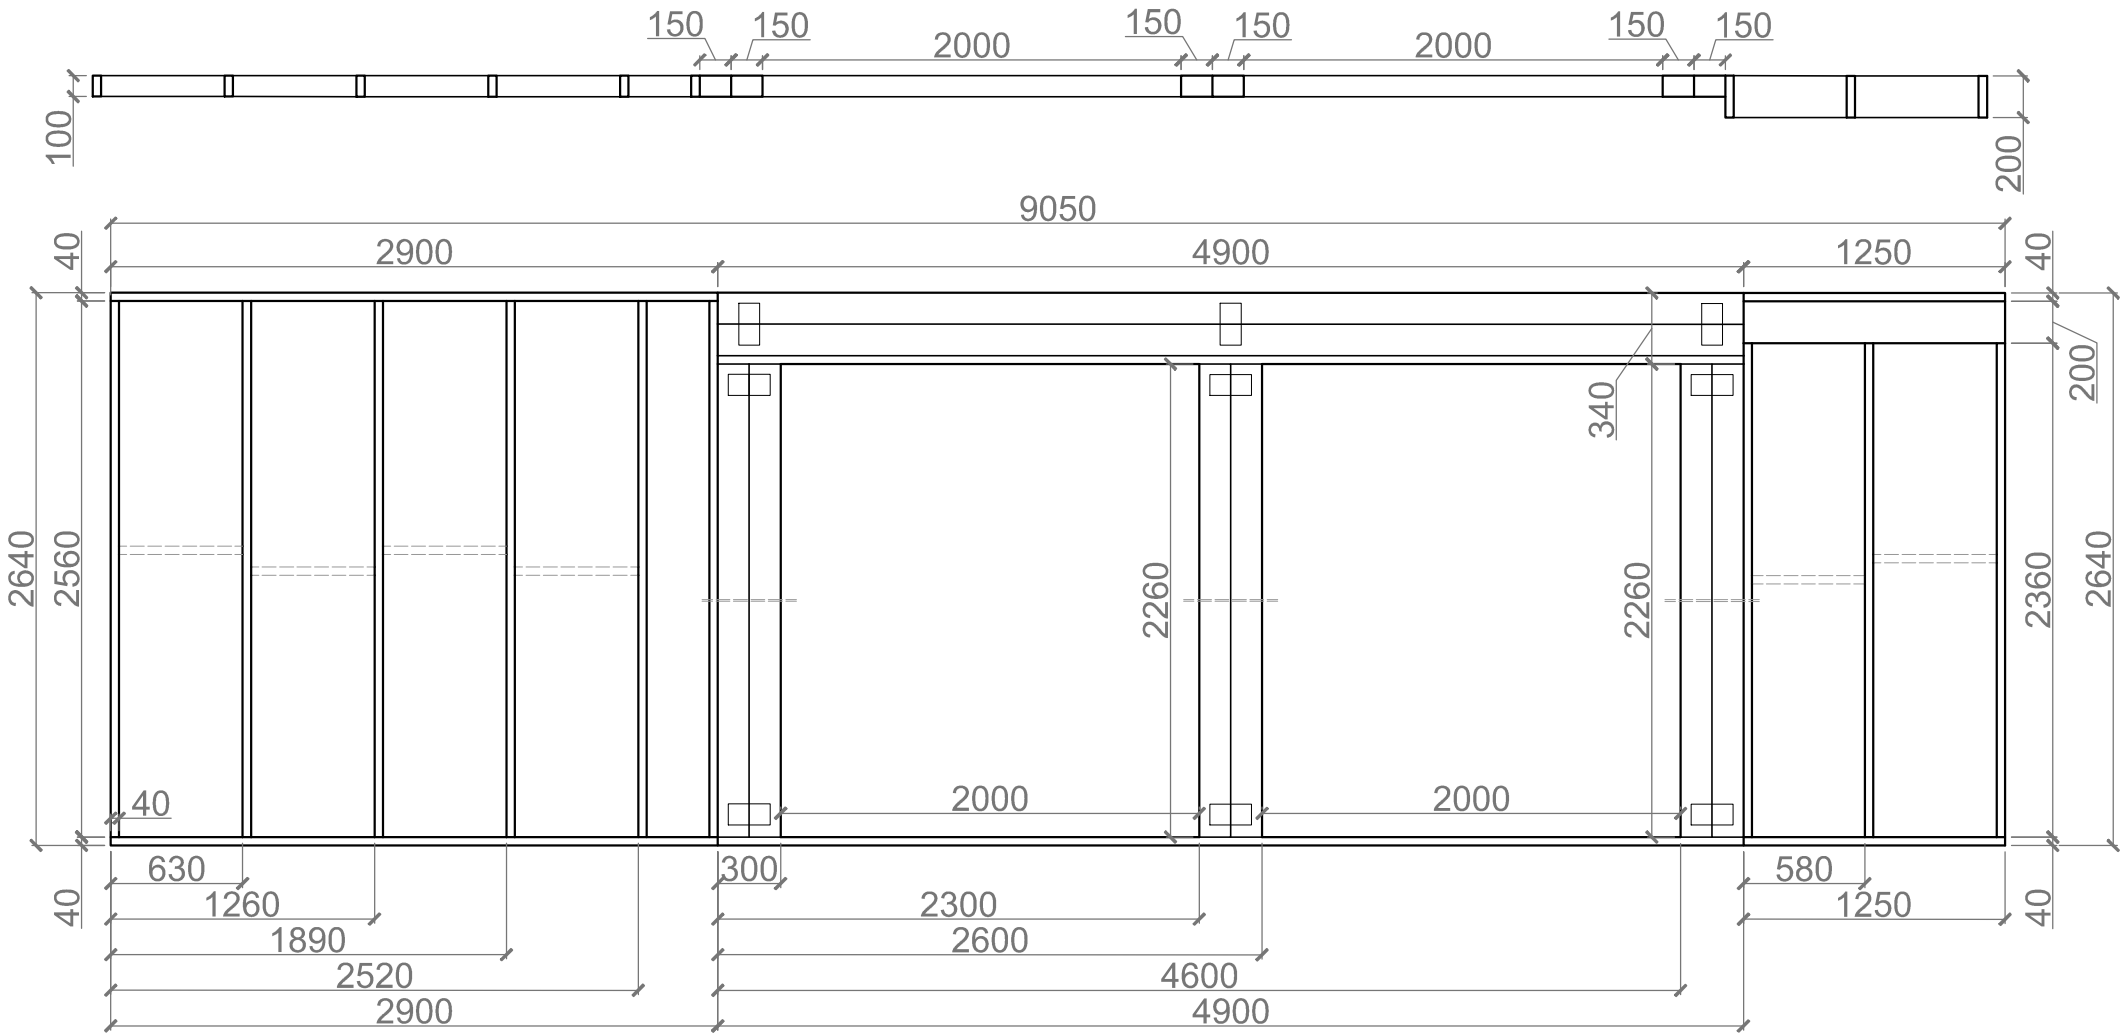

Перегородка 1 (1-й этаж).

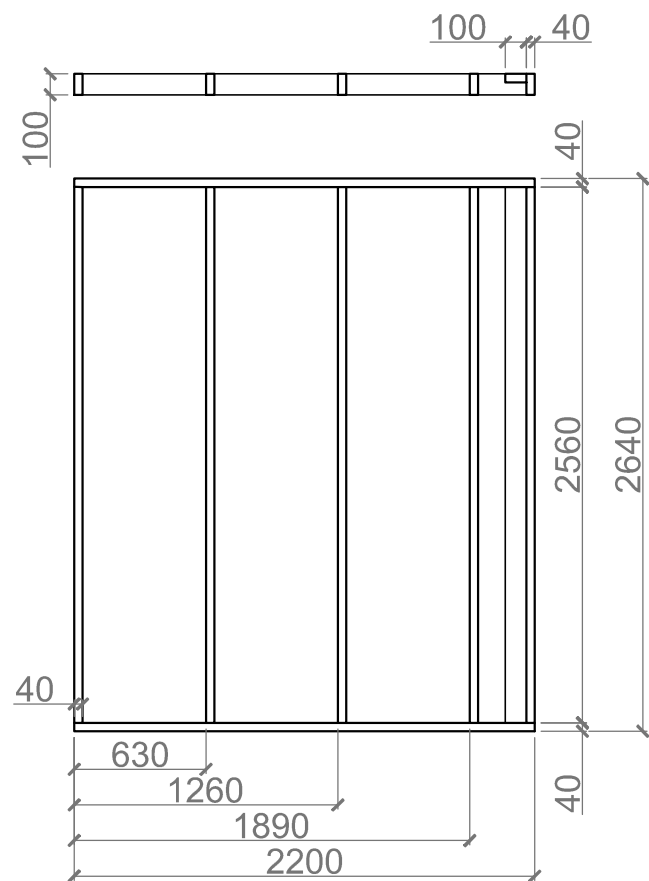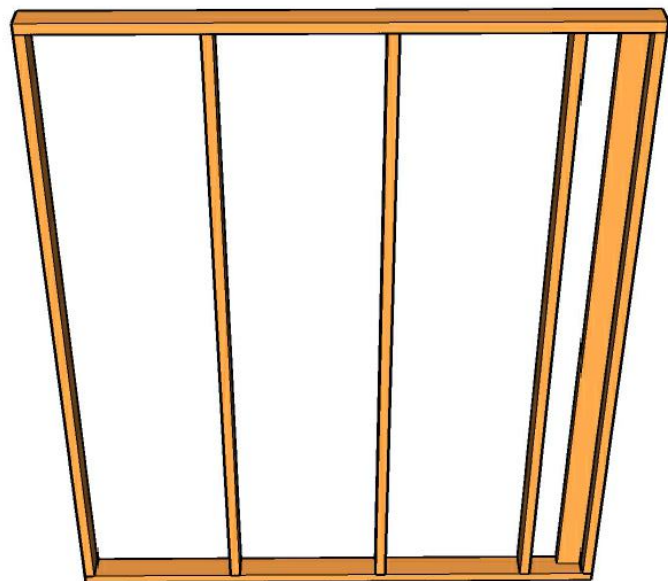



Расположение элементов каркаса.

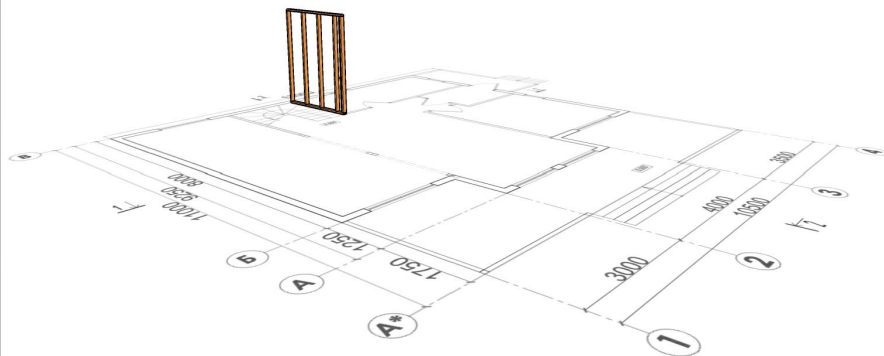


Экспликация:

Маркировка	Длина	Ширина	Толщина	Кол-во
Д 2200	2200	100	40	2
Д 2560	2560	100	40	6

Перегородка 3 (1-й этаж).

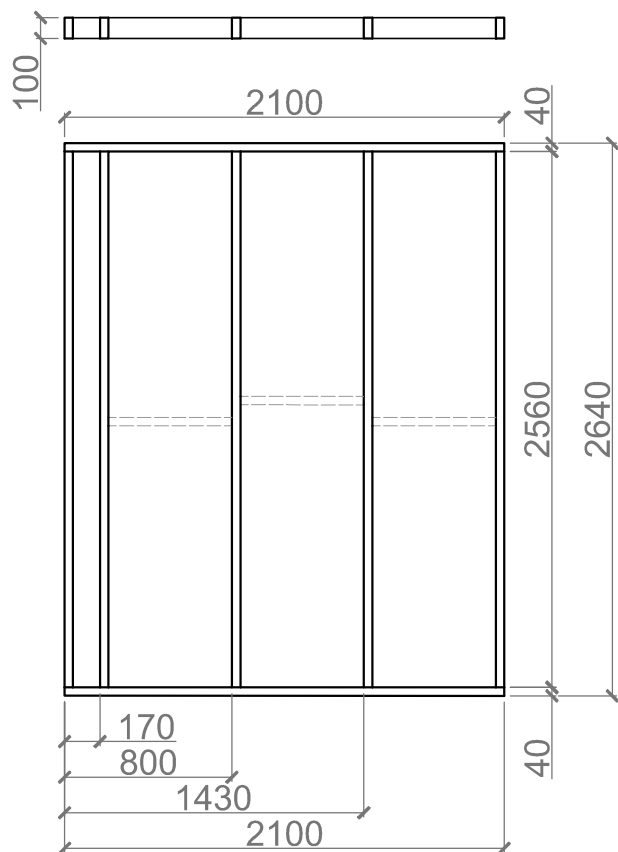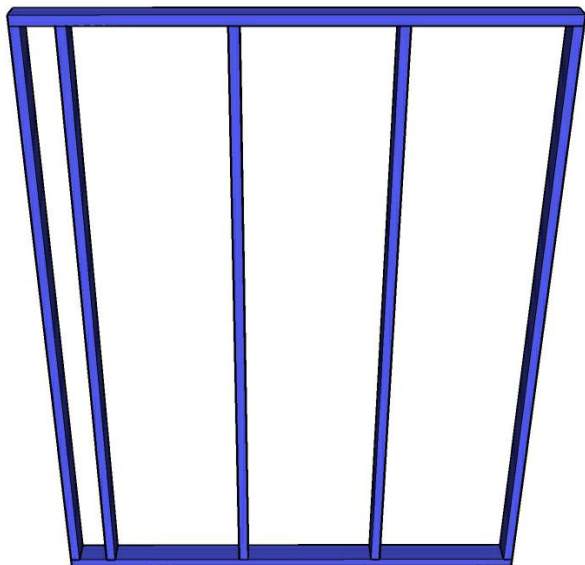


Расположение элементов каркаса.

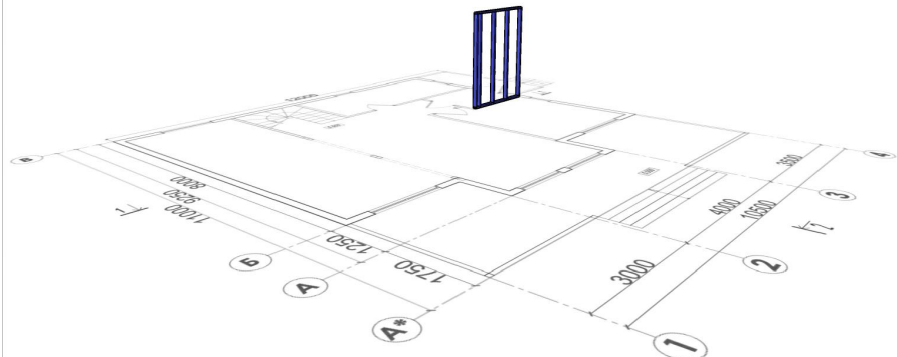


Экспликация:

Маркировка	Длина	Ширина	Толщина	Кол-во
Д 2100	2100	100	40	2
Д 2560	2560	100	40	5

Перегородка 2 (1-й этаж).

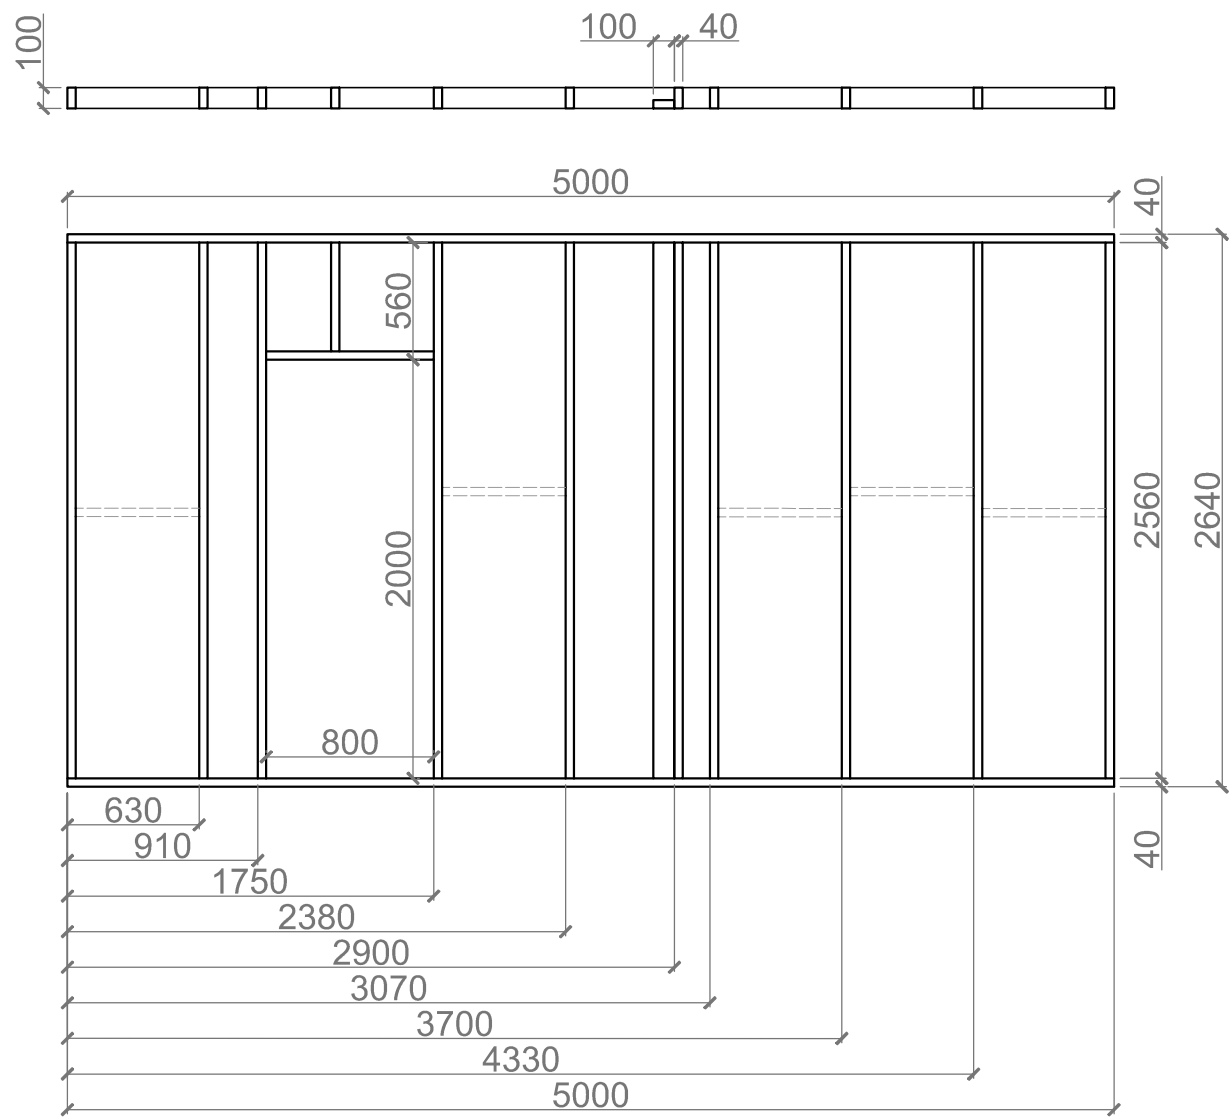

Расположение элементов каркаса.


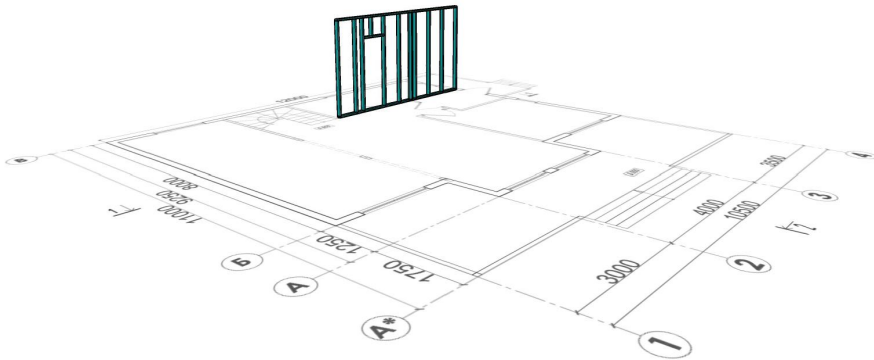


Экспликация:


Маркировка	Длина	Ширина	Толщина	Кол-во
Д 5000	5000	100	40	2
Д 2560	2560	100	40	11
Д 800	800	100	40	1
Д 520	520	100	40	1

Изм.	Кол. уч.	Лист	№ док.	Подп.	Дата	Перегородка 2 (1-й этаж).	Лист
							20

Перегородка 4 (1-й этаж).

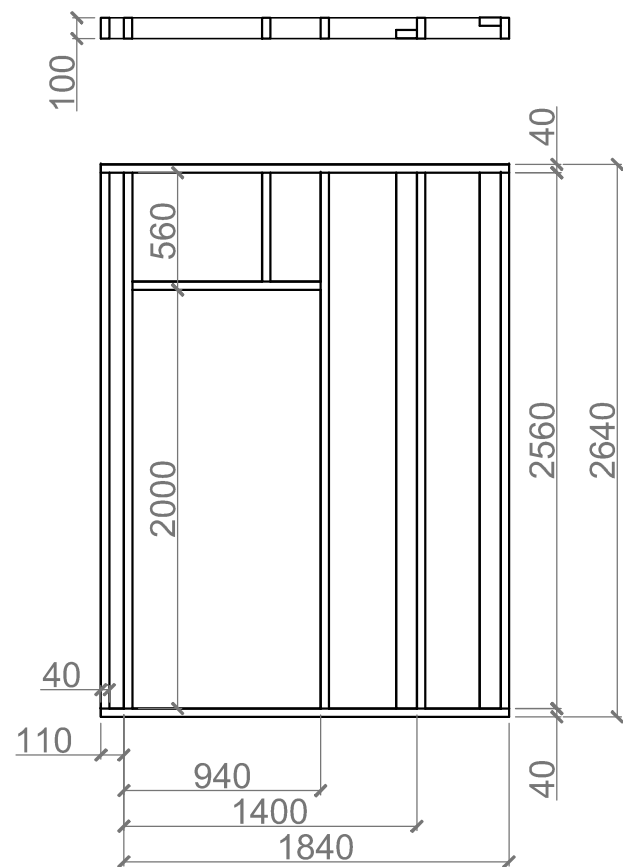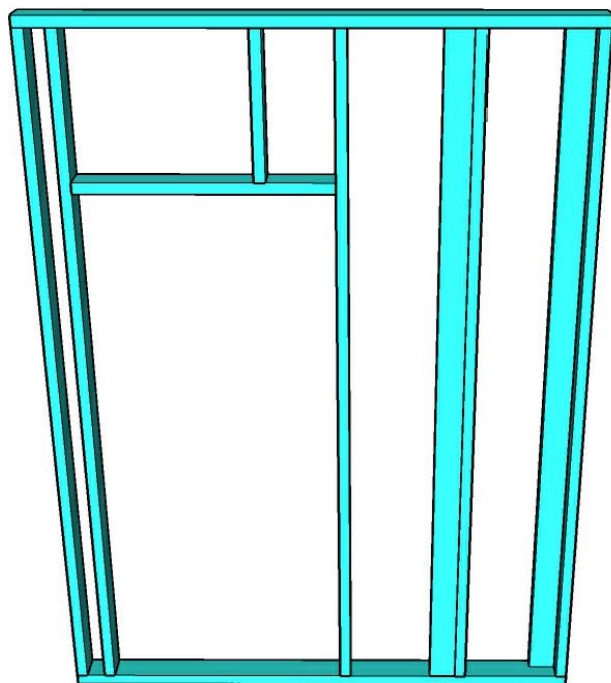



Расположение элементов каркаса.

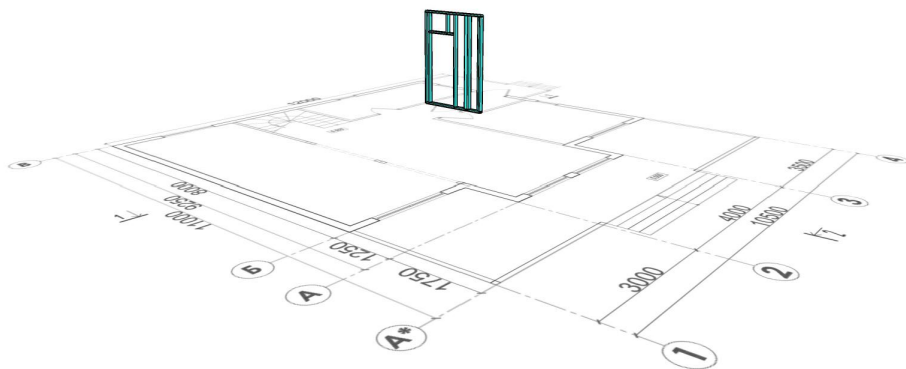


Экспликация:

Маркировка	Длина	Ширина	Толщина	Кол-во
Д 1840	1840	100	40	2
Д 2560	2560	100	40	7
Д 900	900	100	40	1
Д 520	520	100	40	1

Перегородка 5 (1-й этаж).

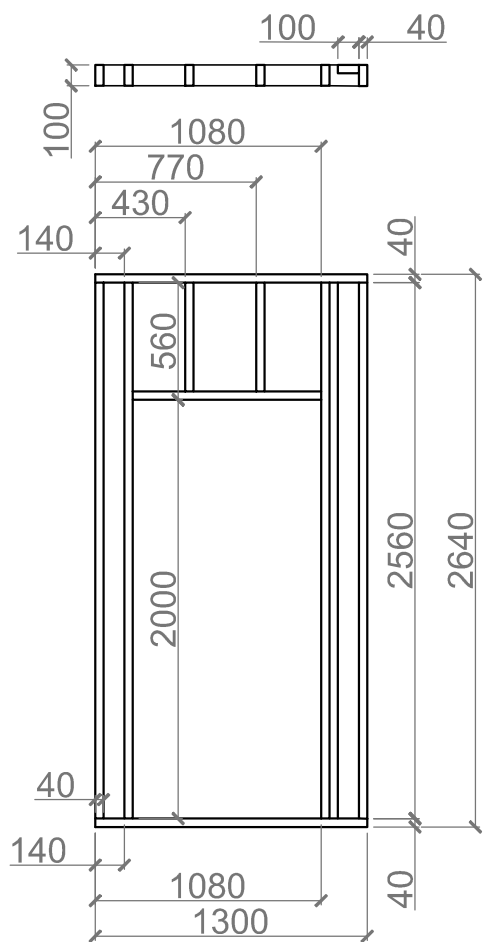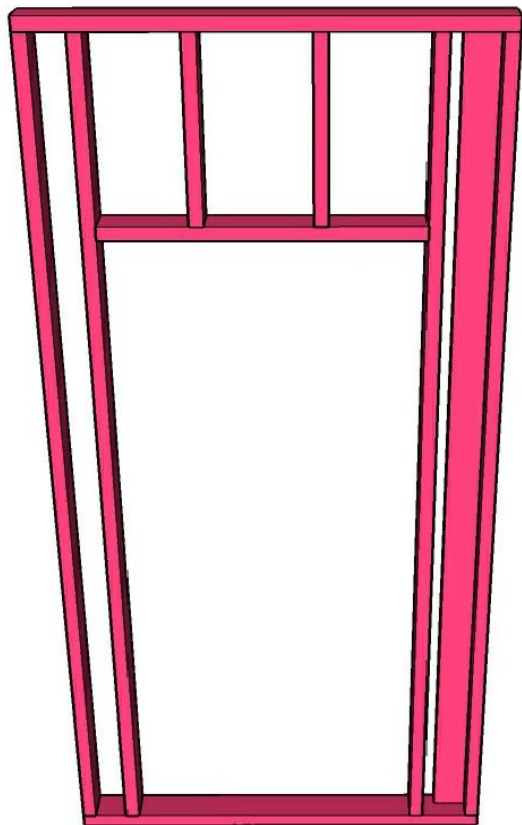


Расположение элементов каркаса.

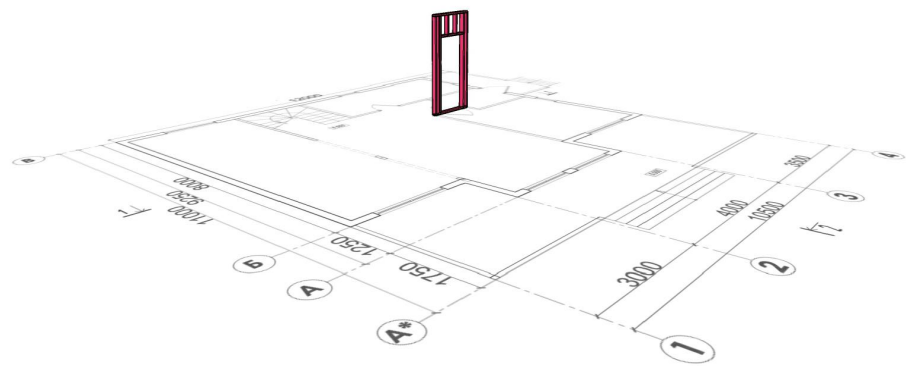


Экспликация:

Маркировка	Длина	Ширина	Толщина	Кол-во
Д 3890	3890	100	40	2
Д 2560	2560	100	40	5
Д 900	900	100	40	1
Д 520	520	100	40	2

Схема обвязки стен 1-го этажа.

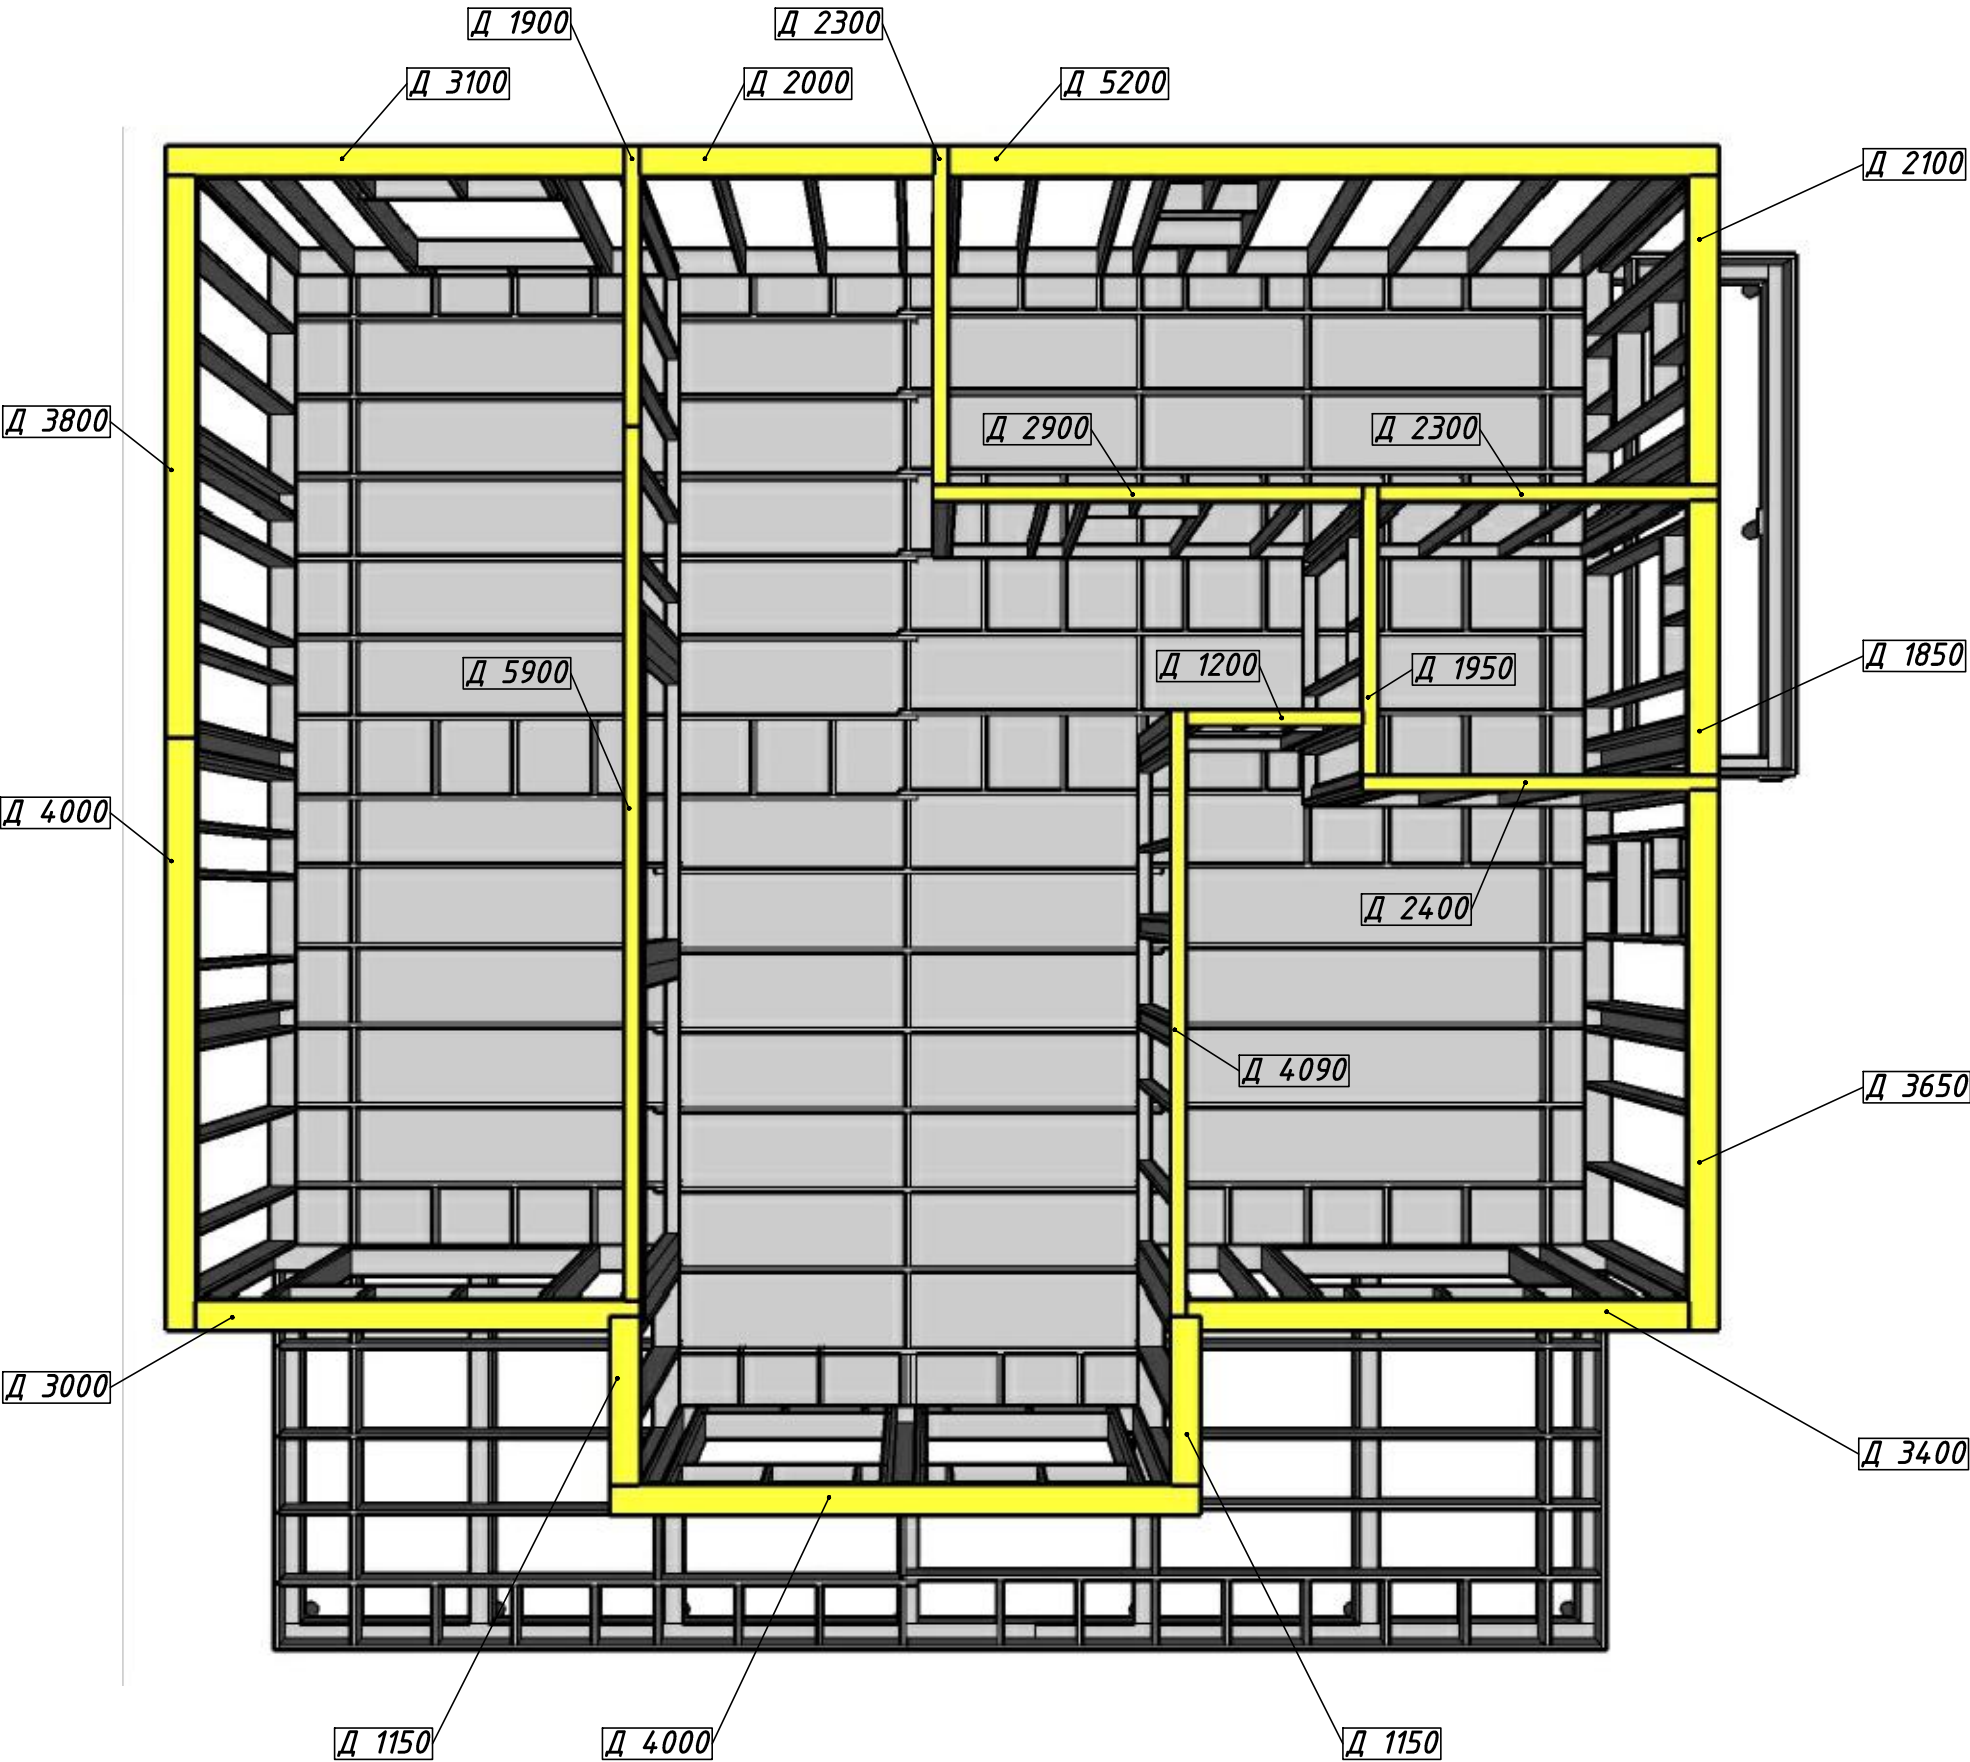


Расположение элементов каркаса.

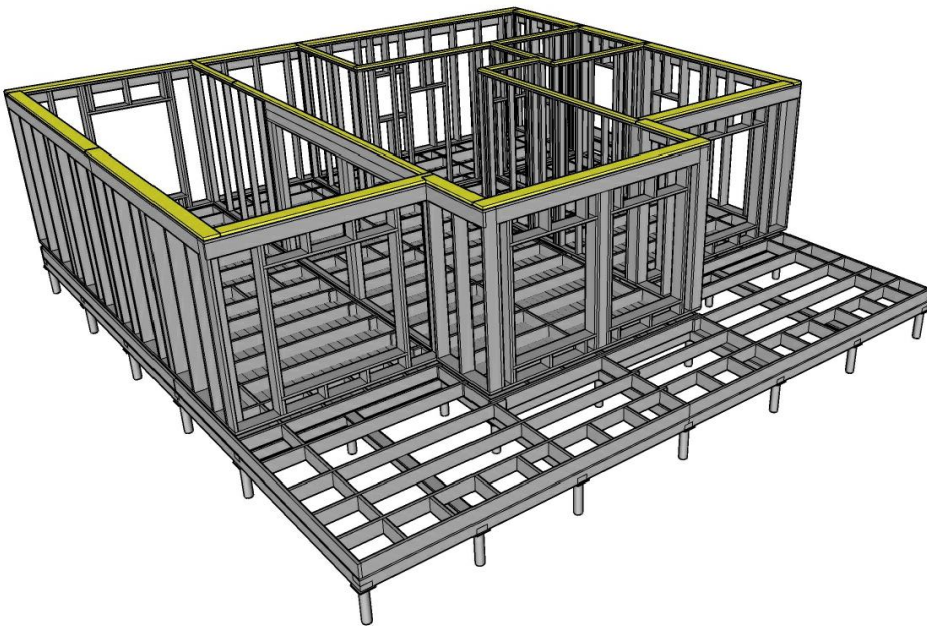

Экспликация:



Маркировка	Длина	Ширина	Толщина	Кол-во
Д 5200	5200	200	40	1
Д 4000	4000	200	40	2
Д 3800	3800	200	40	1
Д 3650	3650	200	40	1
Д 3400	3400	200	40	1
Д 3100	3100	200	40	1
Д 3000	3000	200	40	1
Д 2100	2100	200	40	1
Д 2000	2000	200	40	1
Д 1850	1850	200	40	1
Д 1150	1150	200	40	2
Д 5900	5900	100	40	1
Д 4090	4090	100	40	1
Д 2900	2900	100	40	1
Д 2400	2400	100	40	1
Д 2300	2300	100	40	2
Д 1950	1950	100	40	1
Д 1900	1900	100	40	1
Д 1200	1200	100	40	1

Платформа 2-го мансардного этажа. Общий вид.

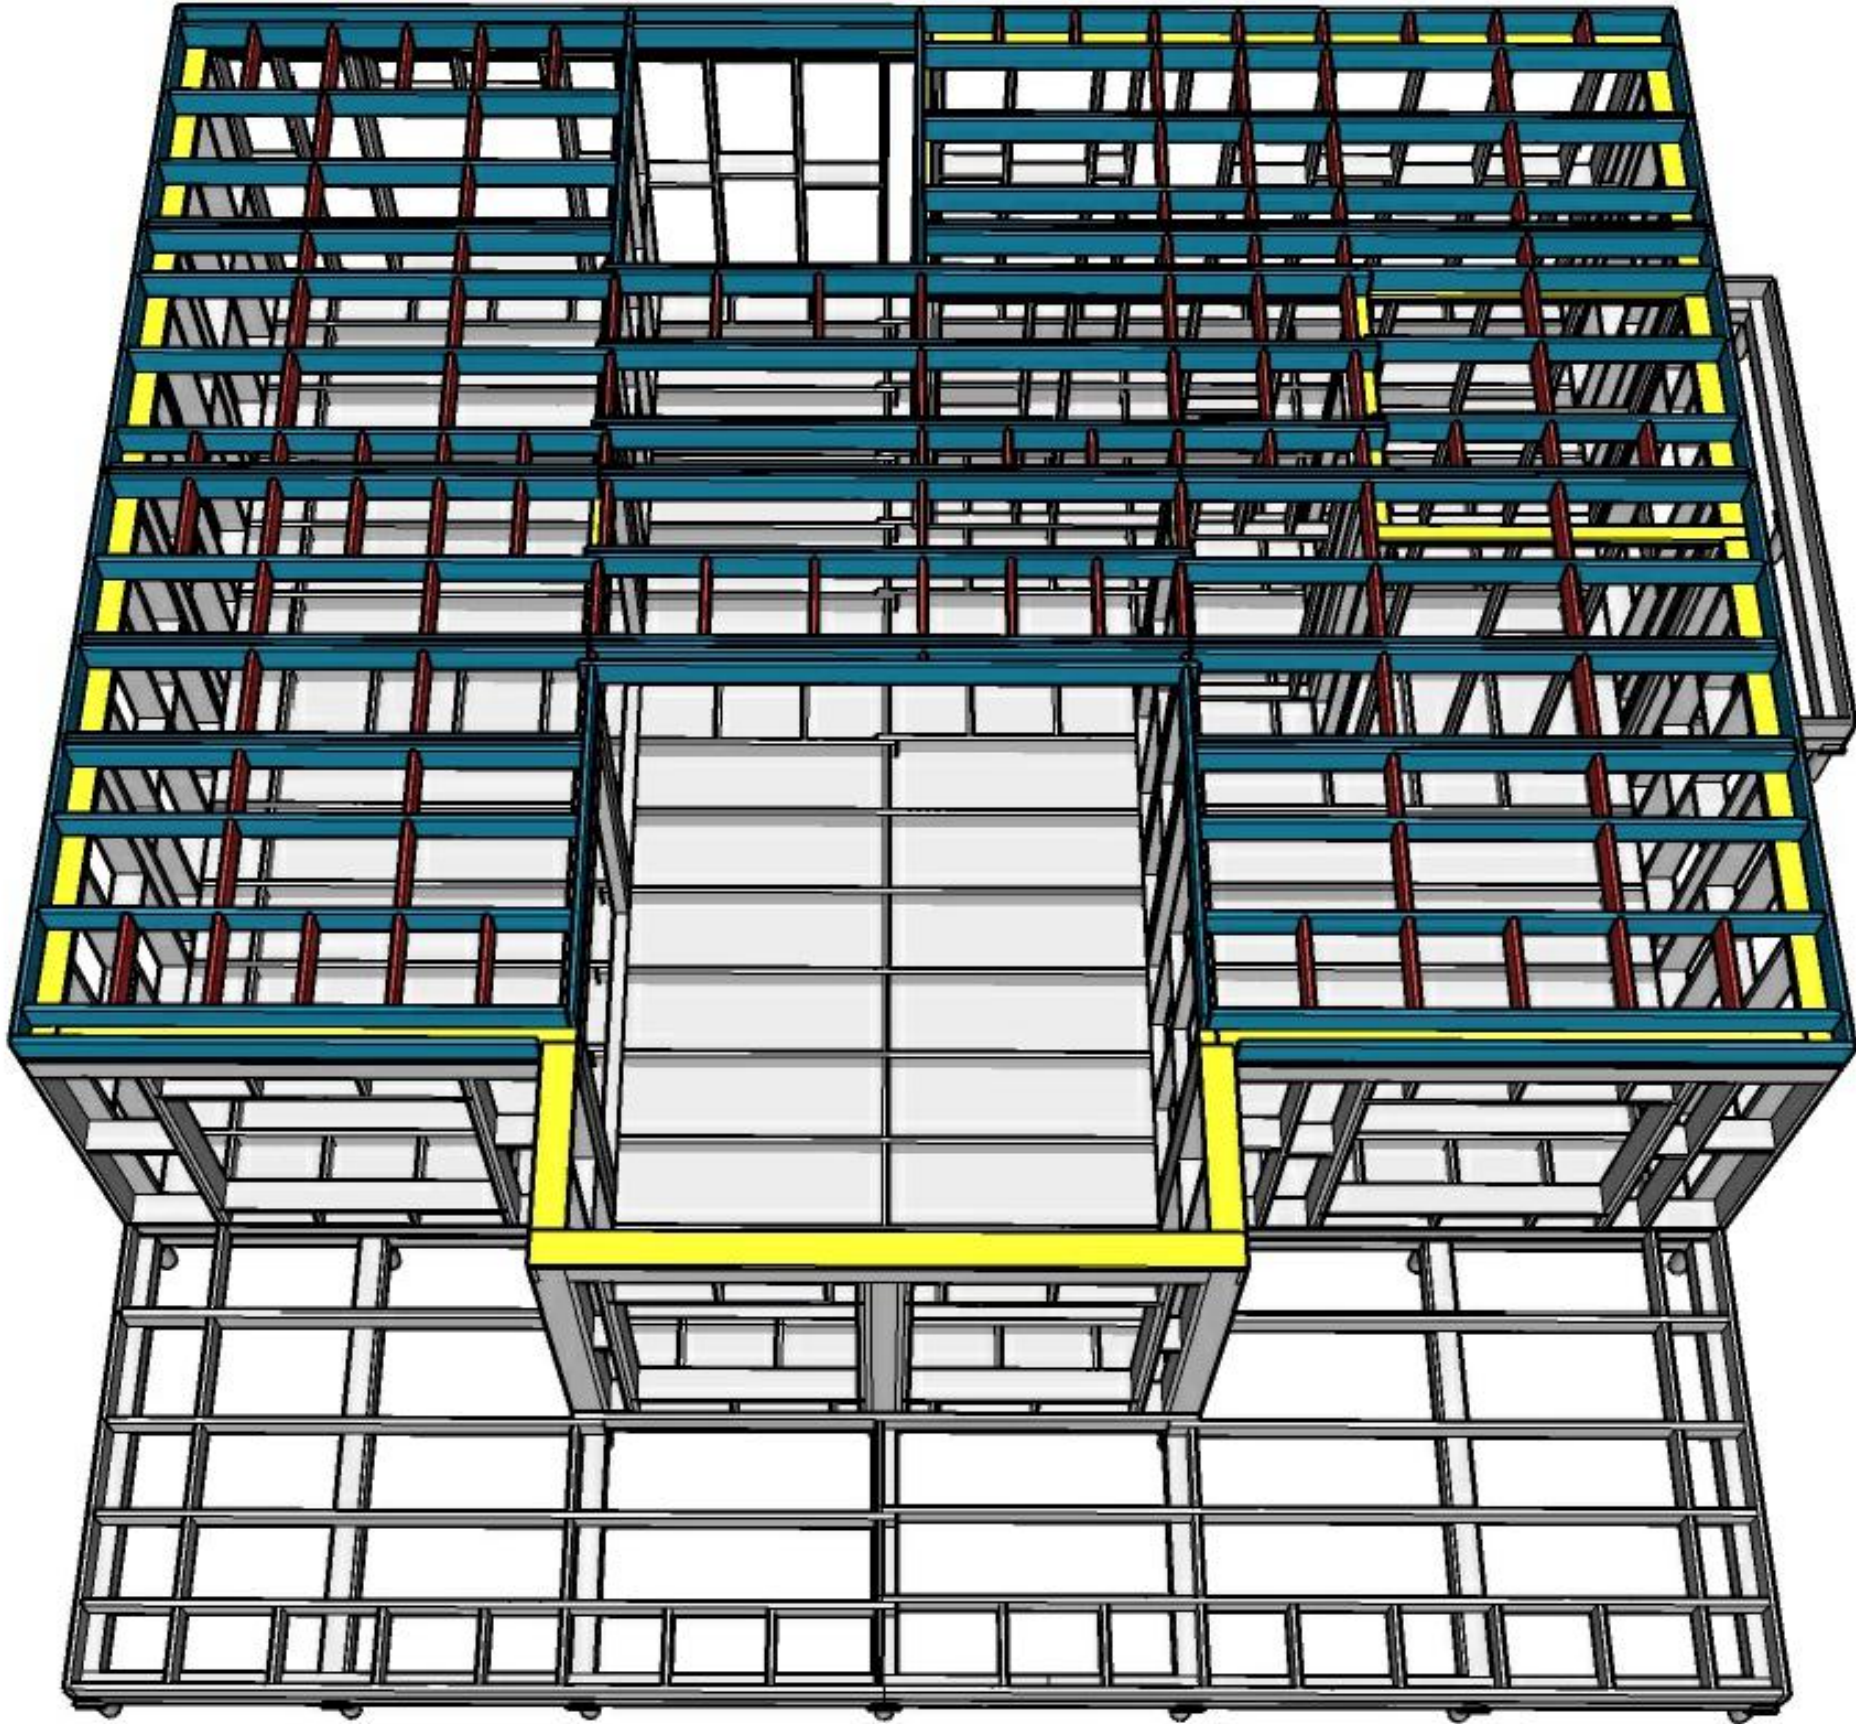

Кол. уч.	Лист	№ док.	Подп.	Дата	Платформа 2-го мансардного этажа. Общий вид.	Лист
						23

Расположение элементов каркаса.

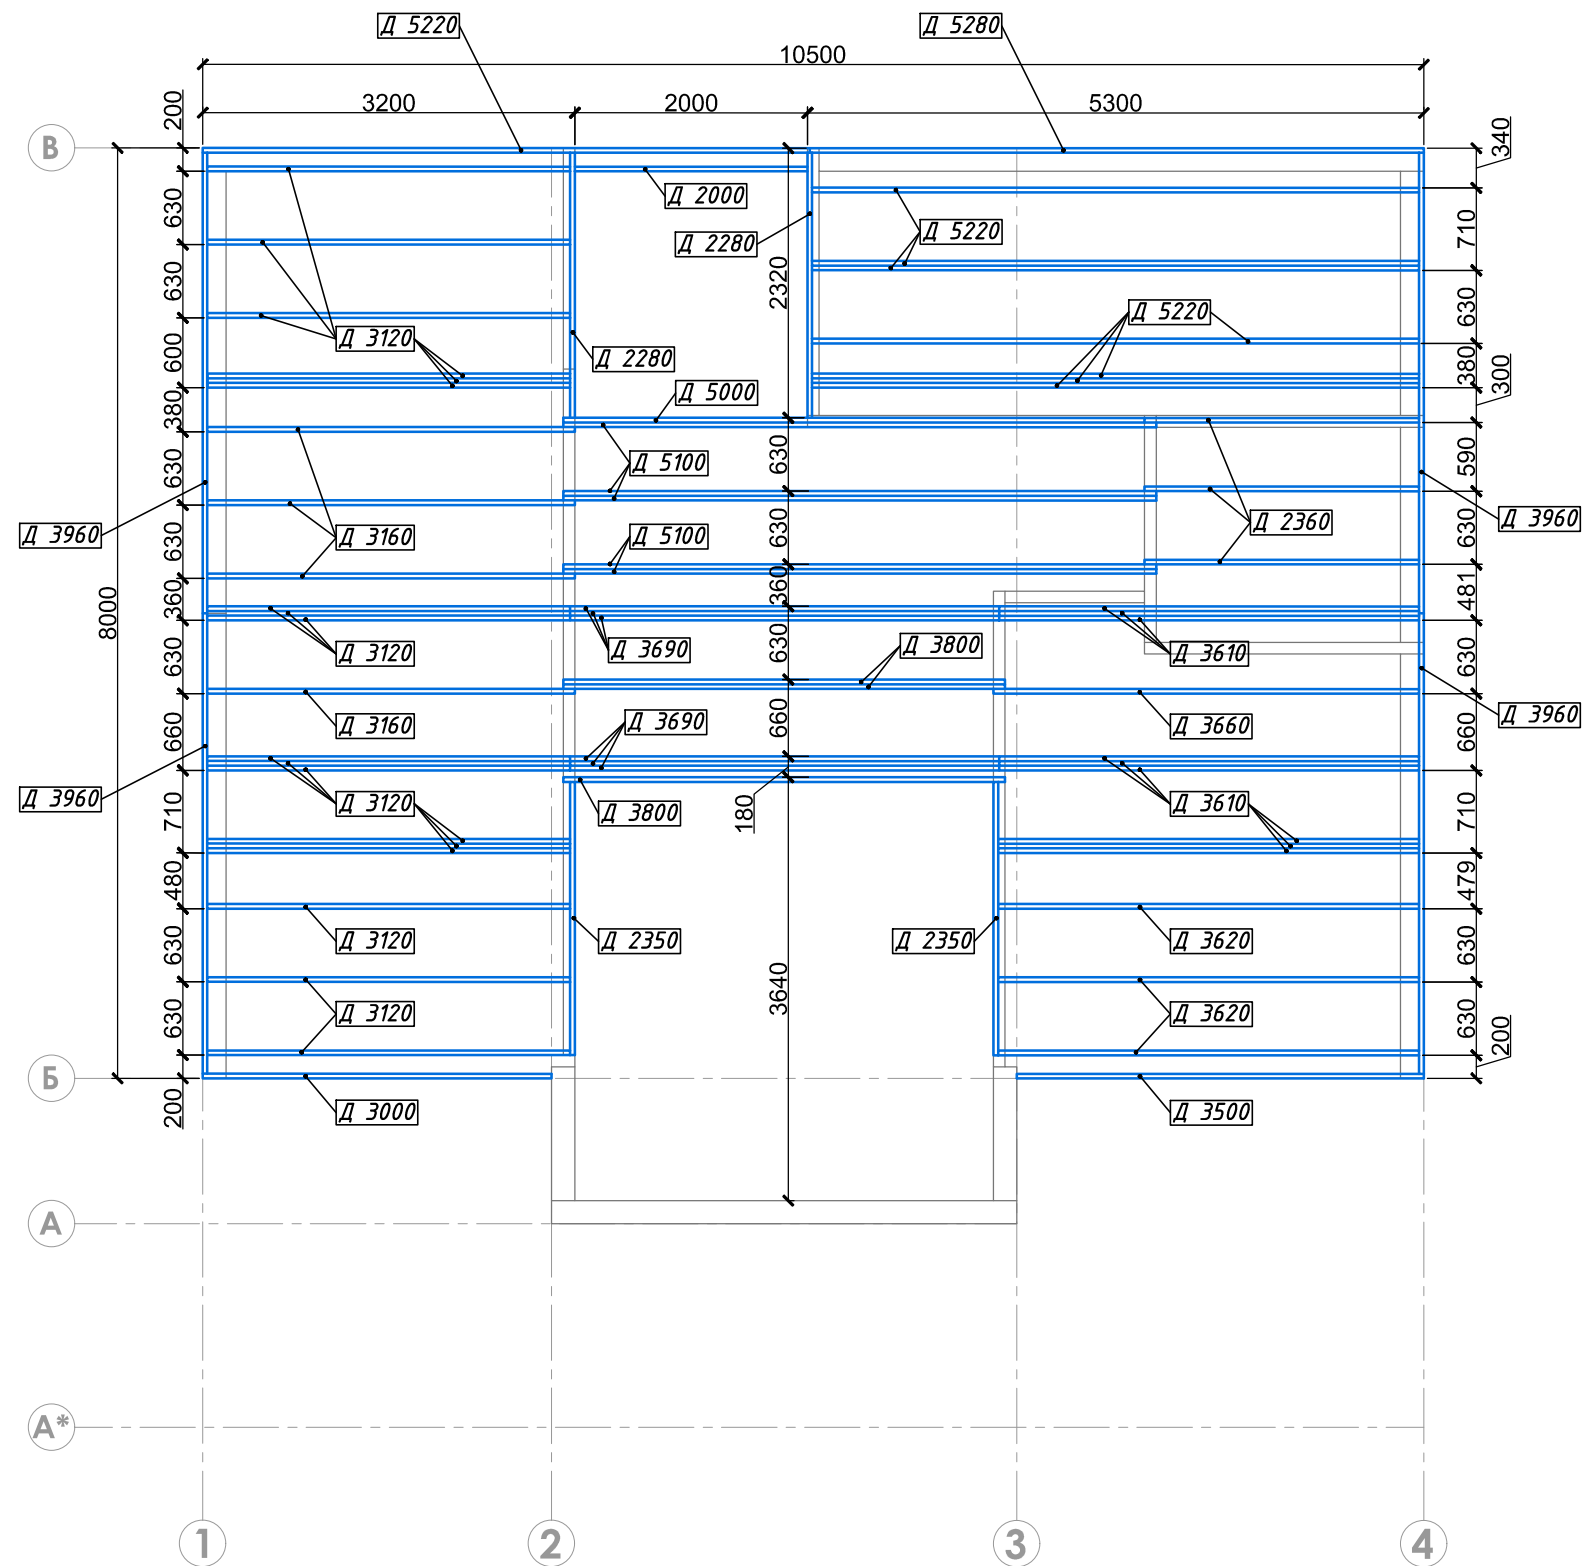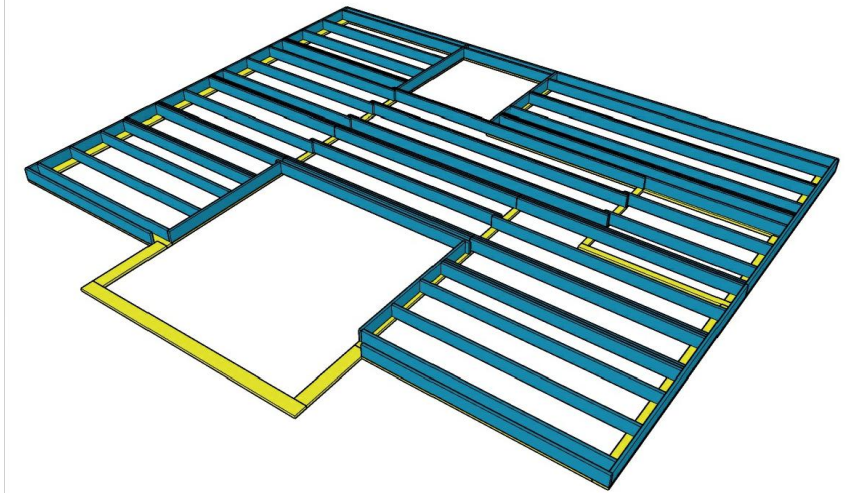

Экспликация:



Маркировка	Длина	Ширина	Толщина	Кол-во
Д 2000	2000	200	40	1
Д 2280	2280	200	40	2
Д 2350	2350	200	40	2
Д 2360	2360	200	40	3
Д 3000	3000	200	40	1
Д 3120	3120	200	40	18
Д 3160	3160	200	40	4
Д 3500	3500	200	40	1
Д 3610	3610	200	40	9
Д 3620	3620	200	40	3
Д 3660	3660	200	40	1
Д 3690	3690	200	40	6
Д 3800	3800	200	40	3
Д 3960	3960	200	40	4
Д 5000	5000	200	40	1
Д 5100	5100	200	40	5
Д 5220	5220	200	40	8
Д 5280	5280	200	40	1

1. Для соединения досок в каркасе стен и перекрытий рекомендуется использовать не менее 1-го гвоздя на каждые 5 см ширины доски.

Изм.	Кол. уч.	Лист	№ док.	Подп.	Дата	Платформа 2-го мансардного этажа. Лаги пола.	Лист
							24

Платформа 2-го мансардного этажа. Бриджинги.

Расположение элементов каркаса.

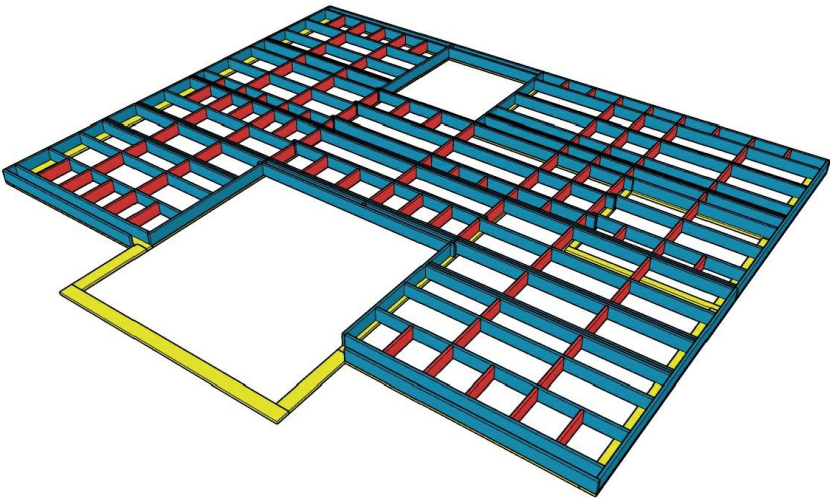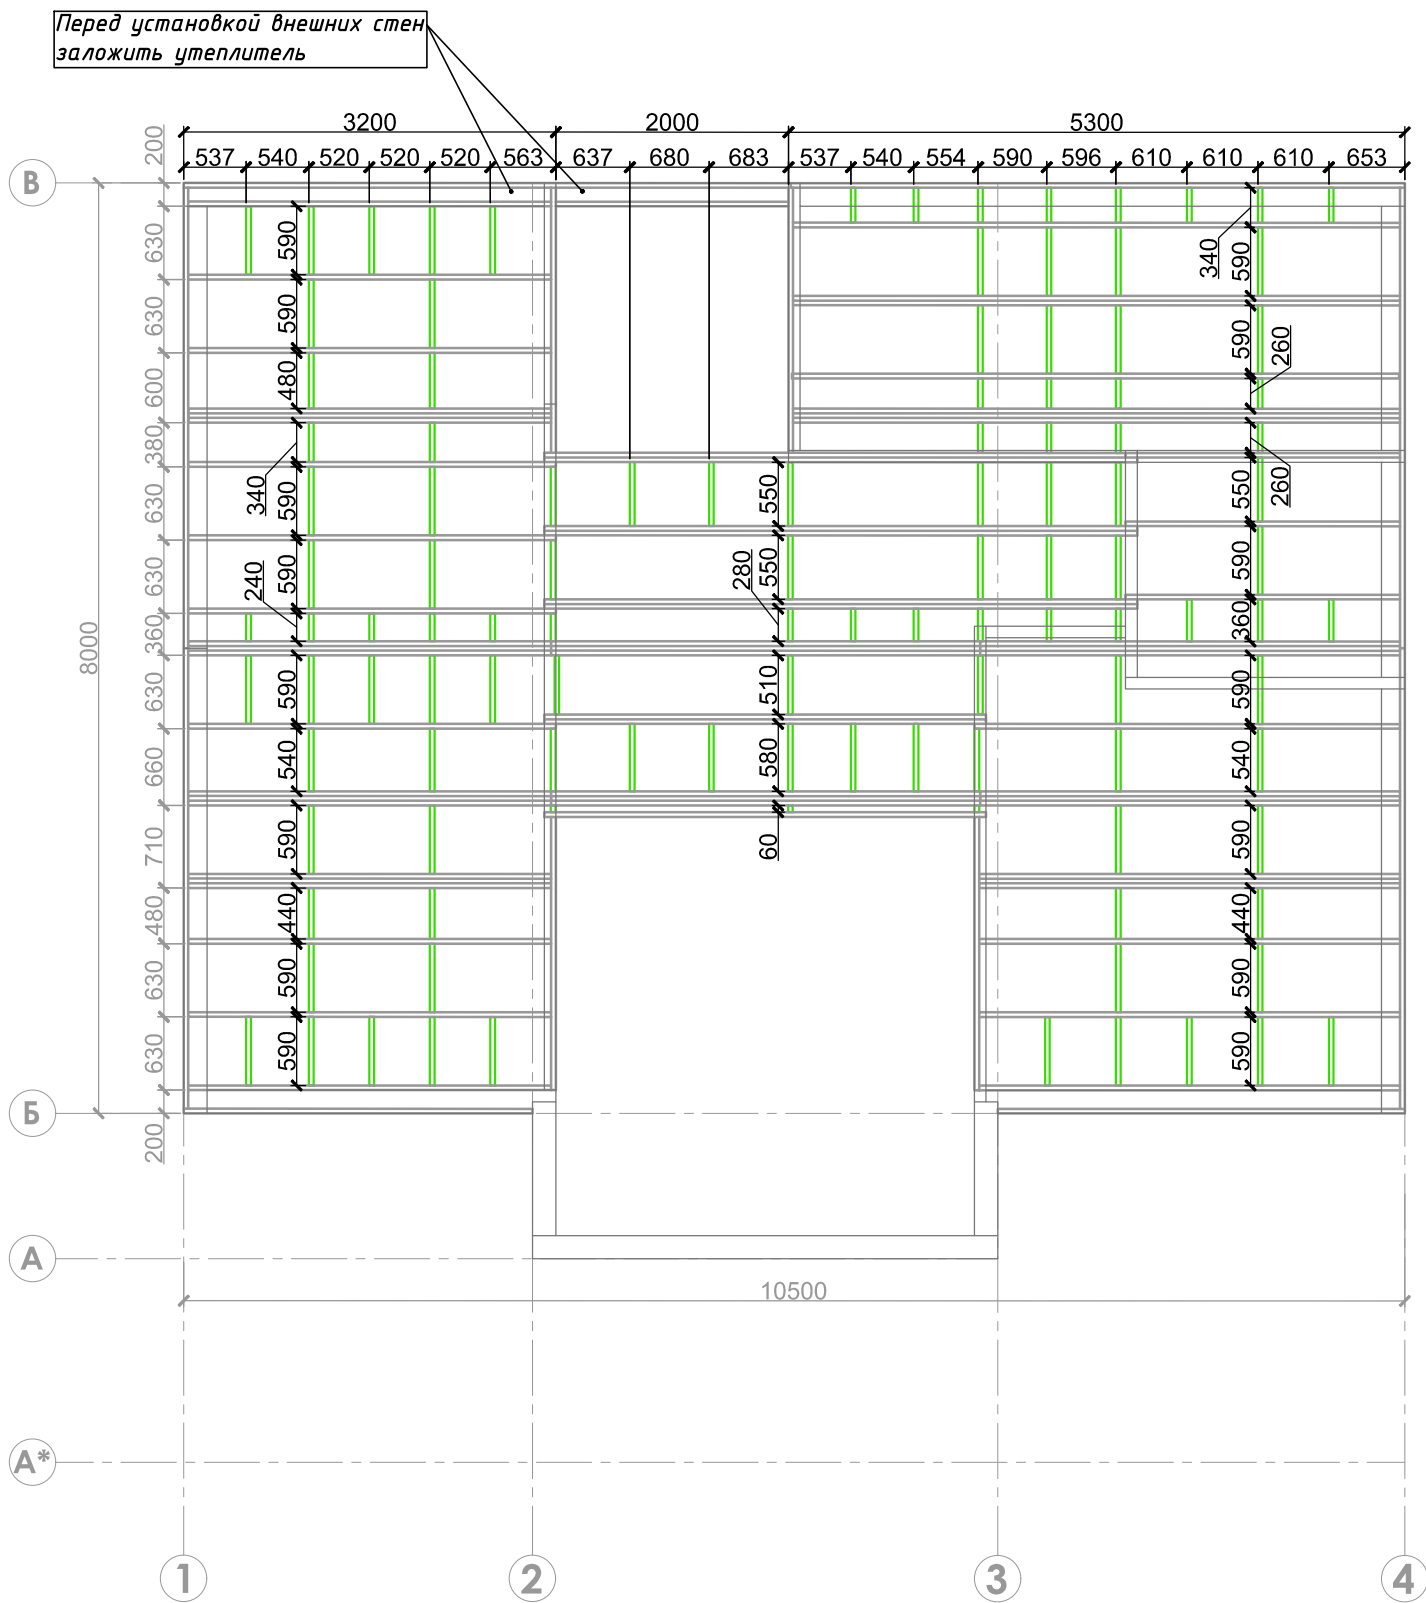


Экспликация:

Маркировка	Длина	Ширина	Толщина	Кол-во
Д 590	590	200	40	45
Д 580	580	200	40	5
Д 550	550	200	40	11
Д 540	540	200	40	6
Д 510	510	200	40	5
Д 480	480	200	40	2
Д 440	440	200	40	4
Д 360	360	200	40	3
Д 340	340	200	40	2
Д 300	300	200	40	8
Д 280	280	200	40	6
Д 260	260	200	40	8
Д 240	240	200	40	6
Д 60	60	200	40	2

1. В местах высокой точечной нагрузки монтируется двойной\тройной бриджинг.

Изм.	Кол. уч.	Лист	№ док.	Подп.	Дата	Платформа 2-го мансардного этажа. Бриджинги.	Лист
							25

Стены 2-го мансардного этажа. Общий вид.


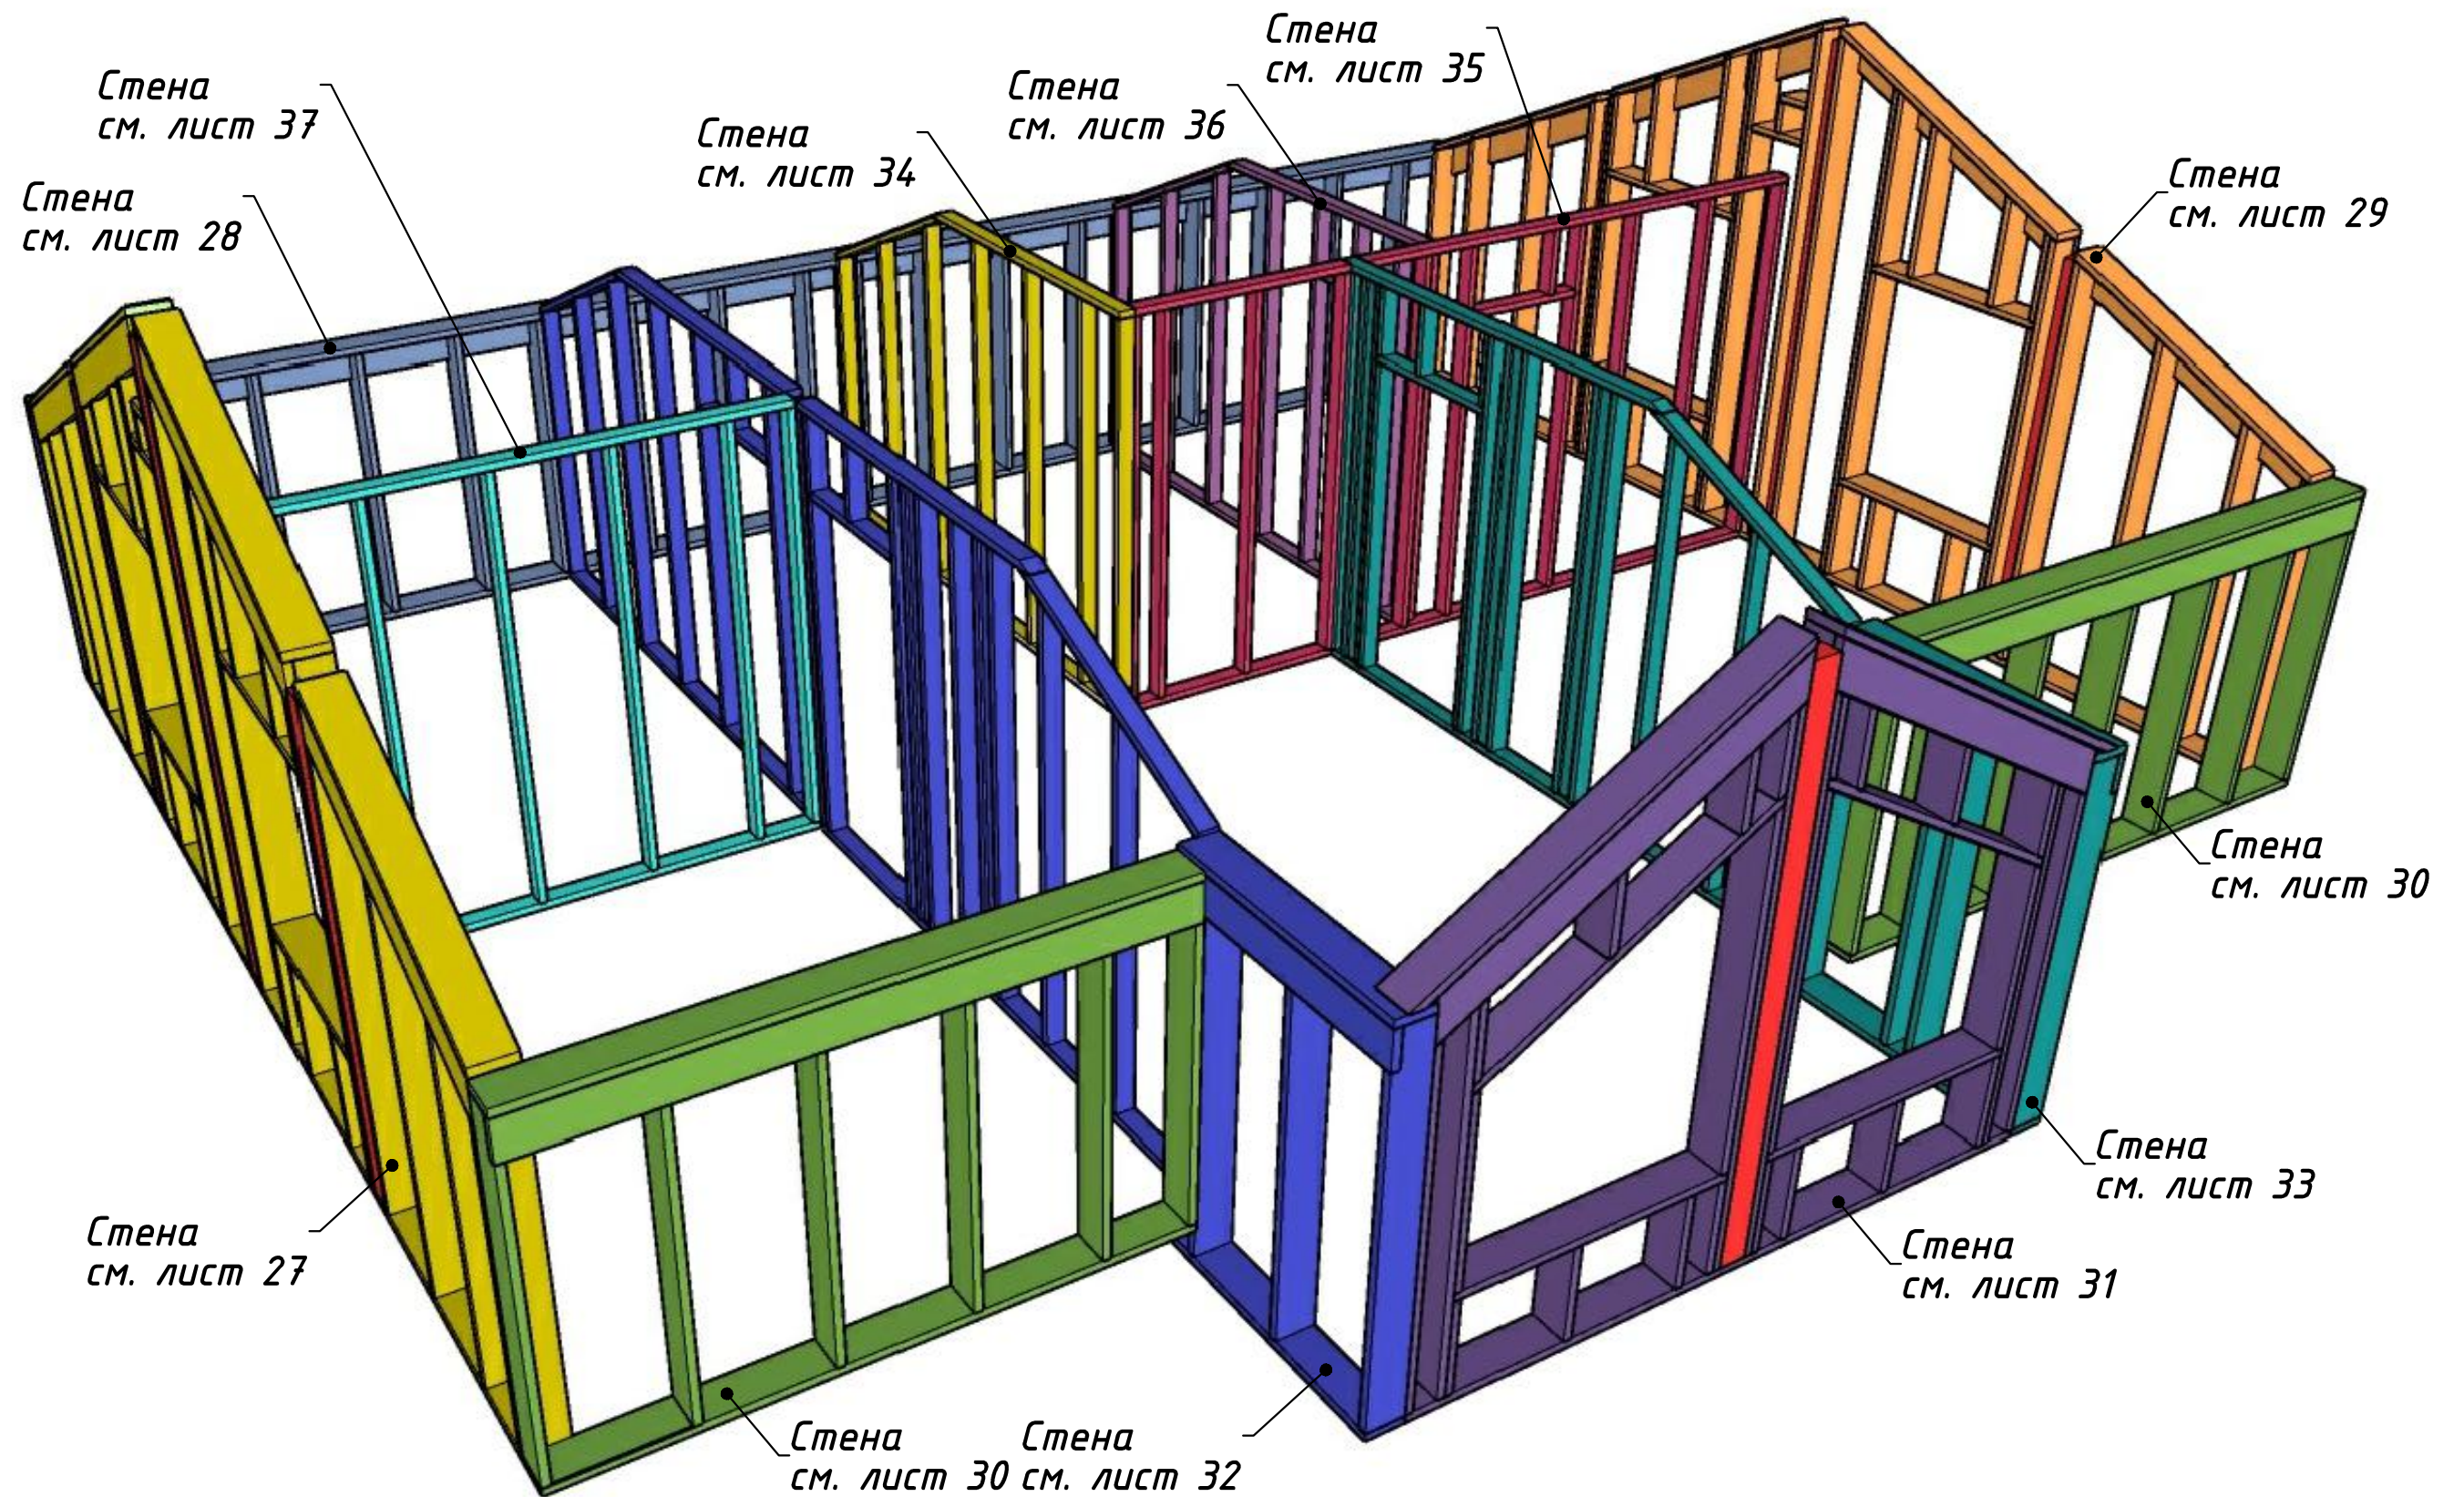


Изм.	Кол. уч.	Лист	№ док.	Подп.	Дата


Стены 1-го этажа. Общий вид.

Лист
26

Стена по оси 1 (2-й этаж).

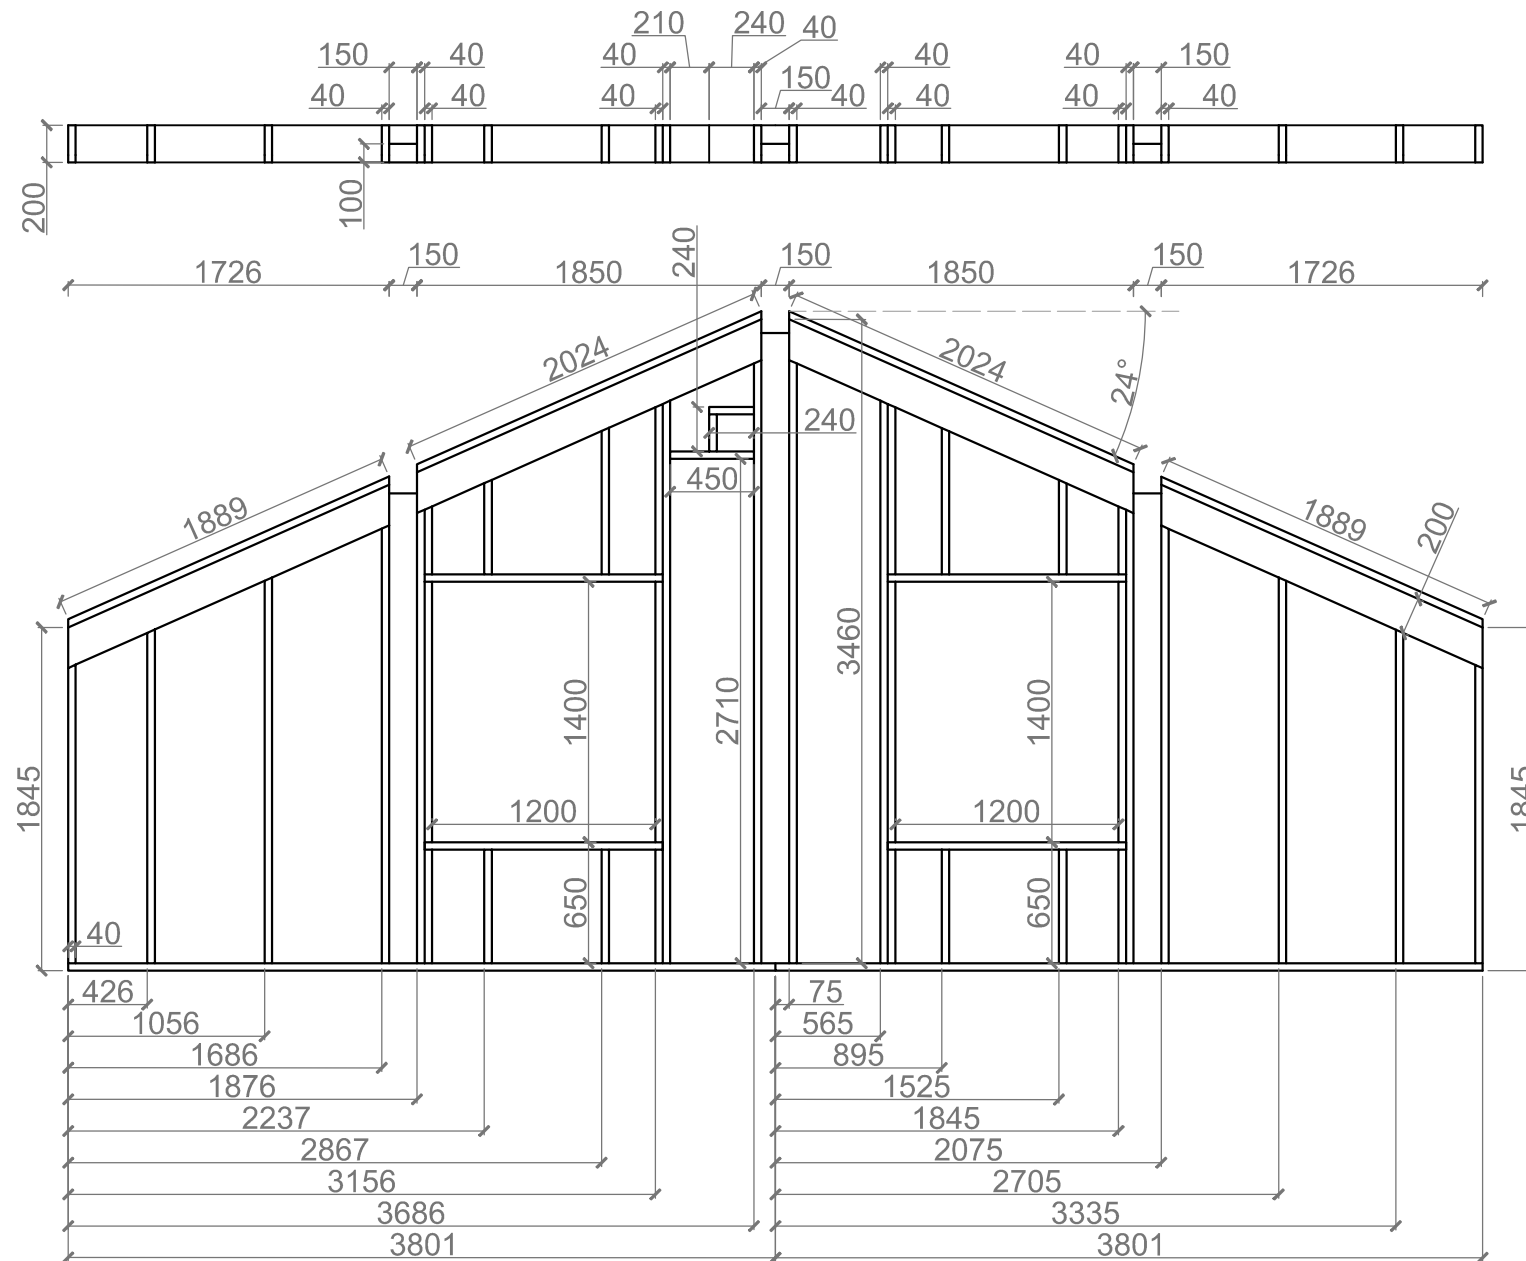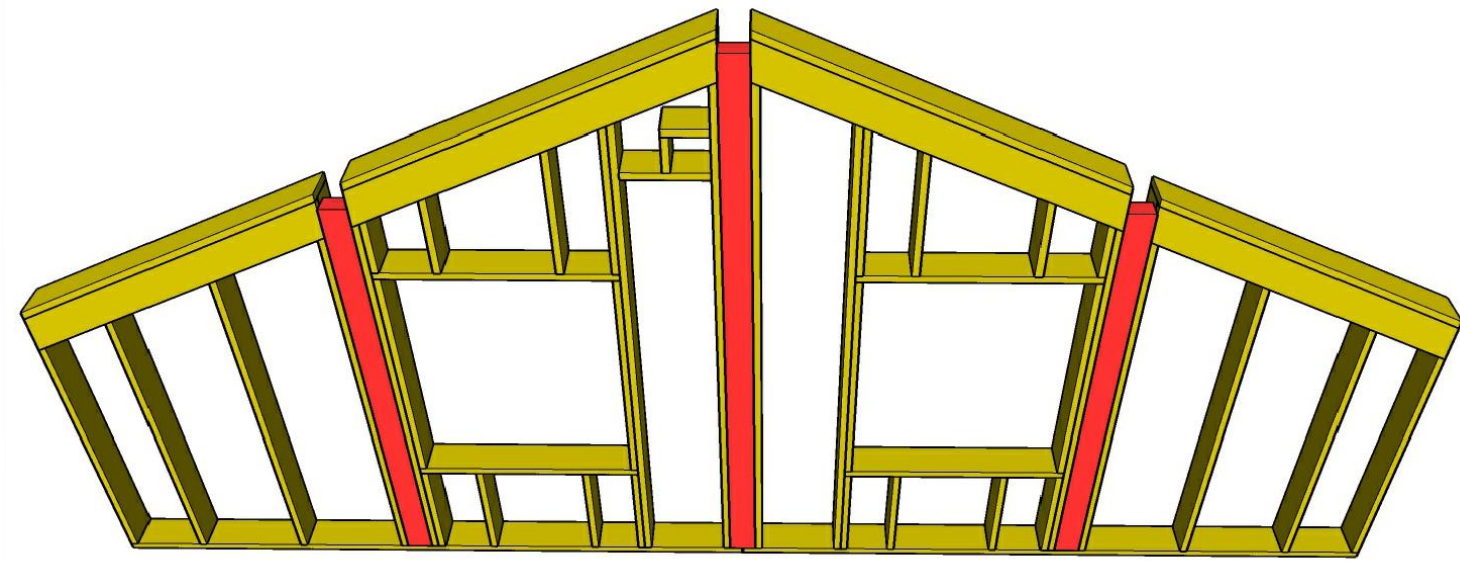

Расположение элементов каркаса.

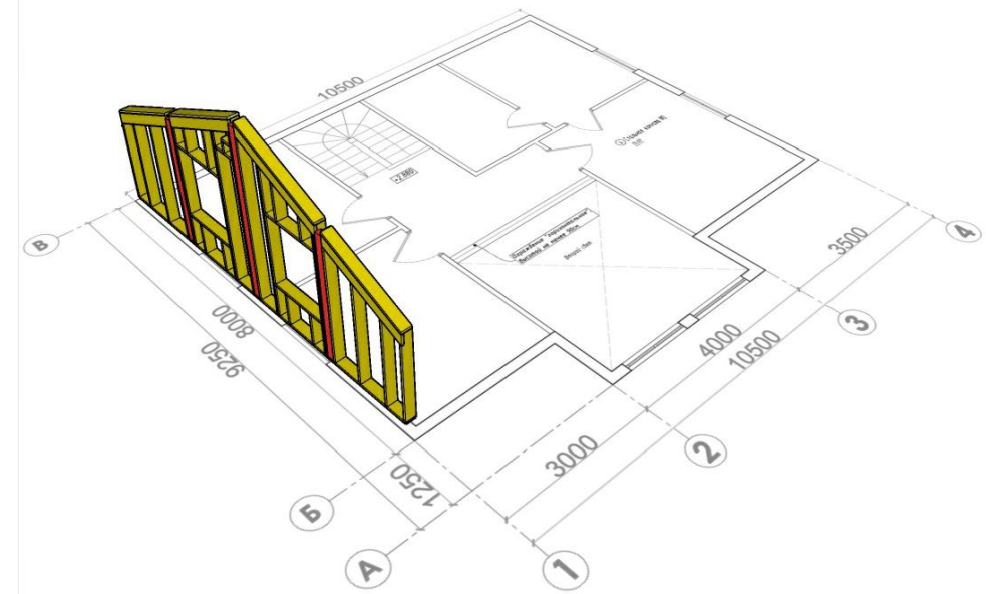

Экспликация:

Маркировка	Длина	Ширина	Толщина	Кол-во
Д 3800	3800	200	40	2
Д 3460	3460	200	40	2
Д 3240	3240	200	40	2
Д 2655	2655	200	40	2
Д 2570	2570	200	40	2
Д 2290	2290	200	40	2
Д 2040	2040	200	40	2
Д 2010	2010	200	40	2
Д 1900	1900	200	40	2
Д 1820	1820	200	40	2
Д 1400	1400	200	40	4
Д 1280	1280	200	40	4
Д 1135	1135	200	40	2
Д 1005	1005	200	40	2
Д 725	725	200	40	2
Д 610	610	200	40	8
Д 580	580	200	40	2
Д 450	450	200	40	1
Д 240	240	200	40	1
Д 200	200	200	40	1
Б 3387	3387	150	100	1


Изм.	Кол. уч.	Лист	№ док.	Подп.	Дата

Стена по оси 1 (2-й этаж).

Лист

27



Стена по оси В (2-й этаж).

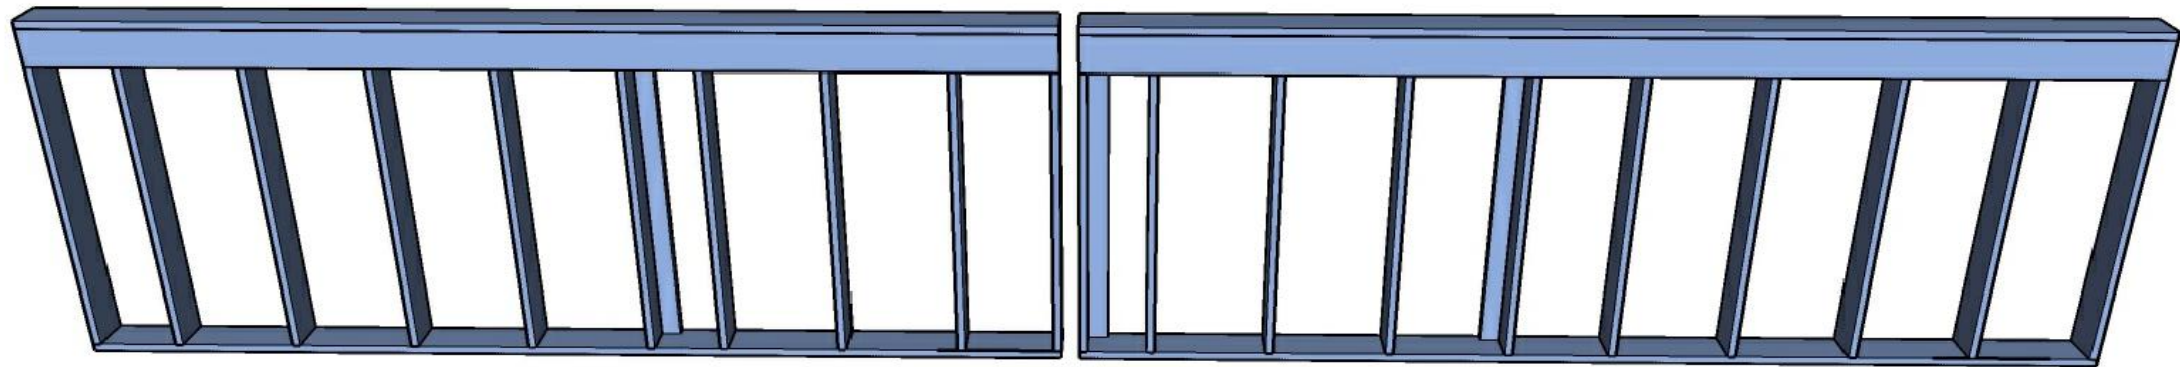


Экспликация:

Маркировка	Длина	Ширина	Толщина	Кол-во
Д 5340	5340	200	40	3
Д 5160	5160	200	40	3
Д 1760	1760	200	40	20
Д 1760	1760	100	40	3


Расположение элементов каркаса.

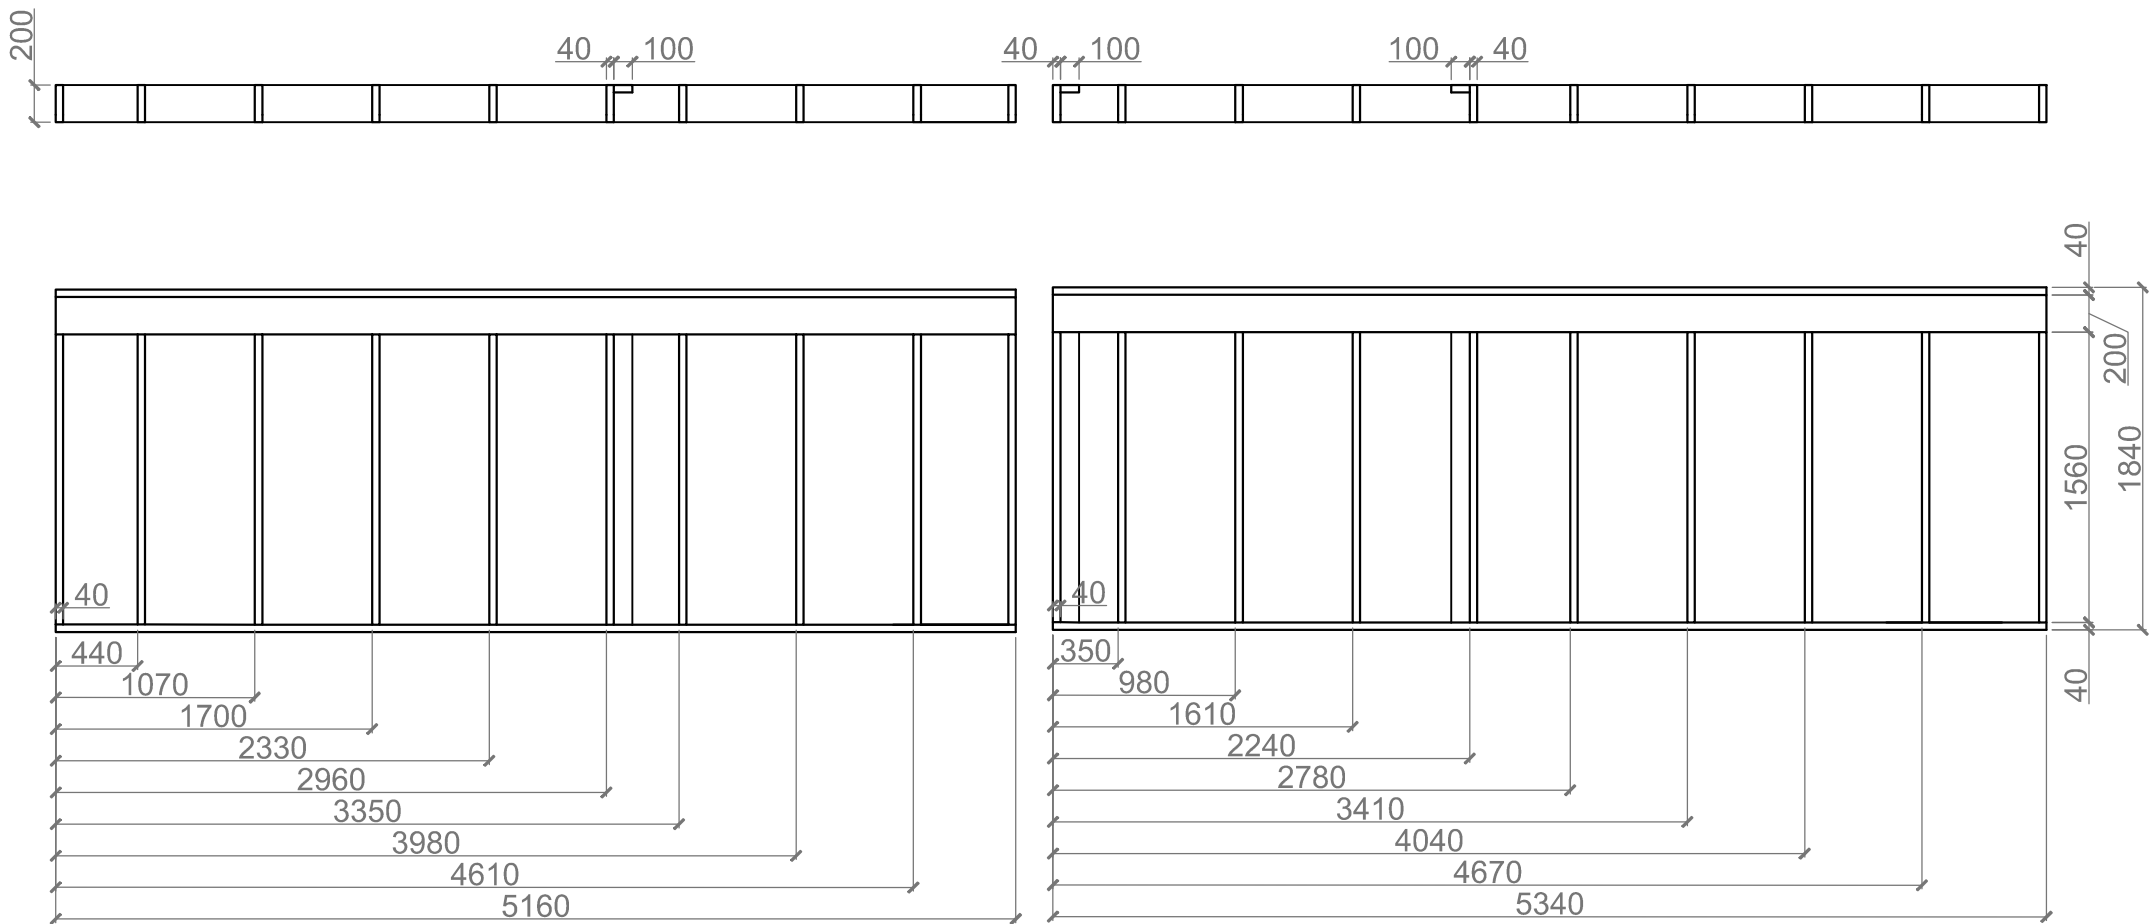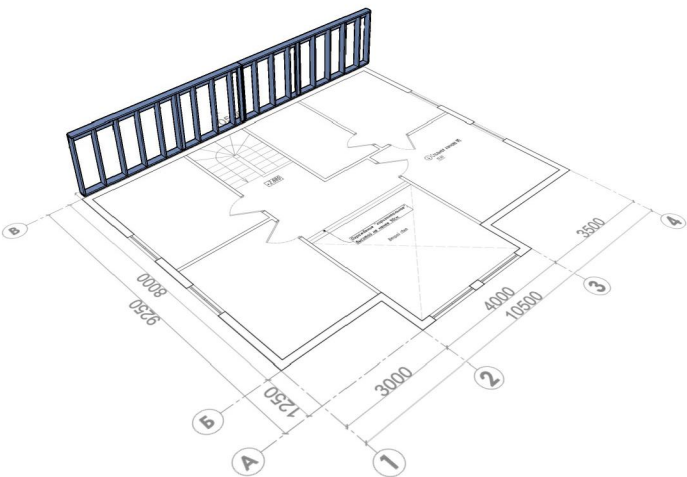

Стена по оси 4 (2-й этаж).

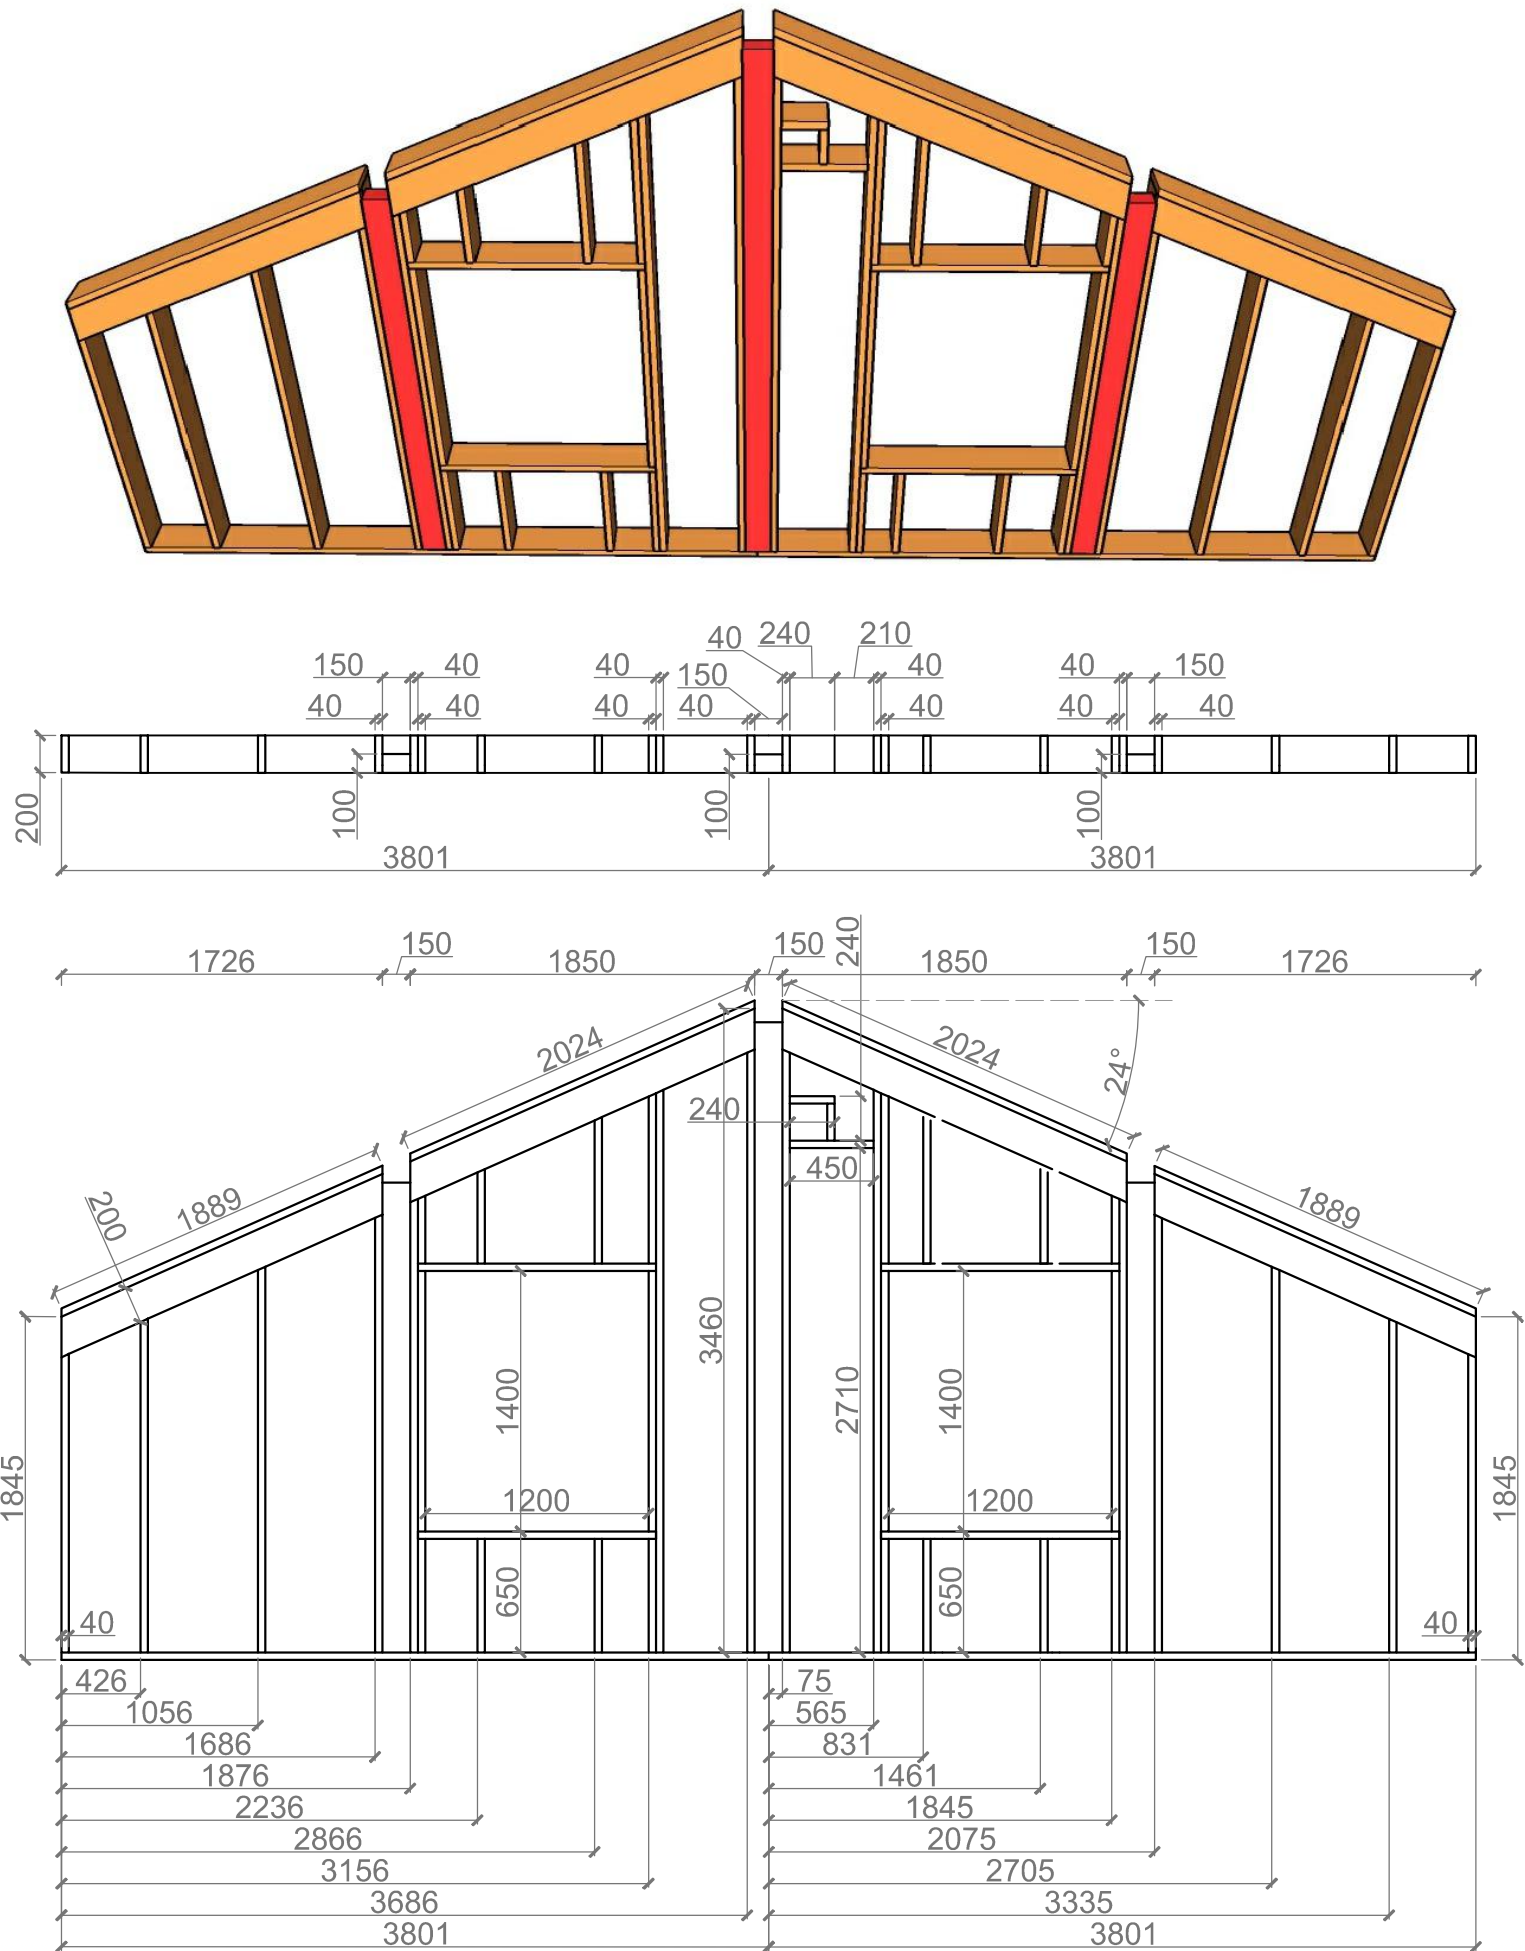


Расположение элементов каркаса.

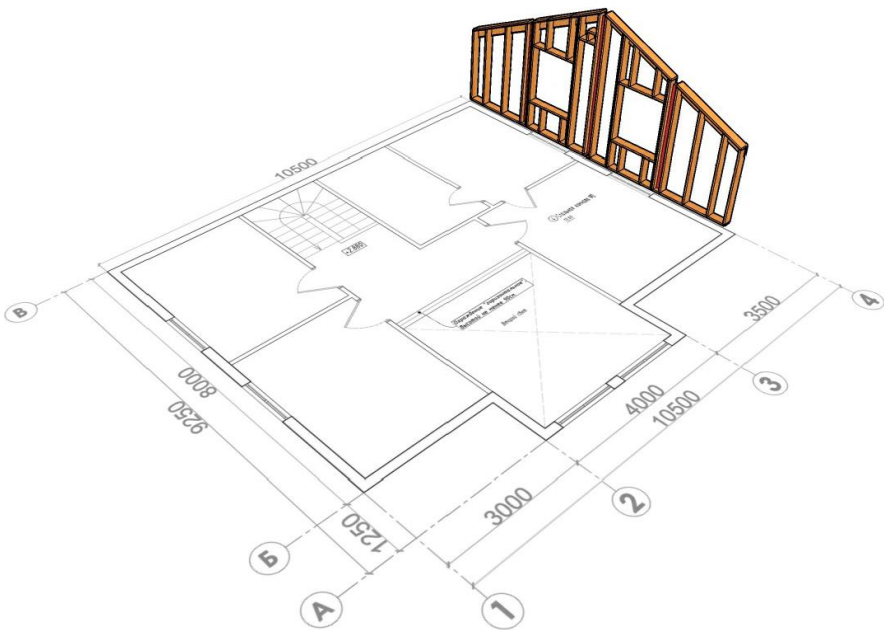



Экспликация:

Маркировка	Длина	Ширина	Толщина	Кол-во
Д 3800	3800	200	40	2
Д 3460	3460	200	40	2
Д 3240	3240	200	40	2
Д 2655	2655	200	40	2
Д 2570	2570	200	40	2
Д 2290	2290	200	40	2
Д 2040	2040	200	40	2
Д 2010	2010	200	40	2
Д 1900	1900	200	40	2
Д 1820	1820	200	40	2
Д 1400	1400	200	40	4
Д 1280	1280	200	40	4
Д 1135	1135	200	40	2
Д 1005	1005	200	40	2
Д 725	725	200	40	2
Д 610	610	200	40	8
Д 580	580	200	40	2
Д 450	450	200	40	1
Д 240	240	200	40	1
Д 200	200	200	40	1
Б 3387	3387	150	100	1

Стена по оси Б (2-й этаж).

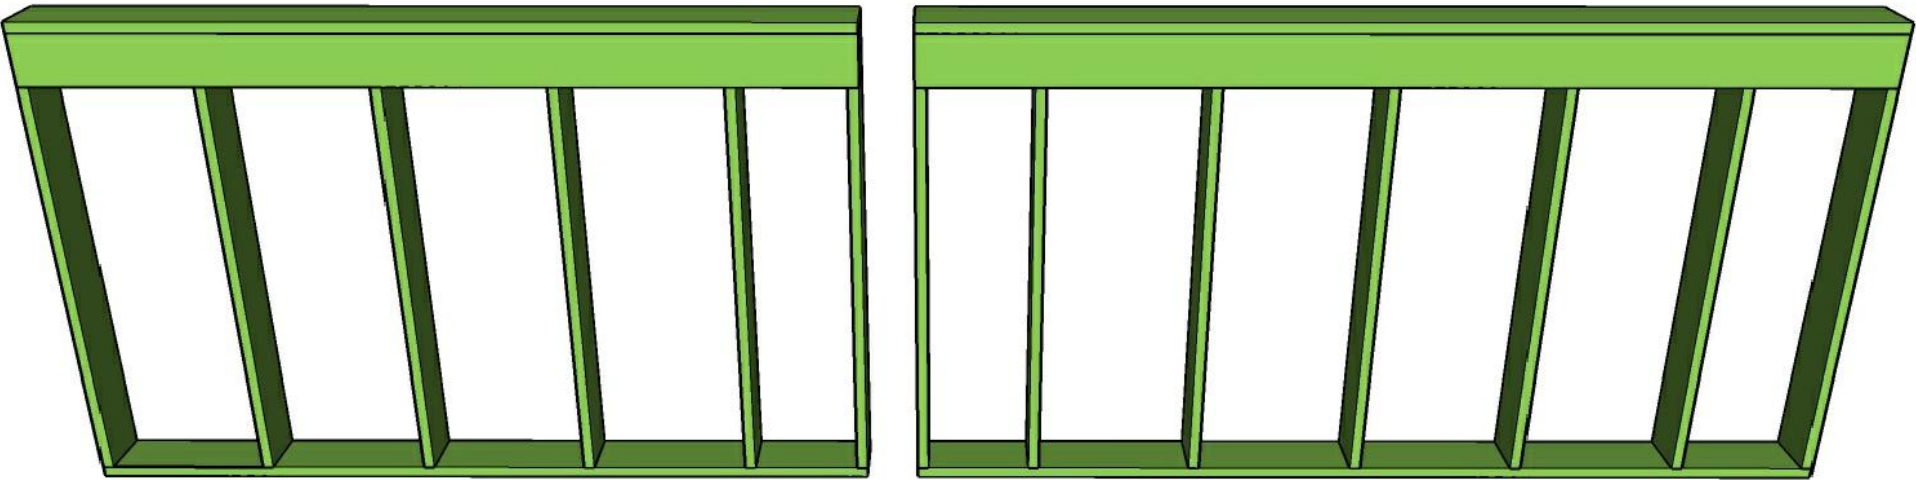


Расположение элементов каркаса.

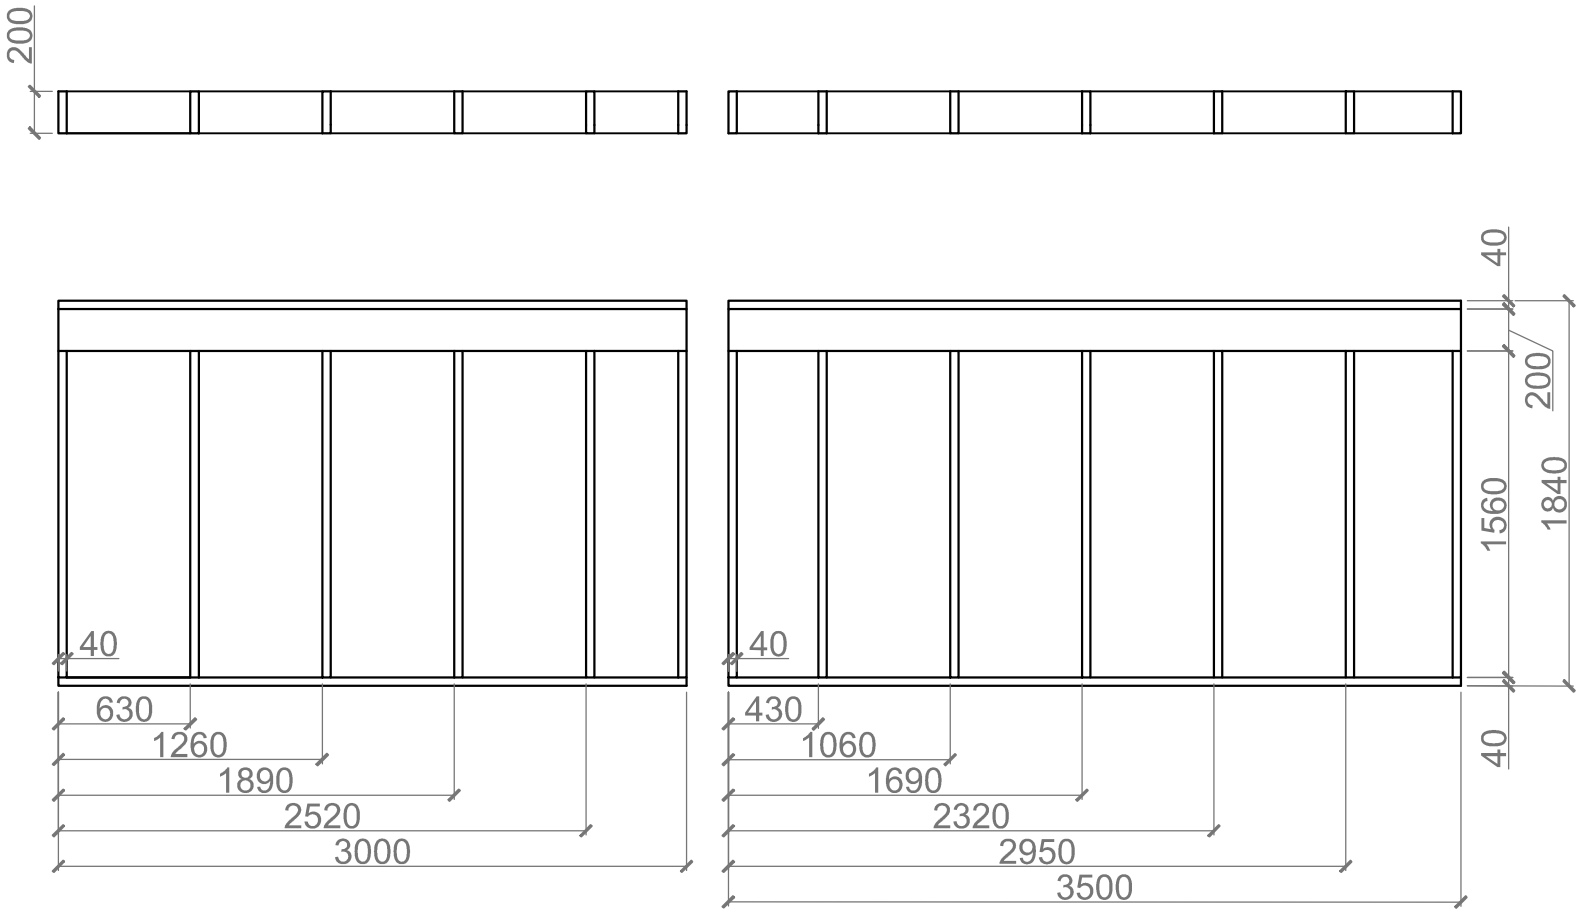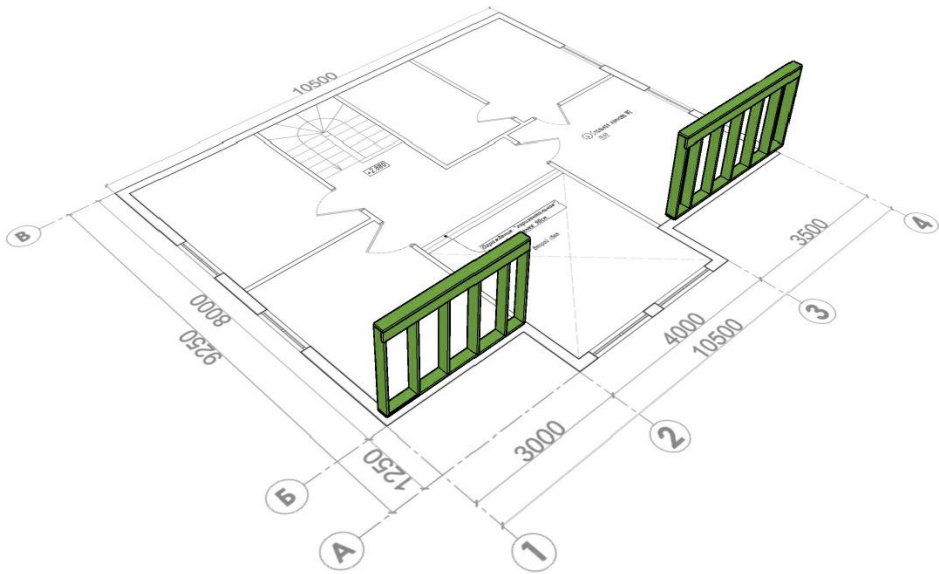


Экспликация:

Маркировка	Длина	Ширина	Толщина	Кол-во
Д 3500	3500	200	40	3
Д 3000	3000	200	40	3
Д 1760	1760	200	40	13

Стена по оси А (2-й этаж).

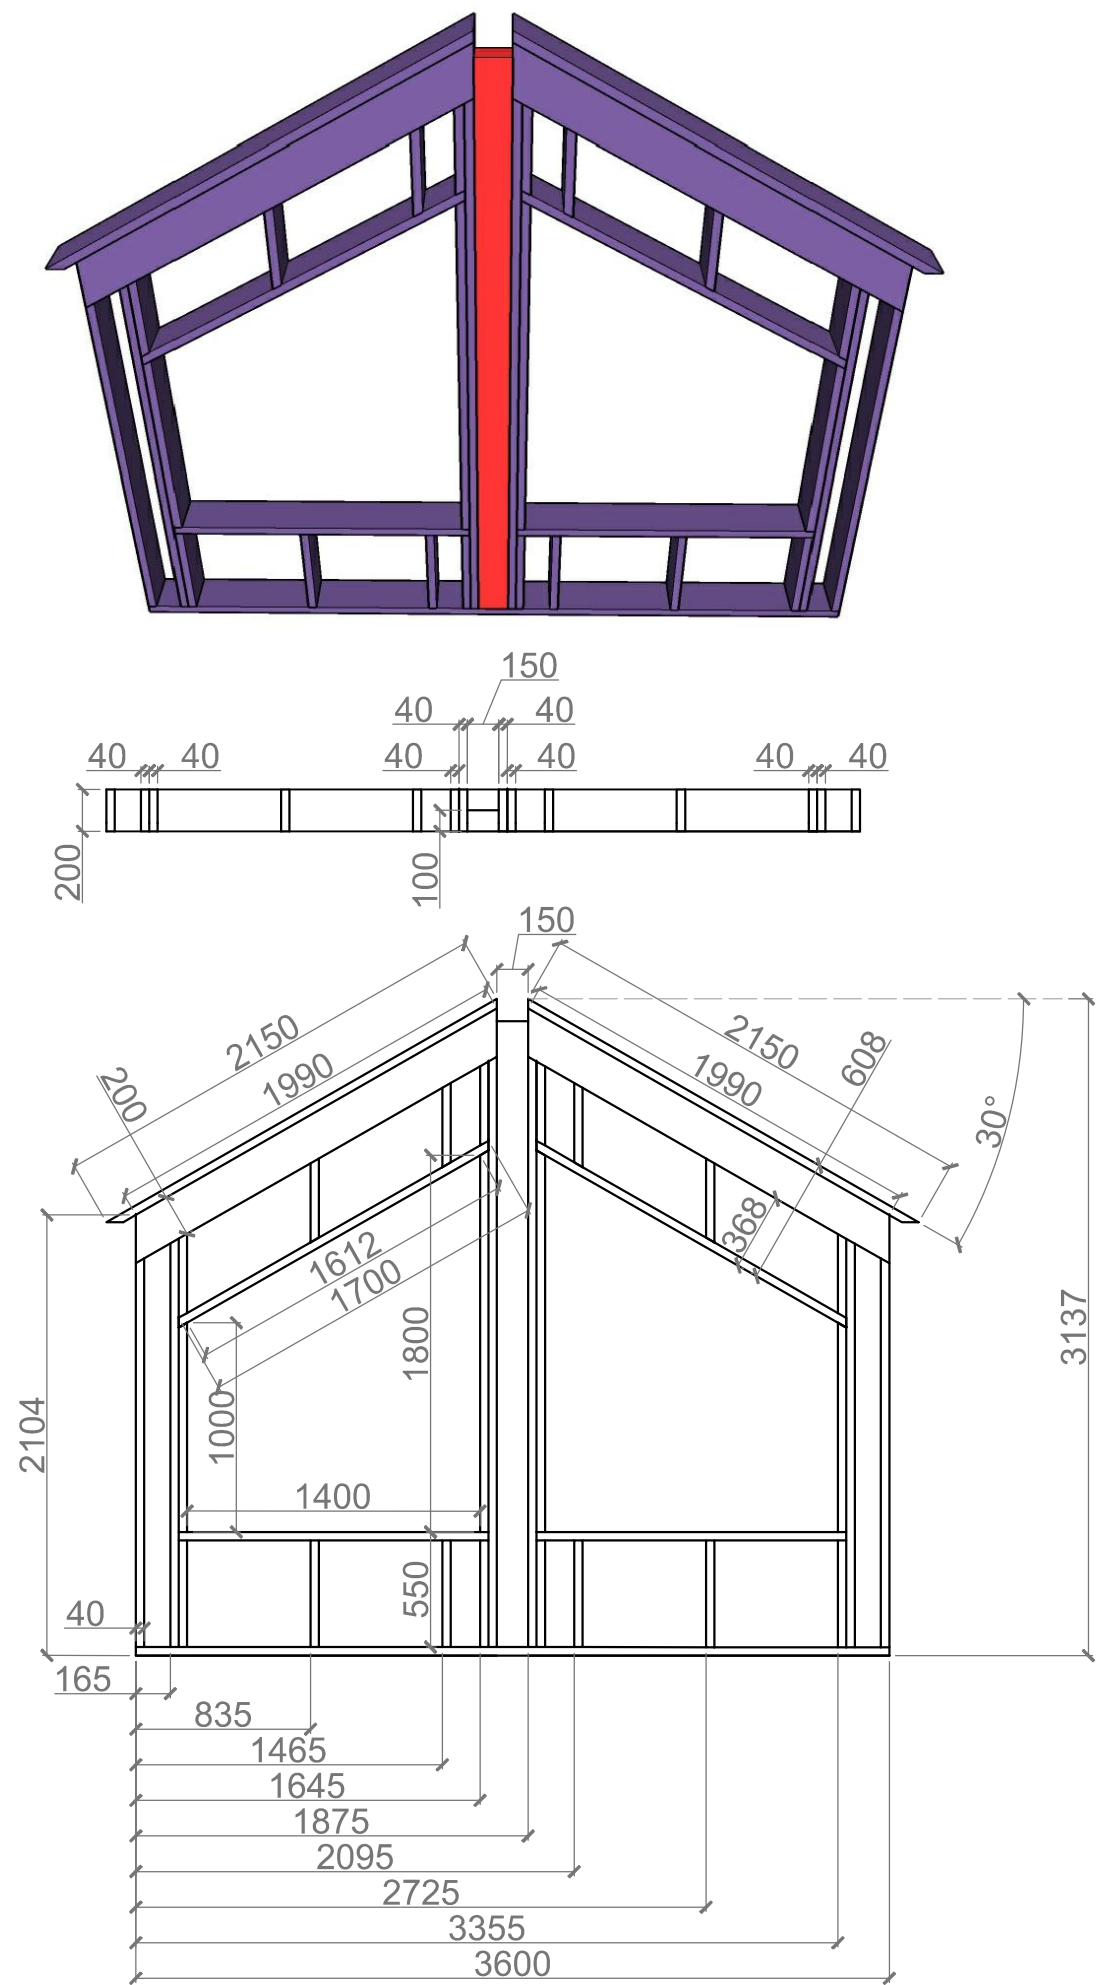

Расположение элементов каркаса.

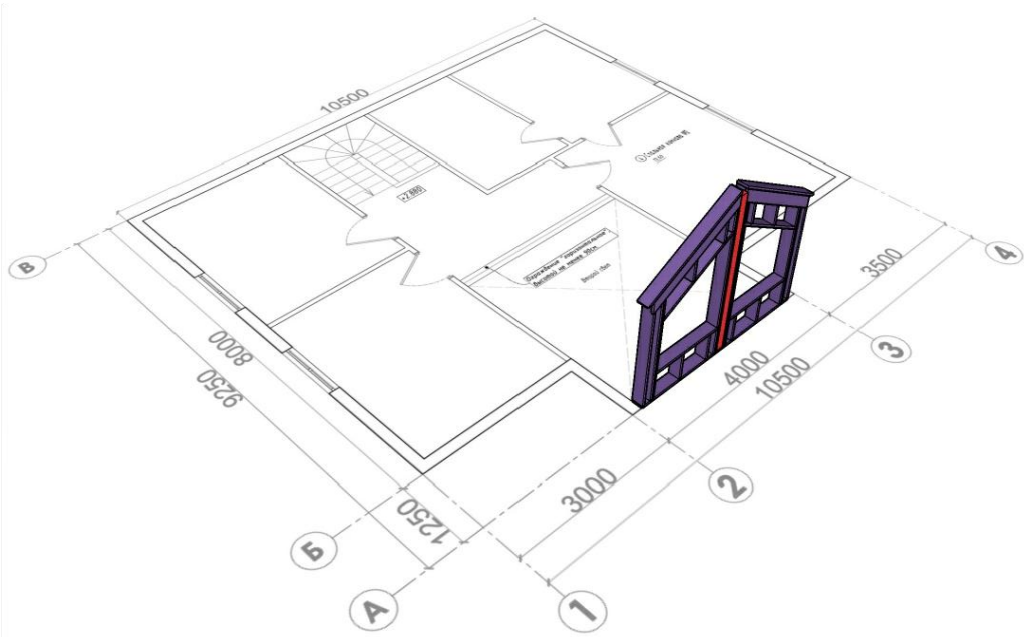


Экспликация:


Маркировка	Длина	Ширина	Толщина	Кол-во
Д 3600	3600	200	40	1
Д 3050	3050	200	40	2
Д 3030	3030	200	40	2
Д 2180	2180	200	40	2
Д 2150	2150	200	40	2
Д 2090	2090	200	40	2
Д 1990	1990	200	40	2
Д 1820	1820	200	40	2
Д 1700	1700	200	40	2
Д 1480	1480	200	40	2
Д 1000	1000	200	40	2
Д 630	630	200	40	8
Д 510	510	200	40	8
Б 2990	2990	150	100	1

Изм.	Кол. уч.	Лист	№ док.	Подп.	Дата	Стена по оси А (2-й этаж).	Лист
							31

Стена по оси 2 (2-й этаж).

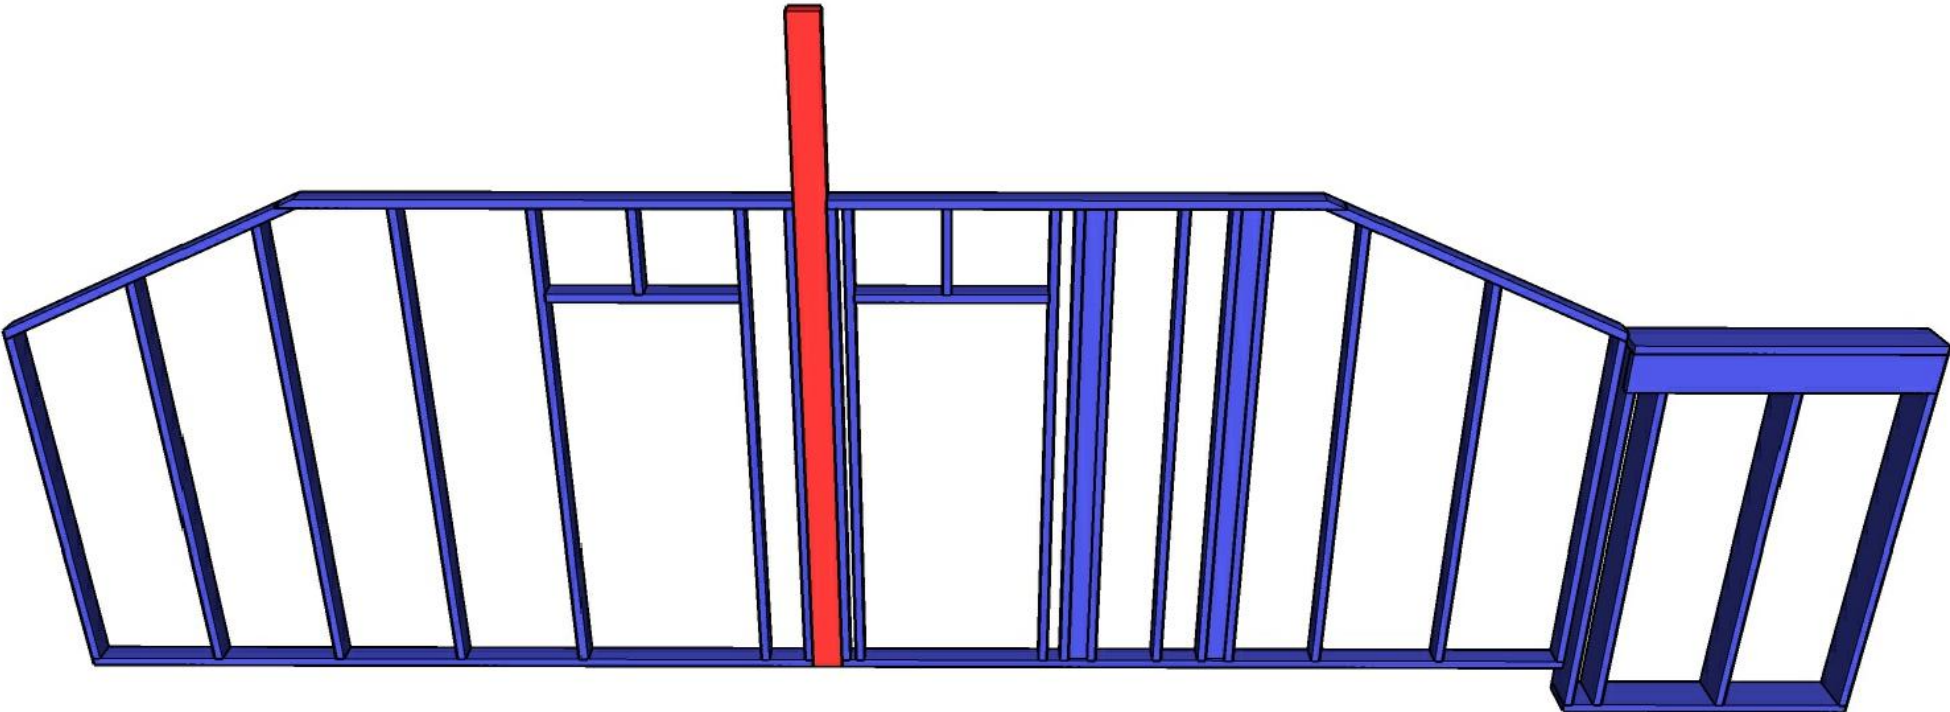


Расположение элементов каркаса.

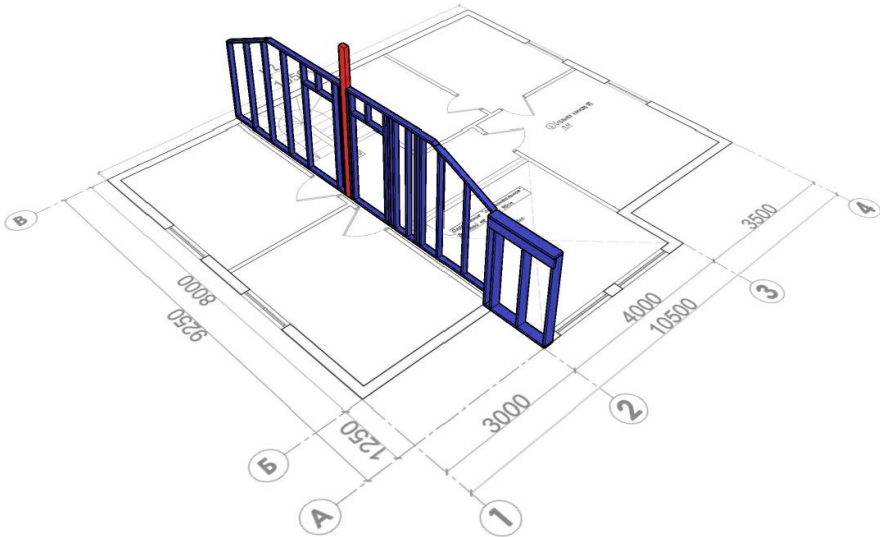

Экспликация:


Маркировка	Длина	Ширина	Толщина	Кол-во
Д 1450	1450	200	40	3
Д 1990	1990	200	40	4
Д 3724	3724	100	40	1
Д 2460	2460	100	40	16
Д 2380	2380	100	40	2
Д 2260	2260	100	40	2
Д 2100	2100	100	40	2
Д 1820	1820	100	40	2
Д 1620	1620	100	40	2
Д 900	900	100	40	2
Д 420	420	100	40	2
Б 3387	3387	150	100	1

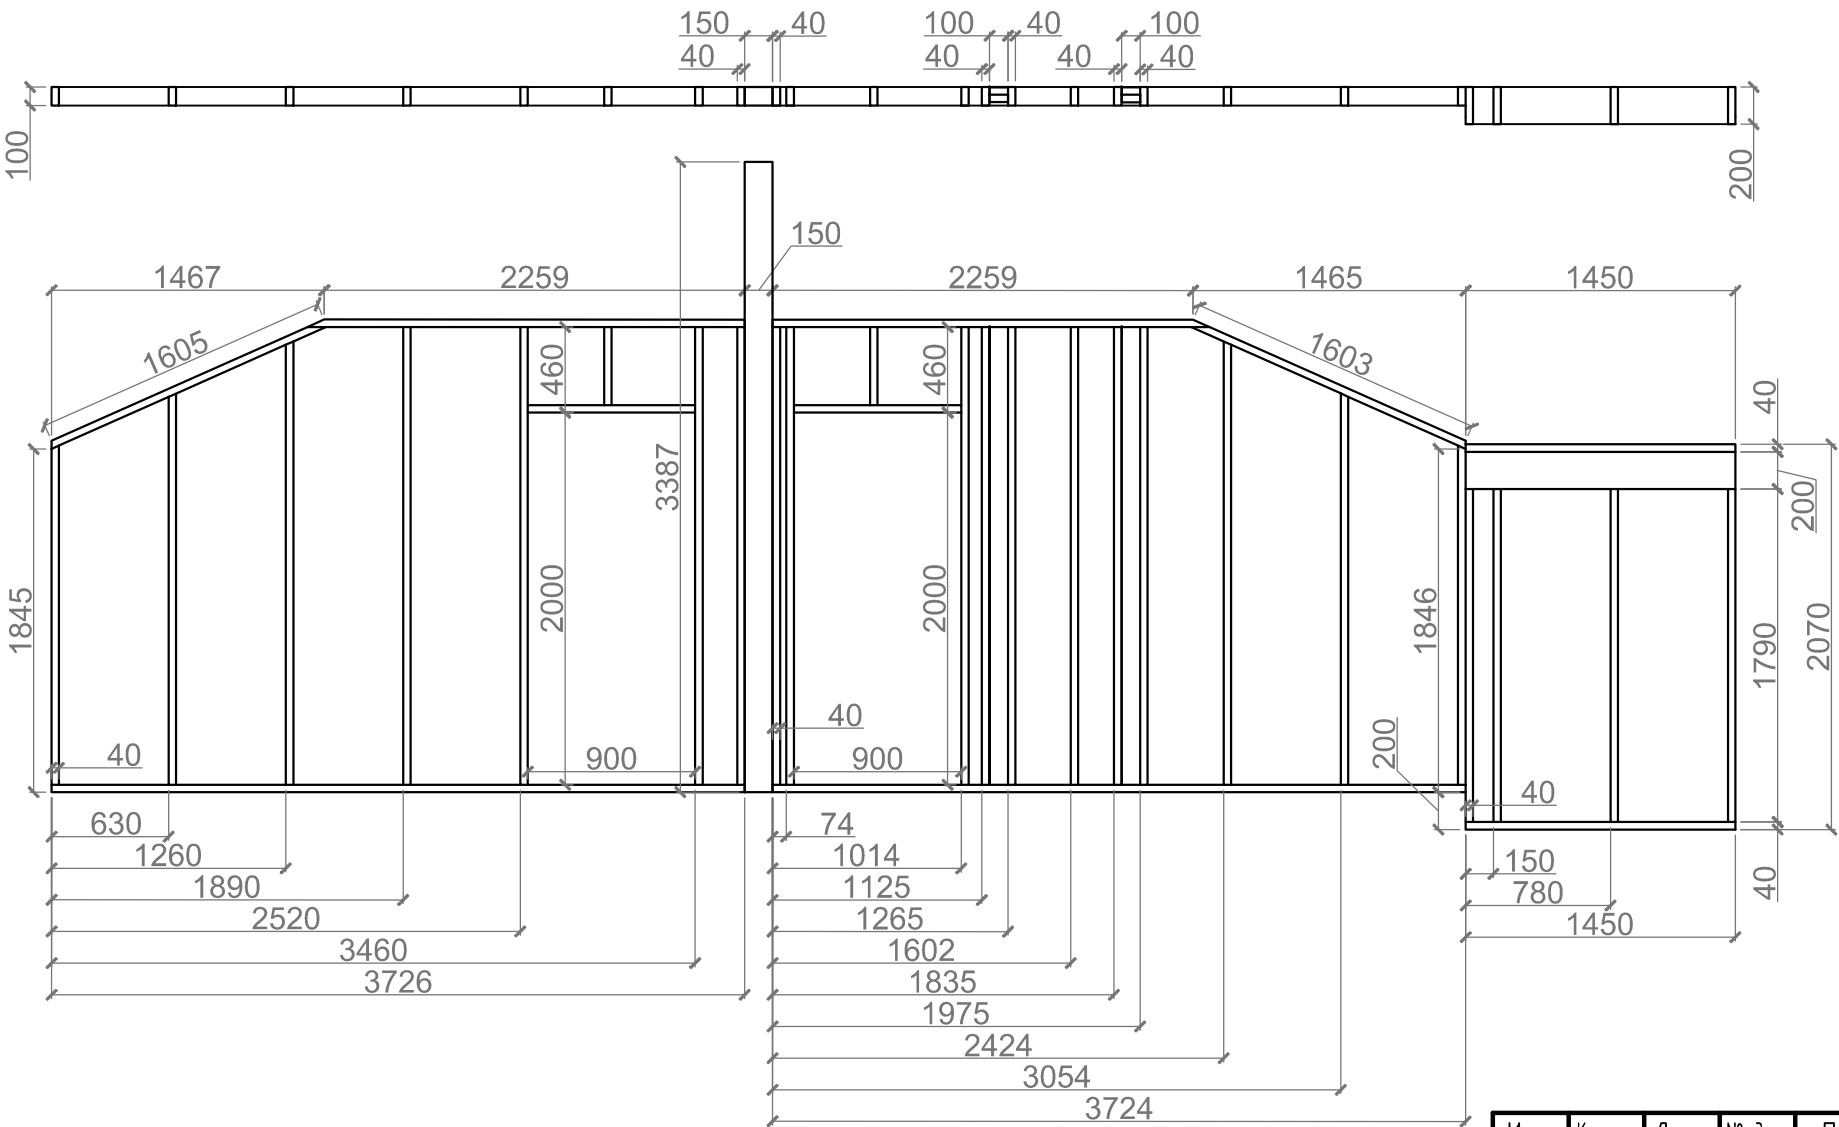


Изм.	Кол. уч.	Лист	№ док.	Подп.	Дата

Стена по оси 2 (2-й этаж).

Стена по оси 3 (2-й этаж).

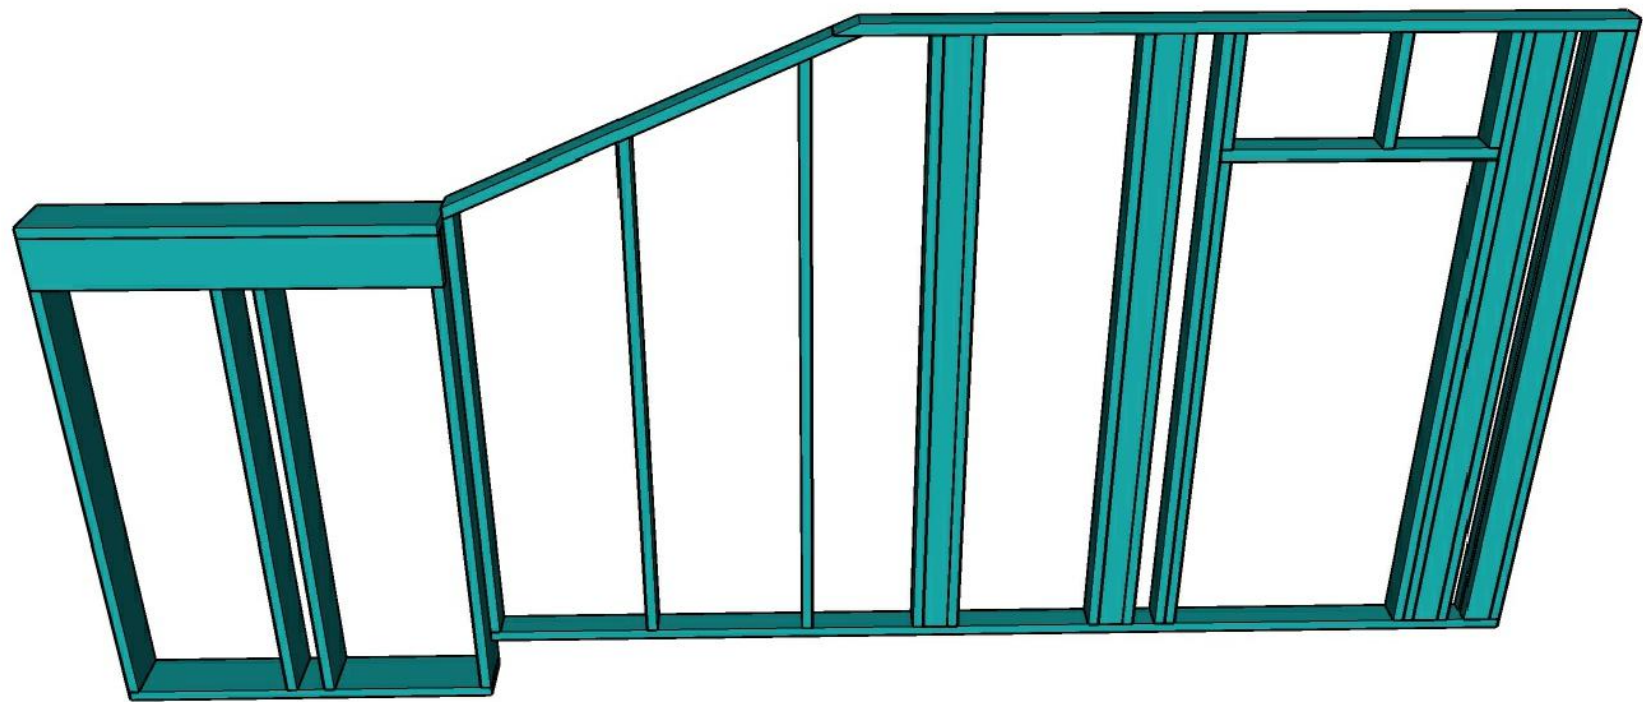


Расположение элементов каркаса.

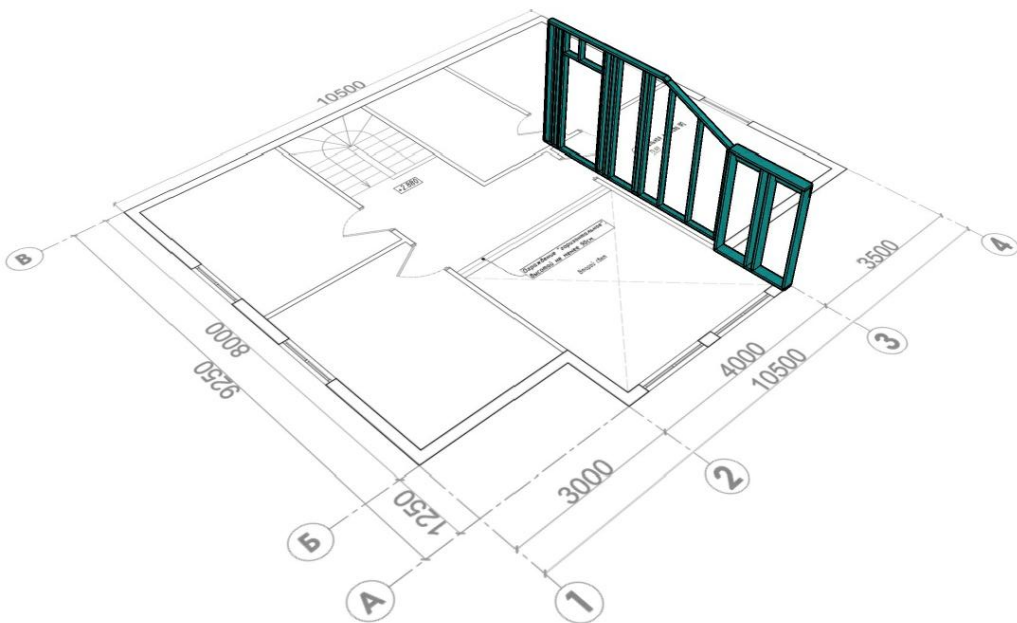


Экспликация:

Маркировка	Длина	Ширина	Толщина	Кол-во
Д 1450	1450	200	40	3
Д 1990	1990	200	40	4
Д 4100	4100	100	40	1
Д 2635	2635	100	40	1
Д 2460	2460	100	40	16
Д 2380	2380	100	40	1
Д 2100	2100	100	40	1
Д 1820	1820	100	40	1
Д 1620	1620	100	40	1
Д 980	980	100	40	1
Д 420	420	100	40	3

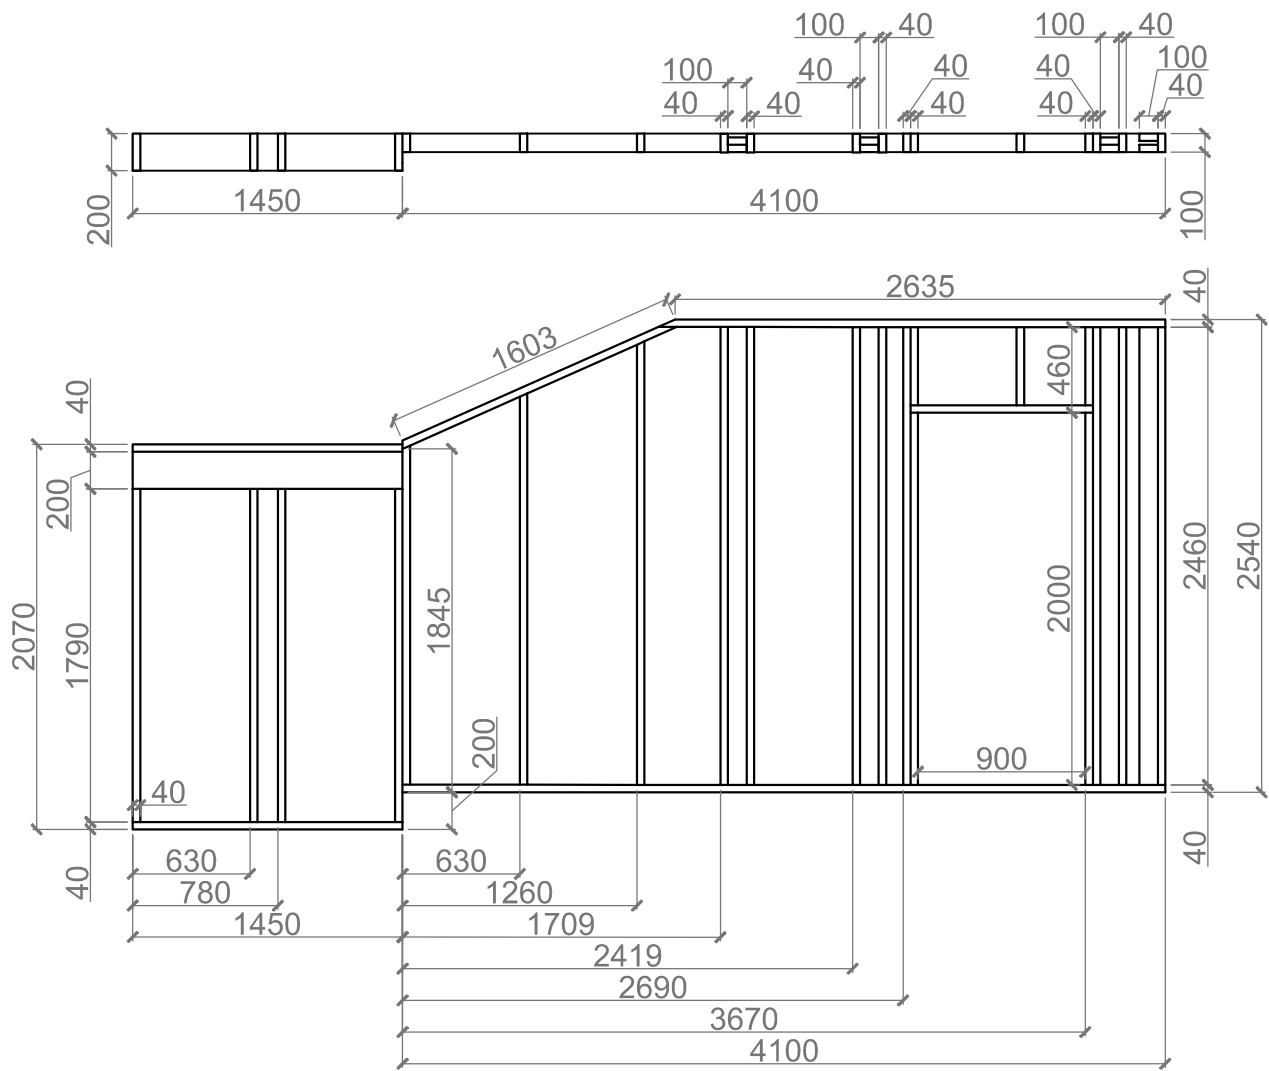


Изм.	Кол. уч.	Лист	№ док.	Подп.	Дата	Стена по оси 3 (2-й этаж).	Лист
							33

Перегородка 1 (2-й этаж).

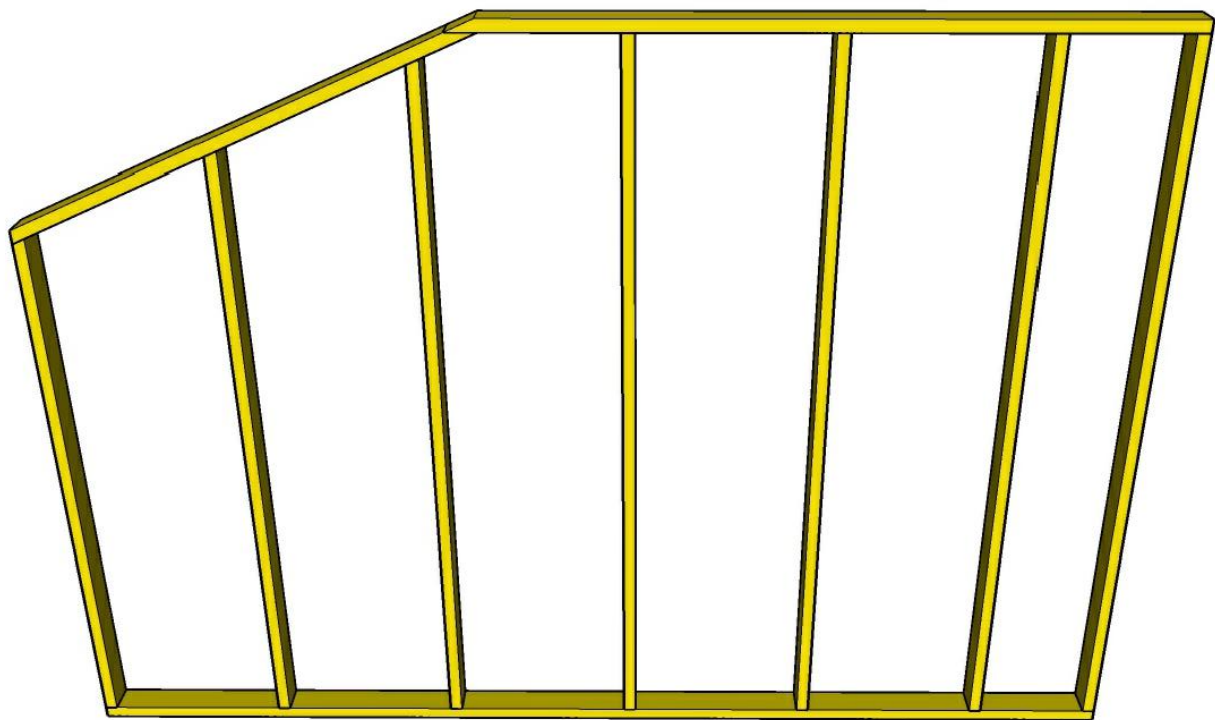


Расположение элементов каркаса.

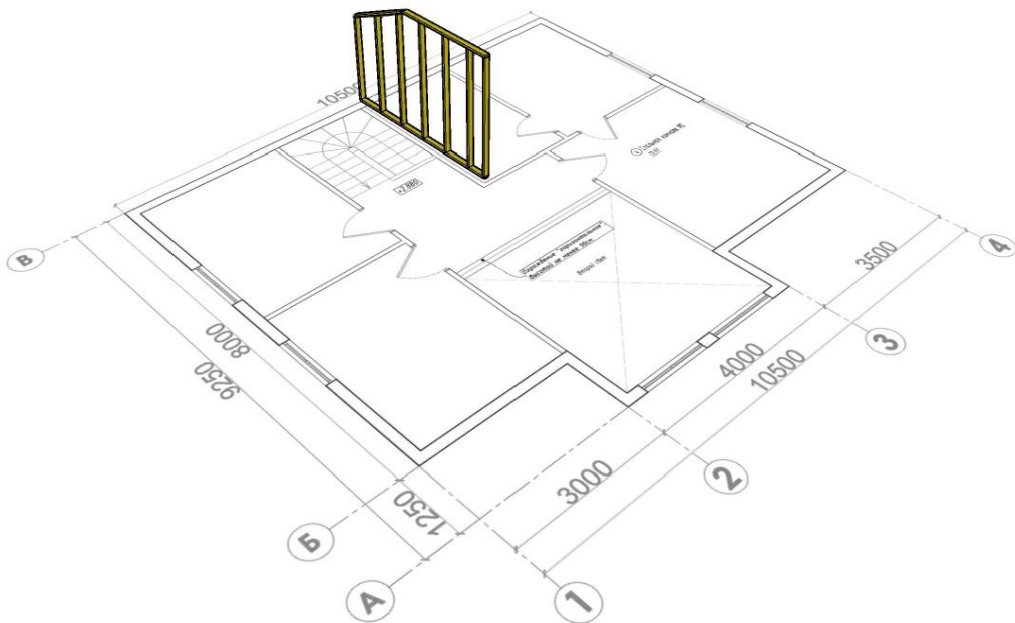


Экспликация:


Маркировка	Длина	Ширина	Толщина	Кол-во
Д 3600	3600	100	40	1
Д 2460	2460	100	40	4
Д 2382	2382	100	40	1
Д 2133	2133	100	40	1
Д 2100	2100	100	40	1
Д 2033	2033	100	40	1
Д 1822	1822	100	40	1
Д 1605	1605	100	40	1

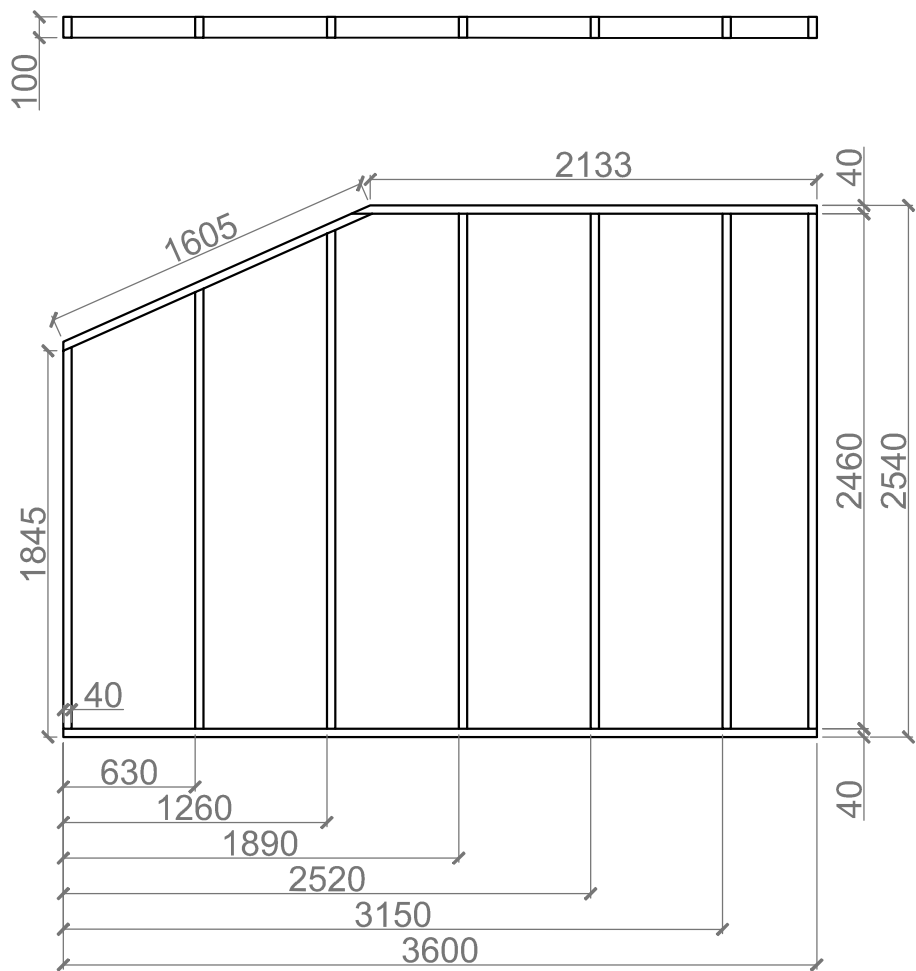

Перезгородка 2 (2-й этаж).

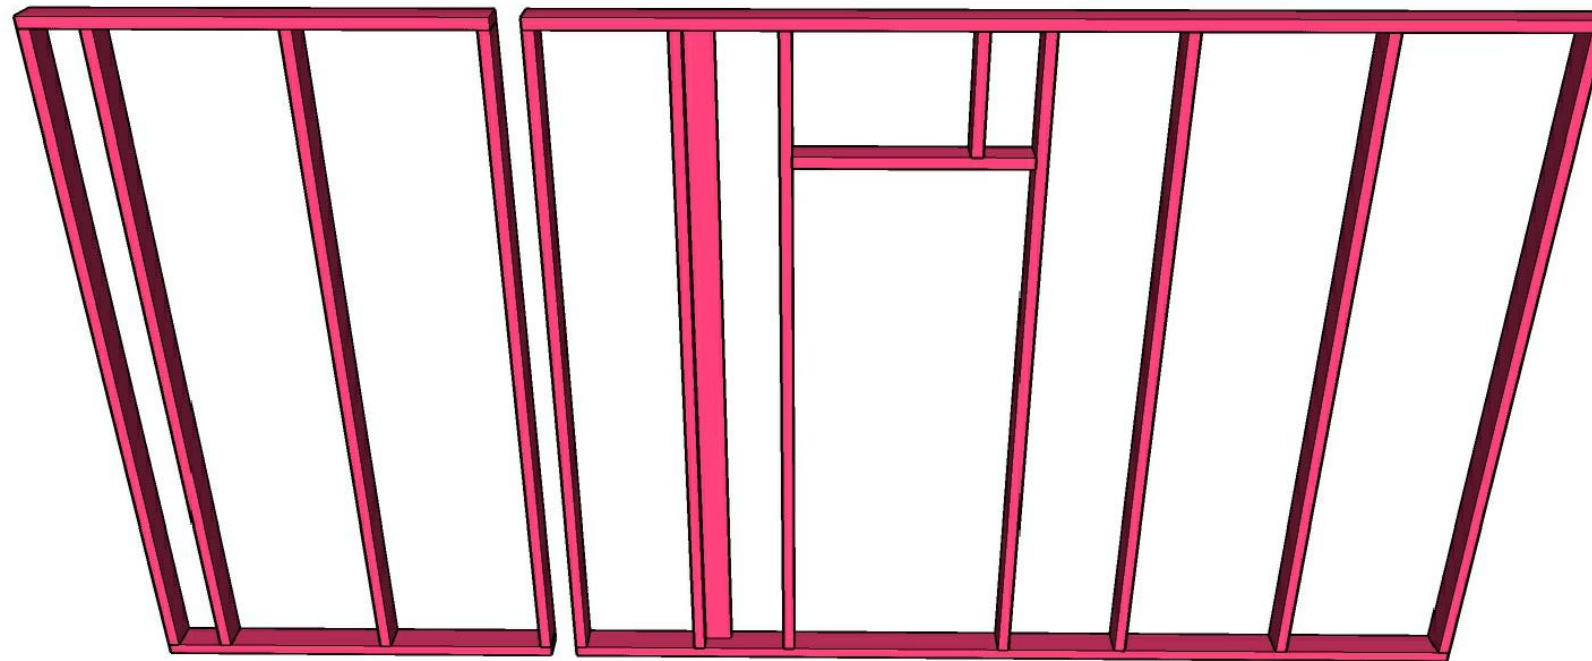


Расположение элементов каркаса.

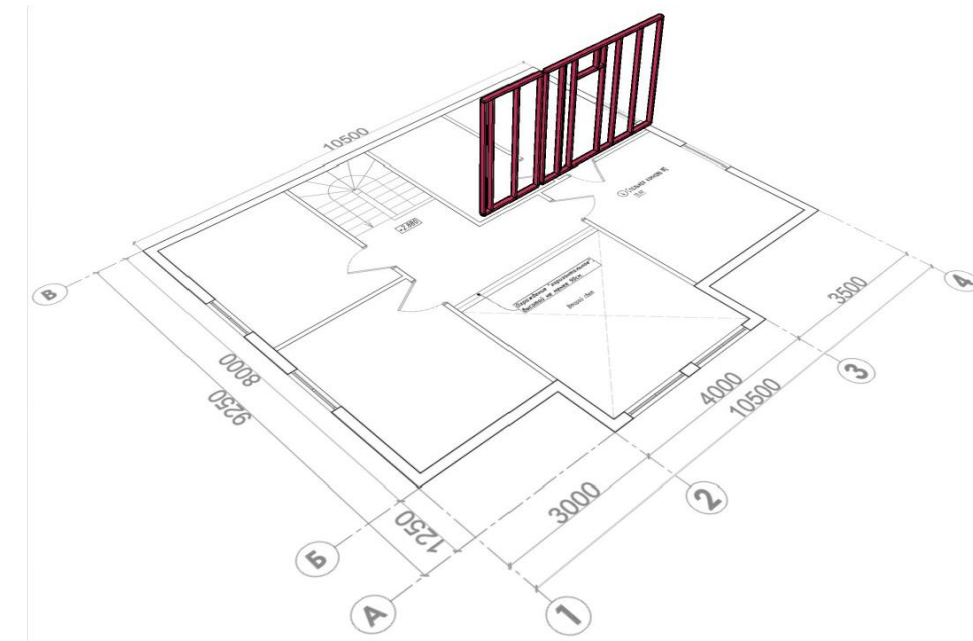

Экспликация:

Маркировка	Длина	Ширина	Толщина	Кол-во
Д 1500	1500	100	40	2
Д 3400	3400	100	40	2
Д 2460	2460	100	40	11
Д 800	800	100	40	1
Д 420	420	100	40	1


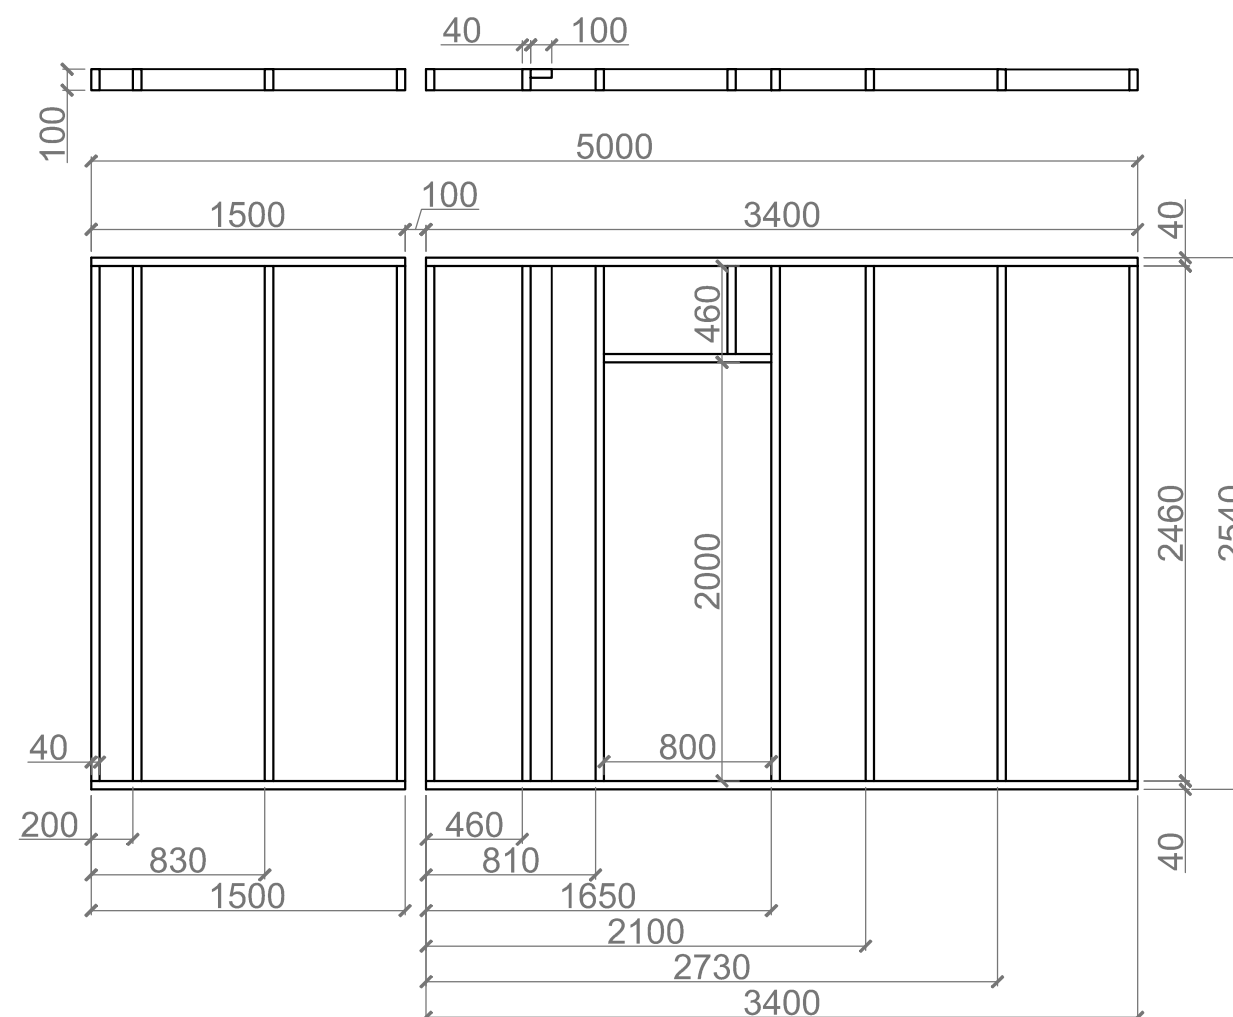


Изм.	Кол. уч.	Лист	№ док.	Подп.	Дата


Перезгородка 2 (2-й этаж).

Лист
35

Стена по оси 1 (2-й этаж).

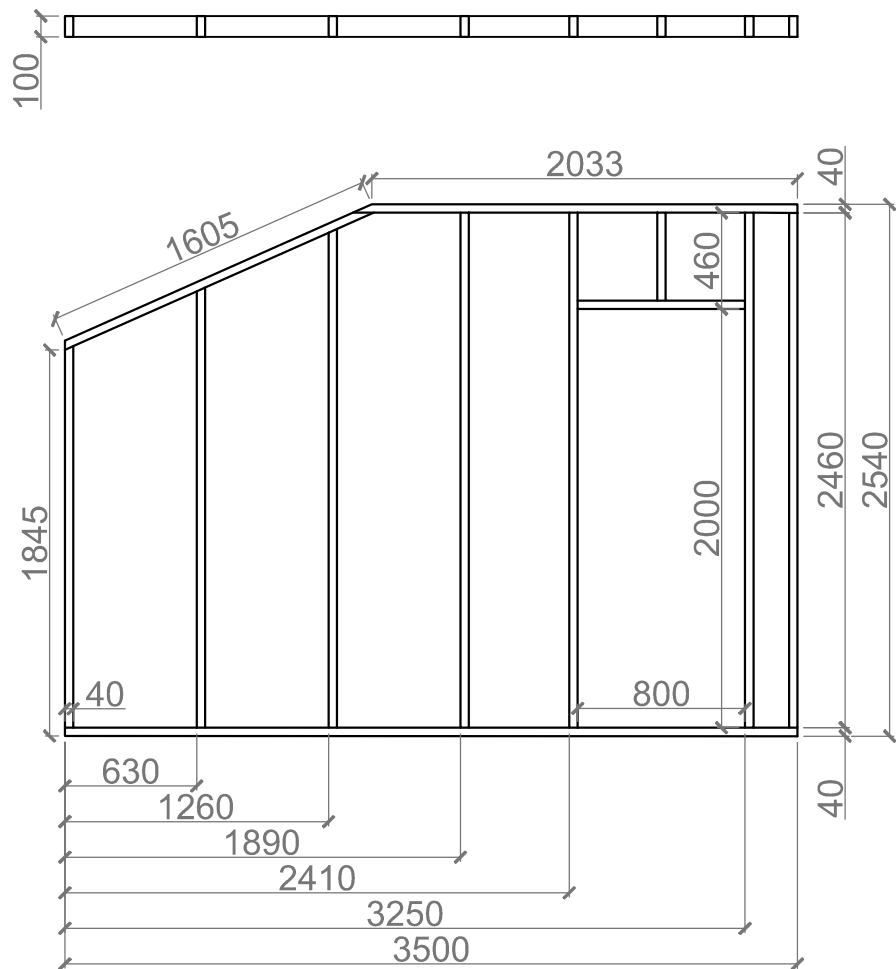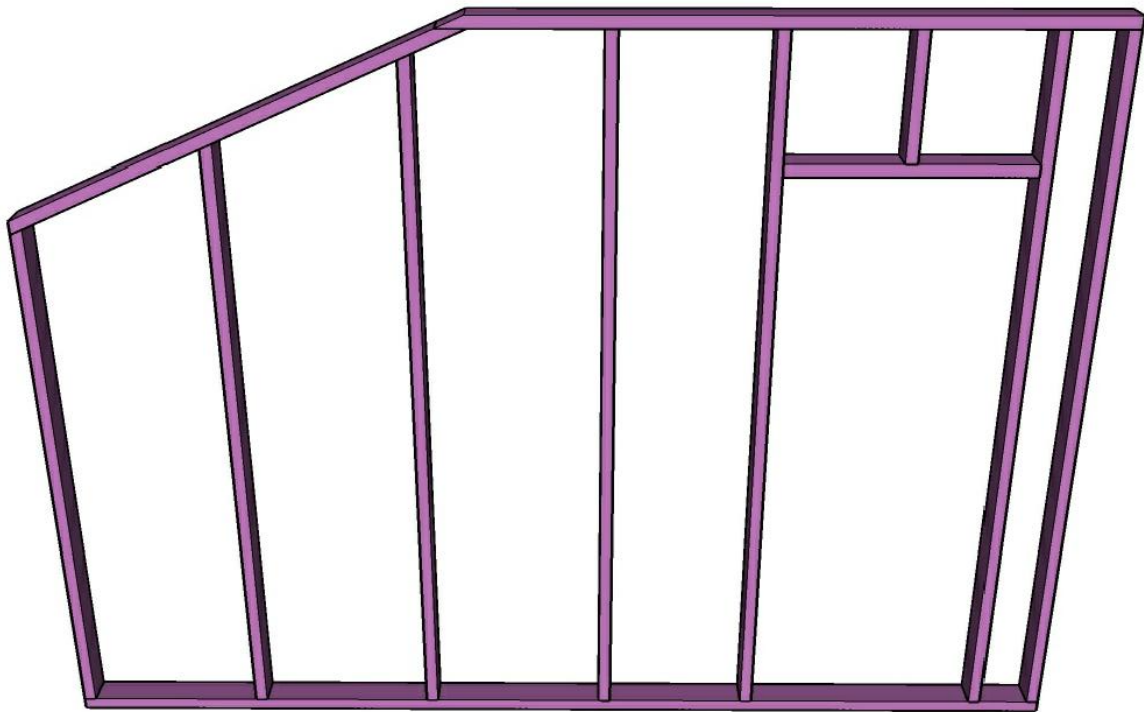




Расположение элементов каркаса.

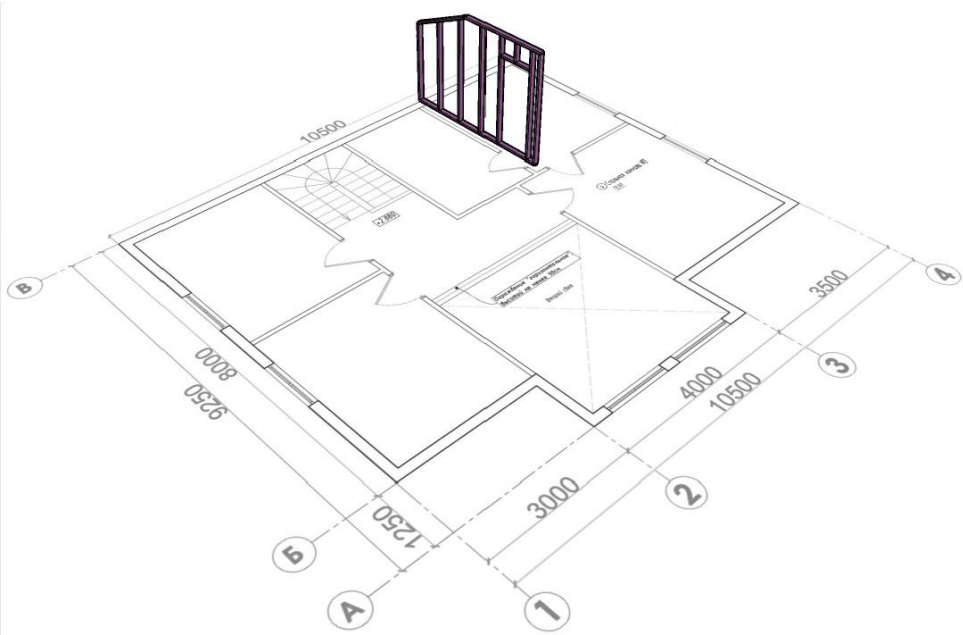


Экспликация:

Маркировка	Длина	Ширина	Толщина	Кол-во
Д 3500	3500	100	40	1
Д 2460	2460	100	40	4
Д 2382	2382	100	40	1
Д 2100	2100	100	40	1
Д 2033	2033	100	40	1
Д 1822	1822	100	40	1
Д 1605	1605	100	40	1
Д 800	800	100	40	1
Д 420	420	100	40	1

Стена по оси 1 (2-й этаж).

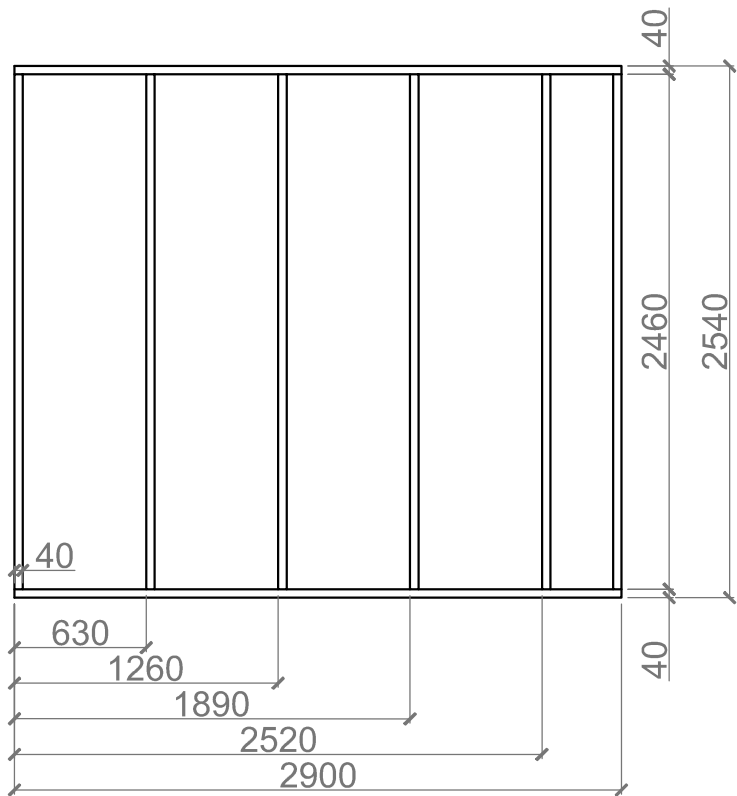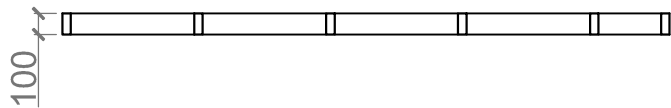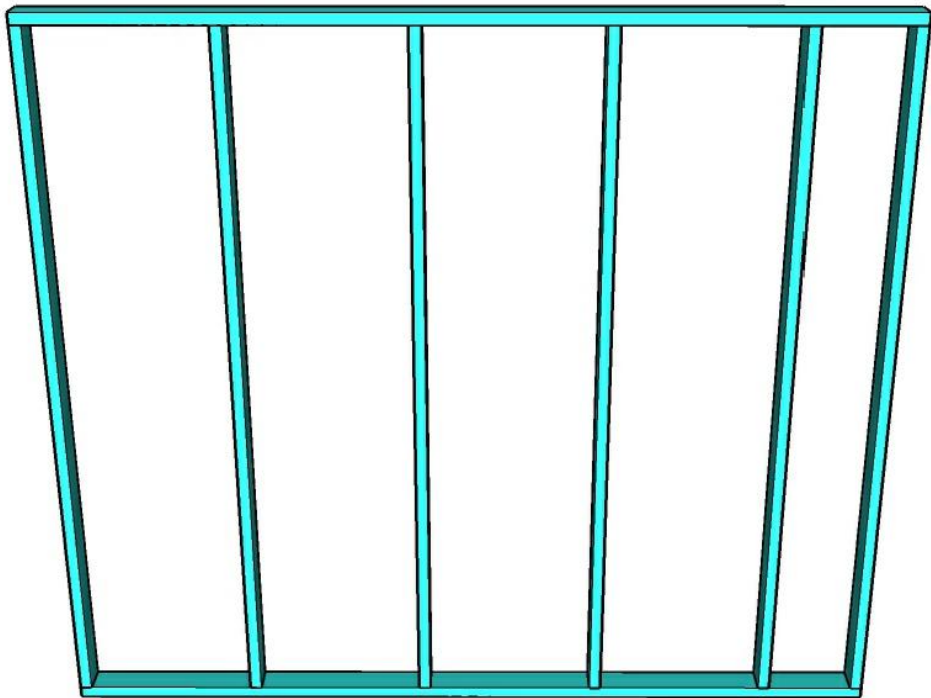


Расположение элементов каркаса.

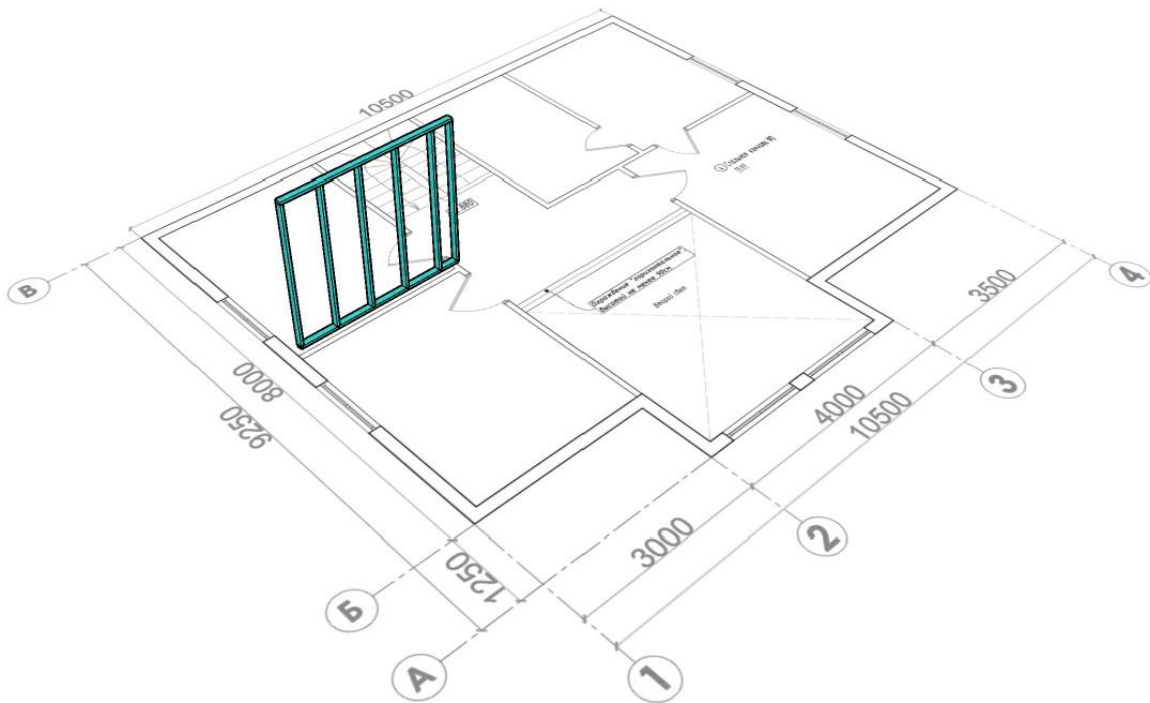

Экспликация:

Маркировка	Длина	Ширина	Толщина	Кол-во
Д 2900	2900	100	40	2
Д 2460	2460	100	40	6


Коньковая система. Общий вид.

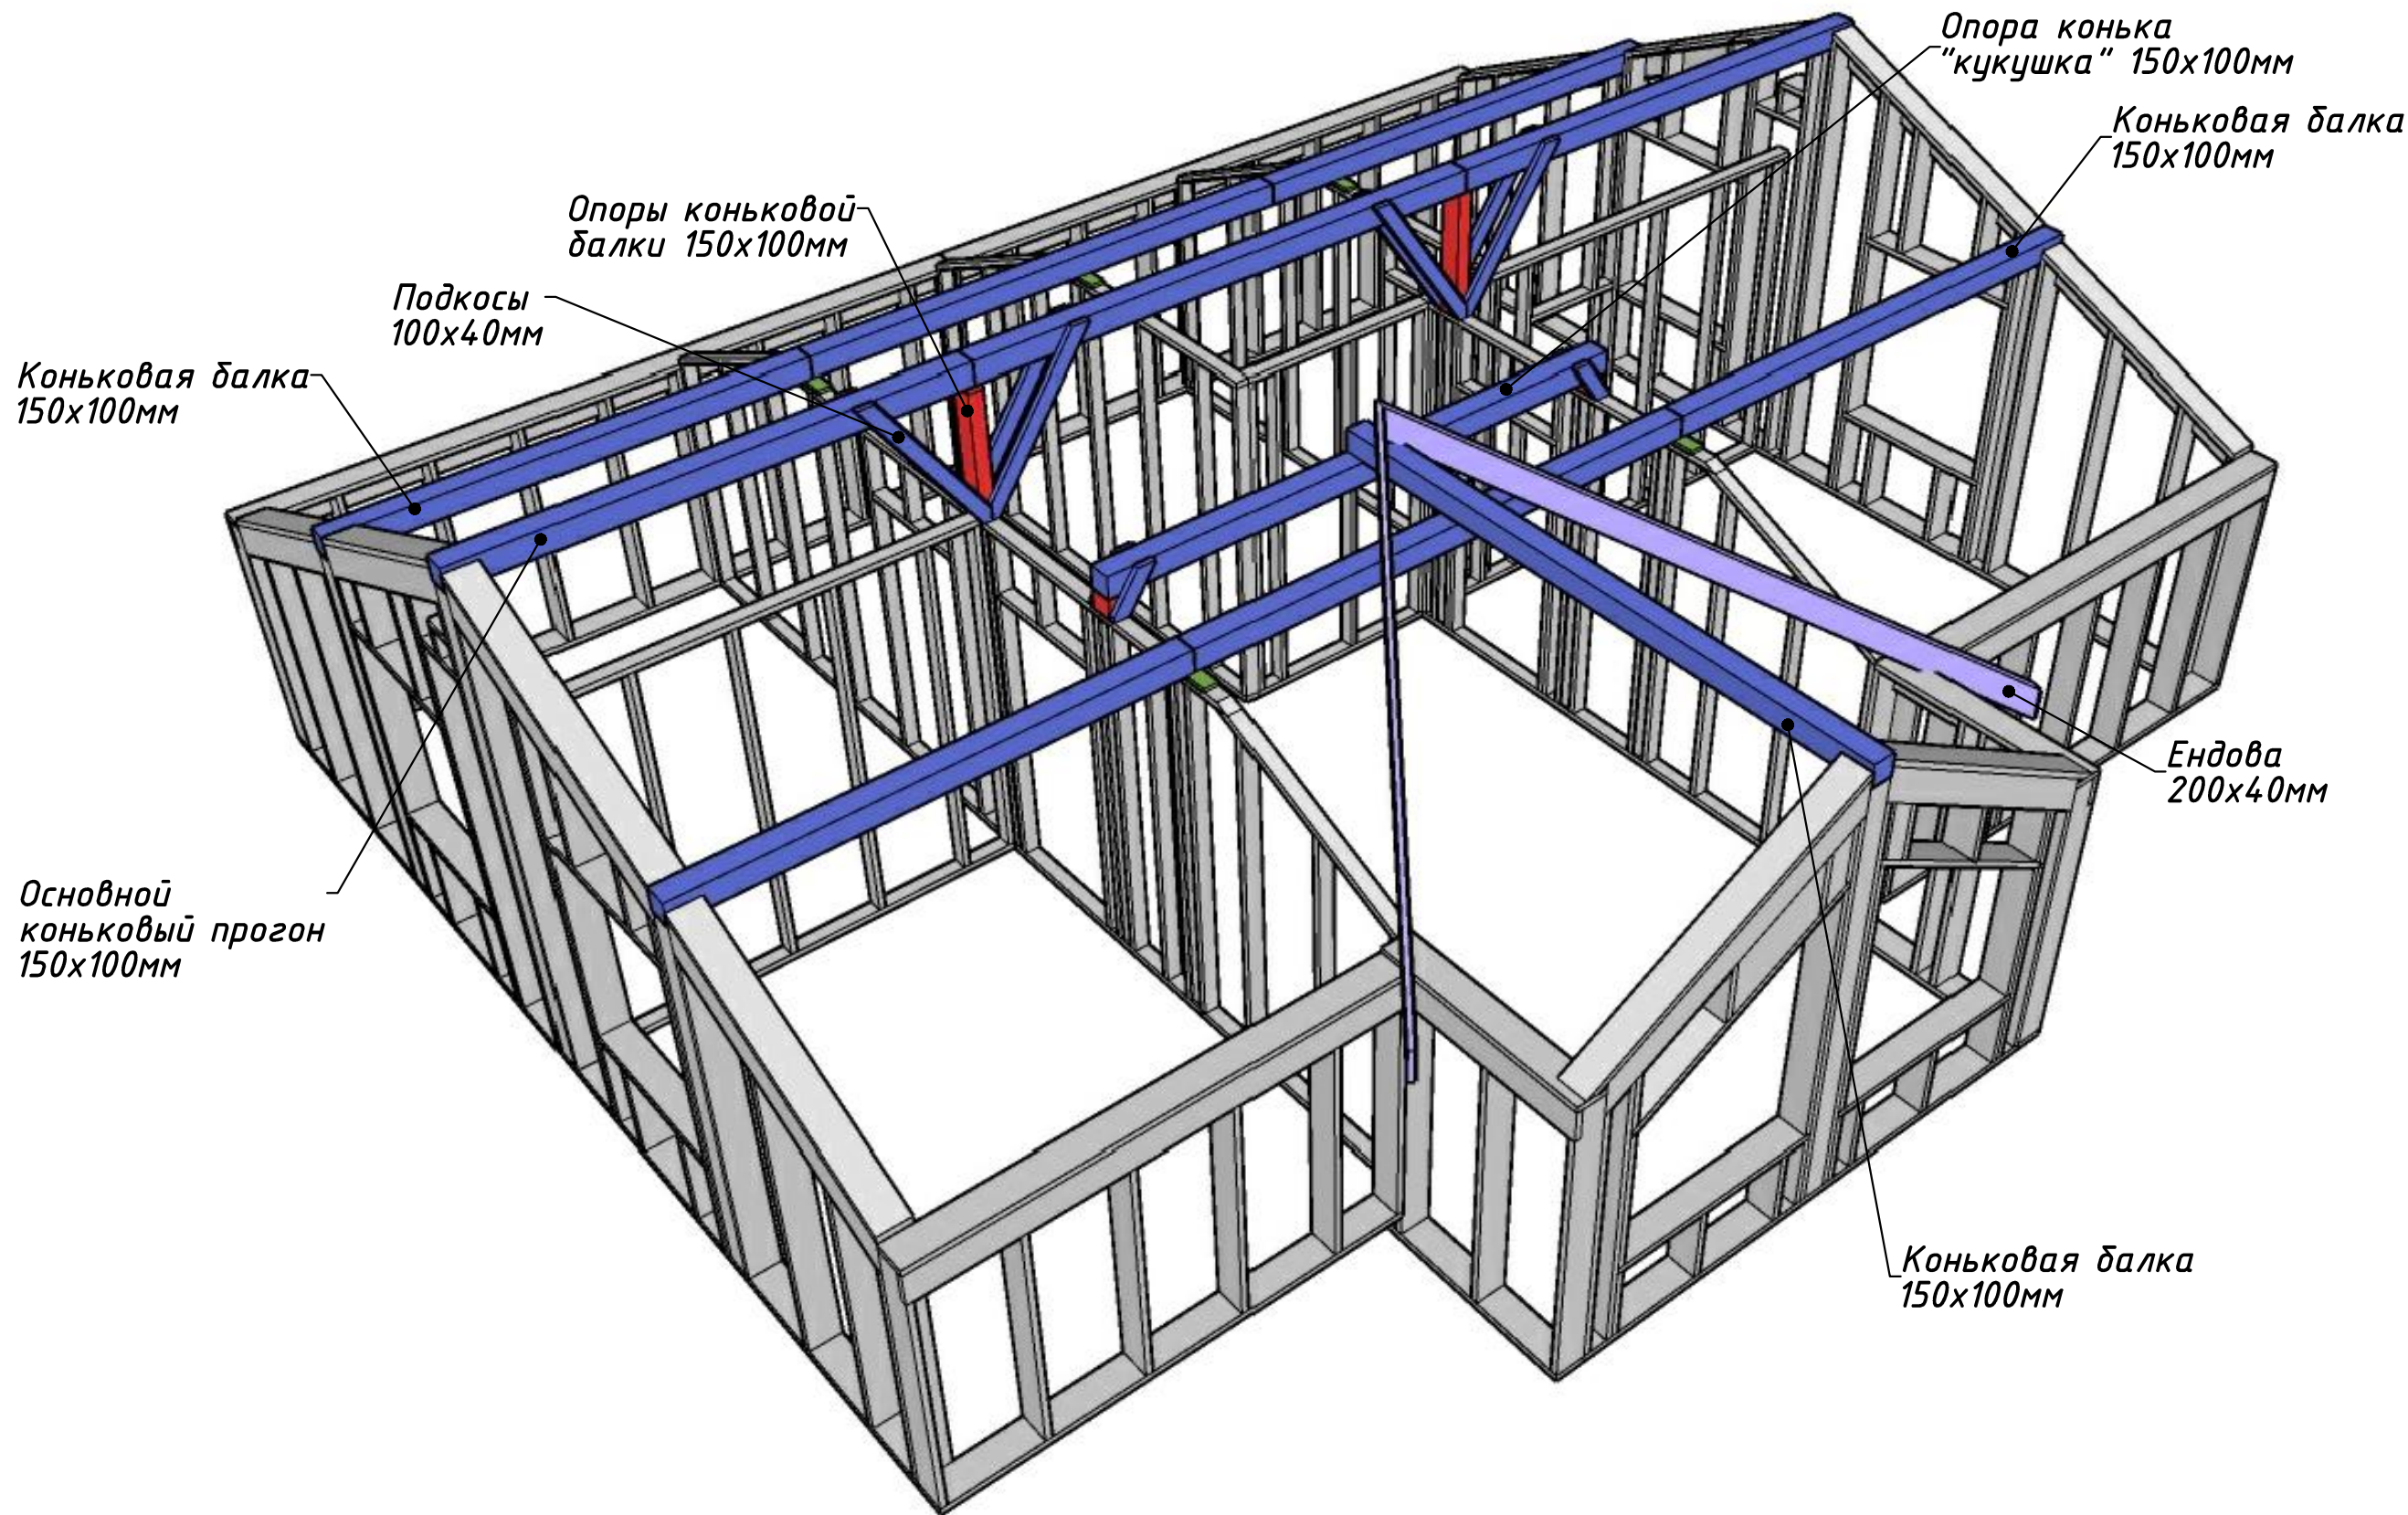


Изм.	Кол. уч.	Лист	№ док.	Подп.	Дата

Коньковая система. Общий вид.

Коньковая система.

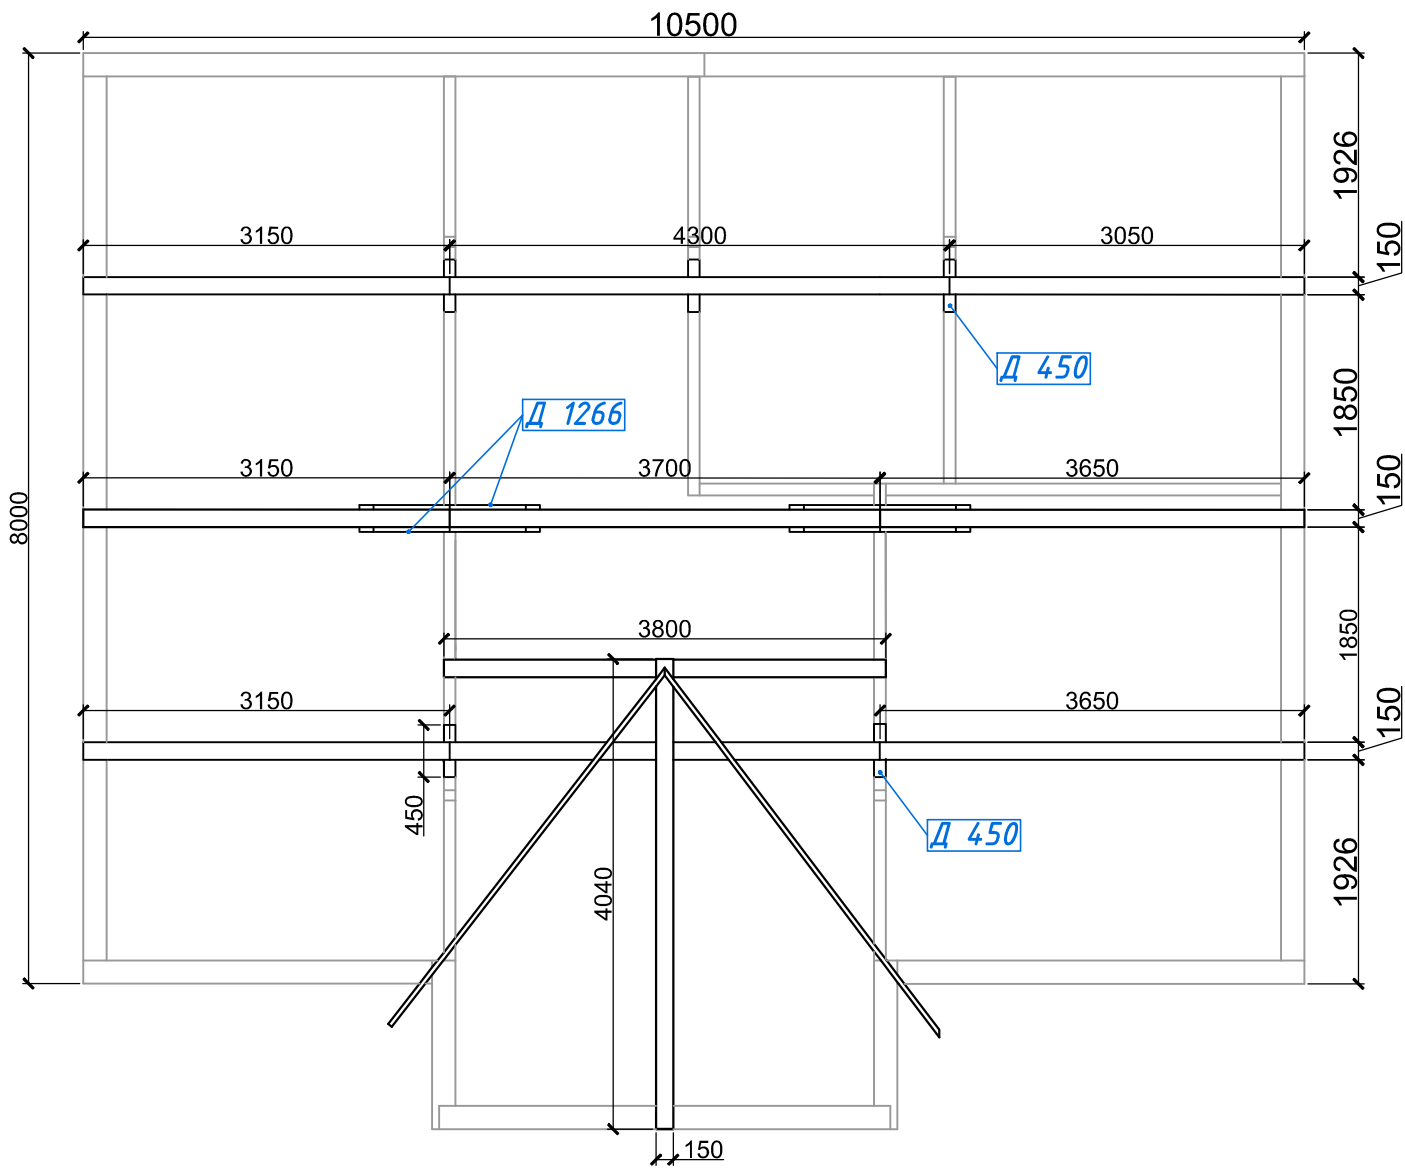


Расположение элементов каркаса.

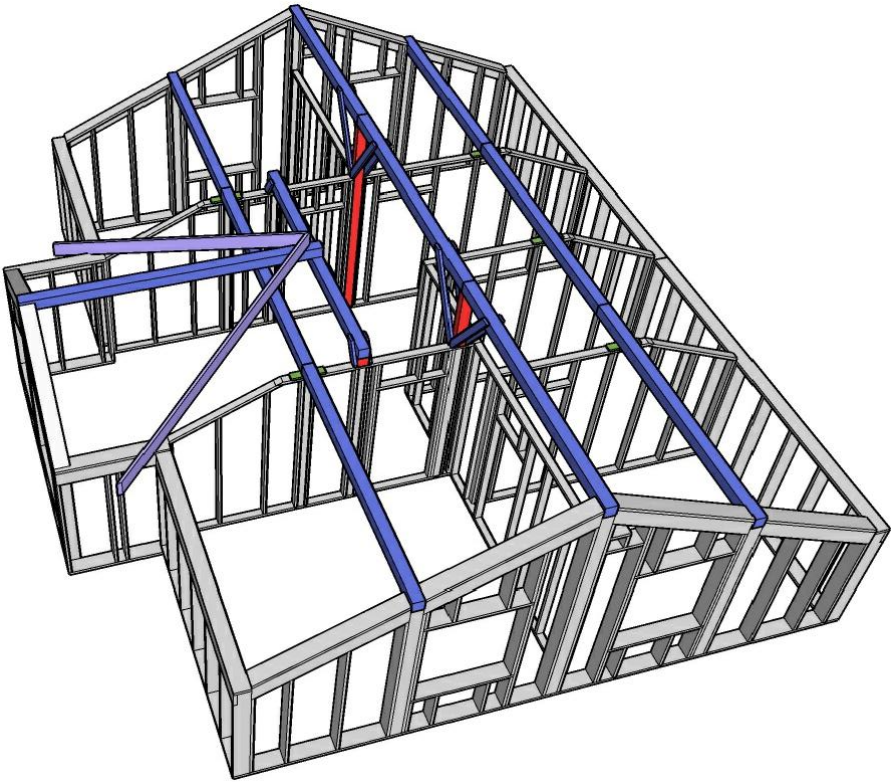



Экспликация:

Маркировка	Длина	Ширина	Толщина	Кол-во
Б 4300	4300	150	150	1
Б 4040	4040	150	150	1
Б 3800	3800	150	150	1
Б 3700	3700	150	150	2
Б 3650	3650	150	150	2
Б 3150	3150	150	150	2
Б 890	890	150	100	1
Б 140	1400	150	100	2
Д 1266	1266	150	40	8
Д 450	450	100	40	5
Д 354	354	100	40	4


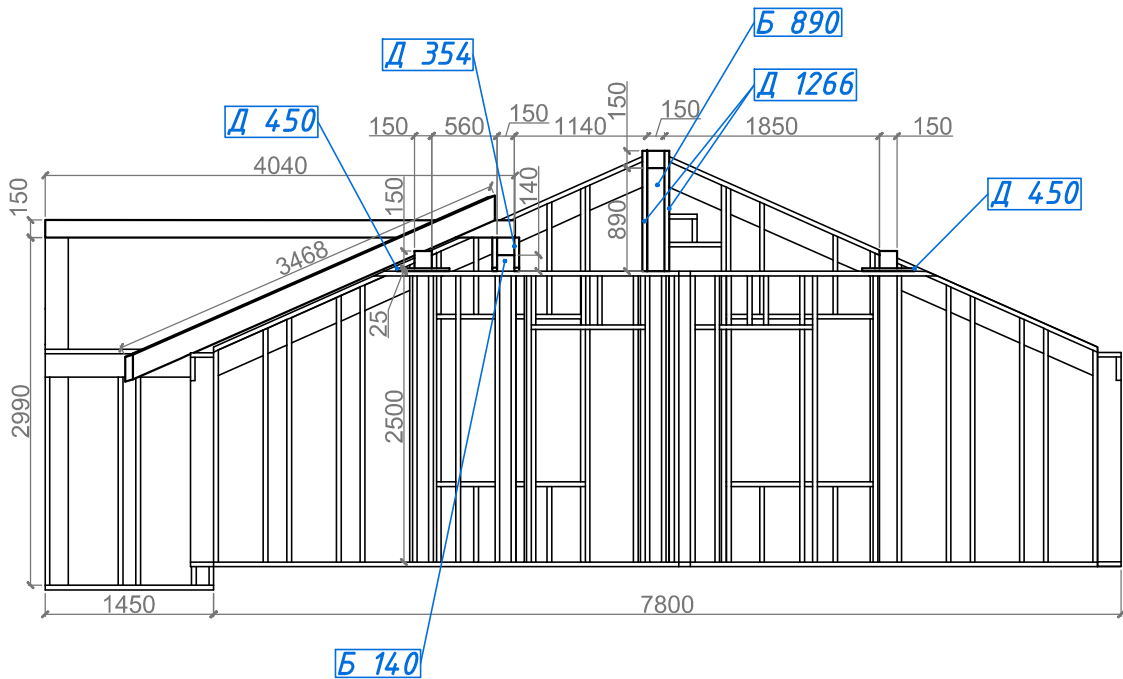


Изм.	Кол. уч.	Лист	№ док.	Подп.	Дата	Коньковая система (начало).	Лист
							39

Коньковая система основной крыши.

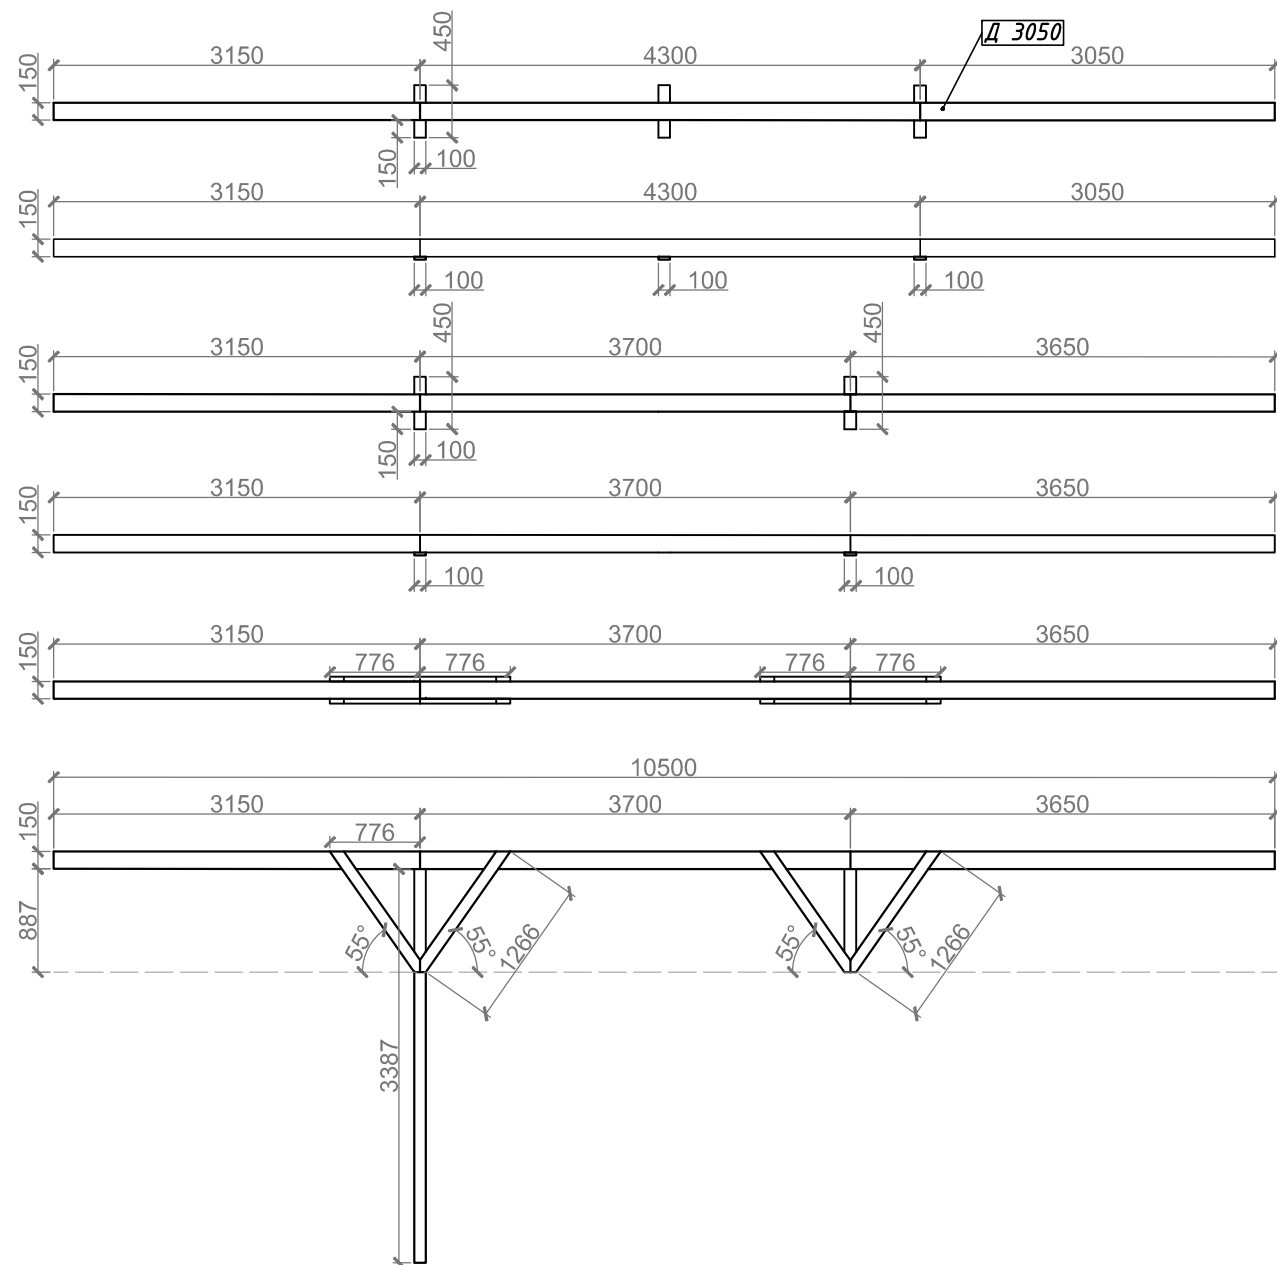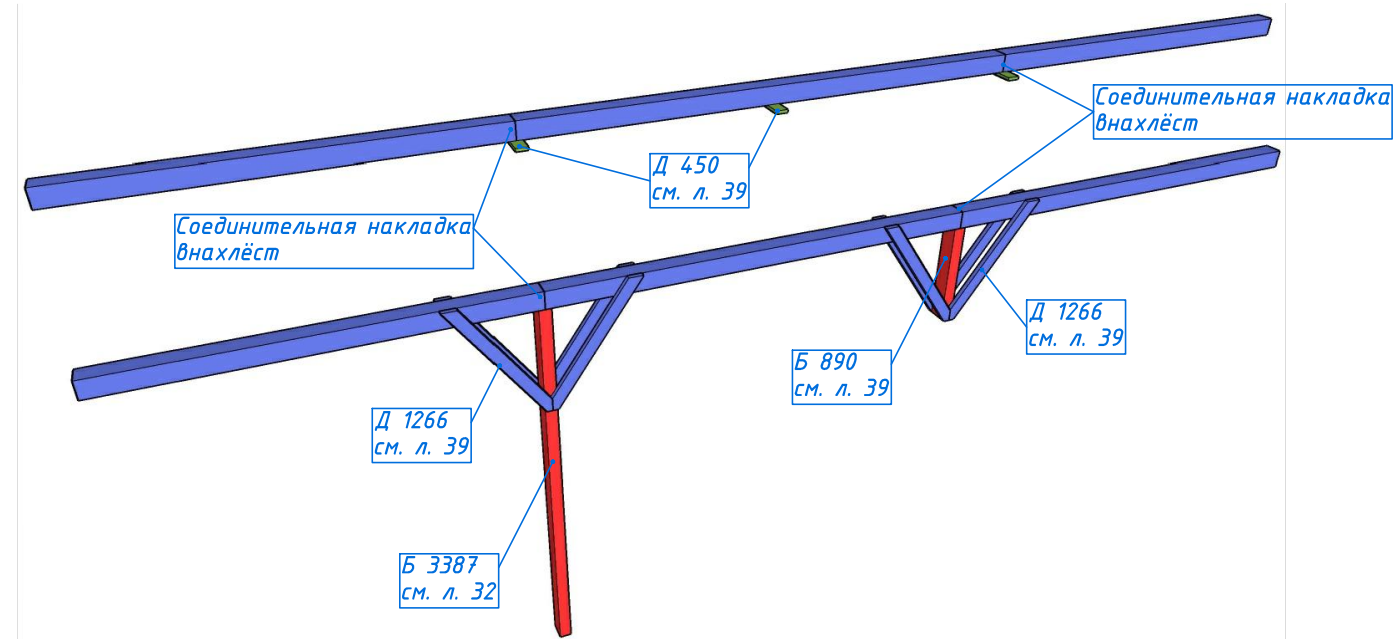

Коньковая система "кукушка".

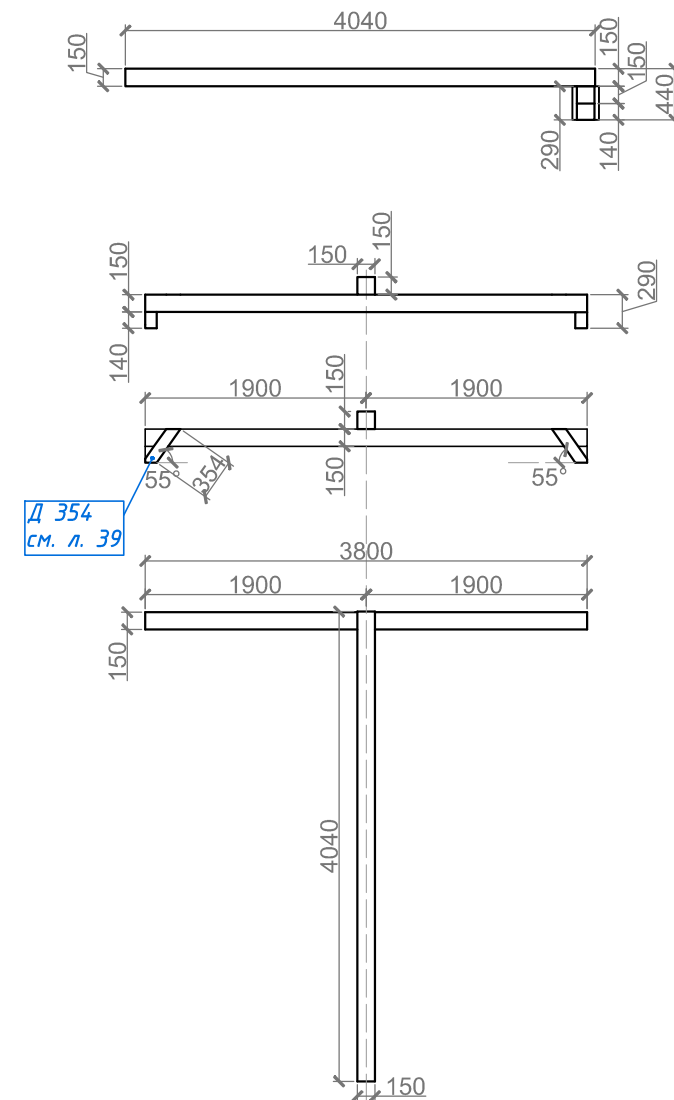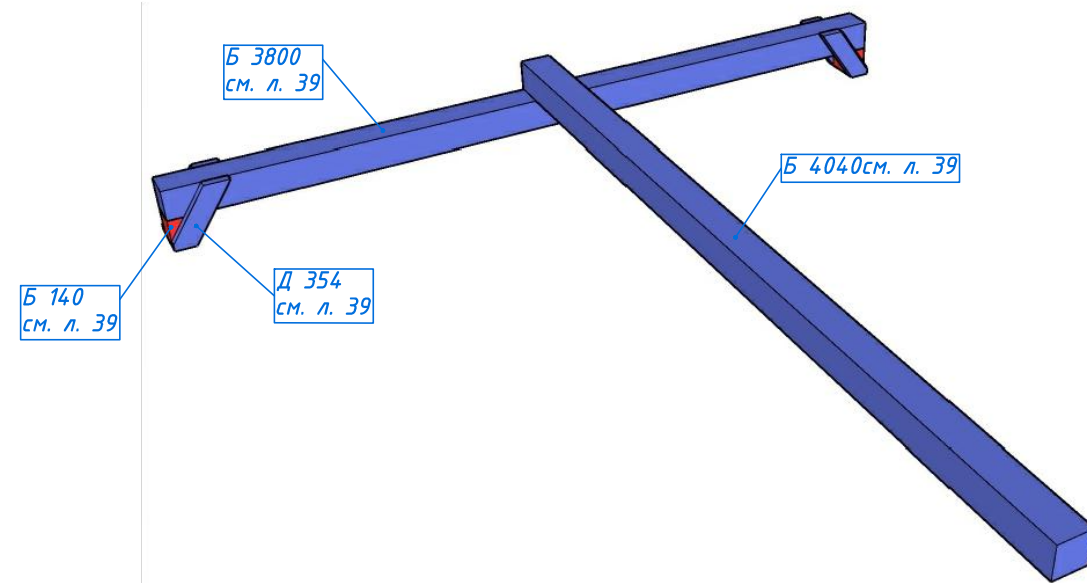



Изм.	Кол. уч.	Лист	№ док.	Подп.	Дата

Коньковая система (конец).

Луст

40


Крыша. Общий вид.

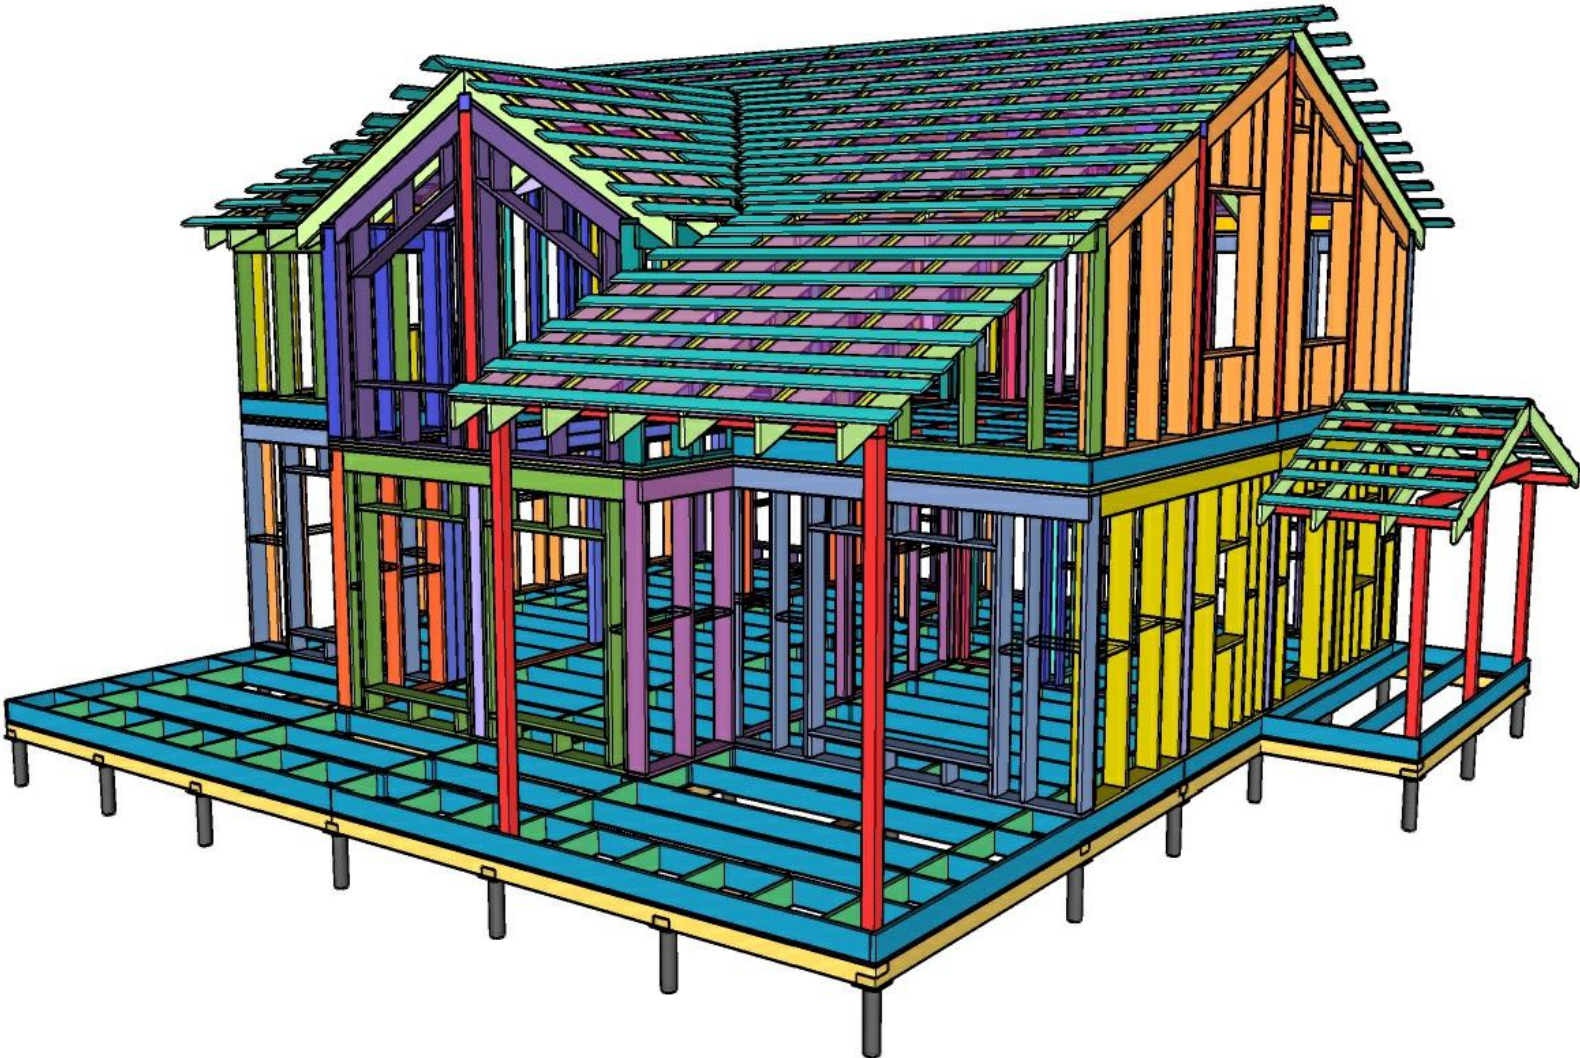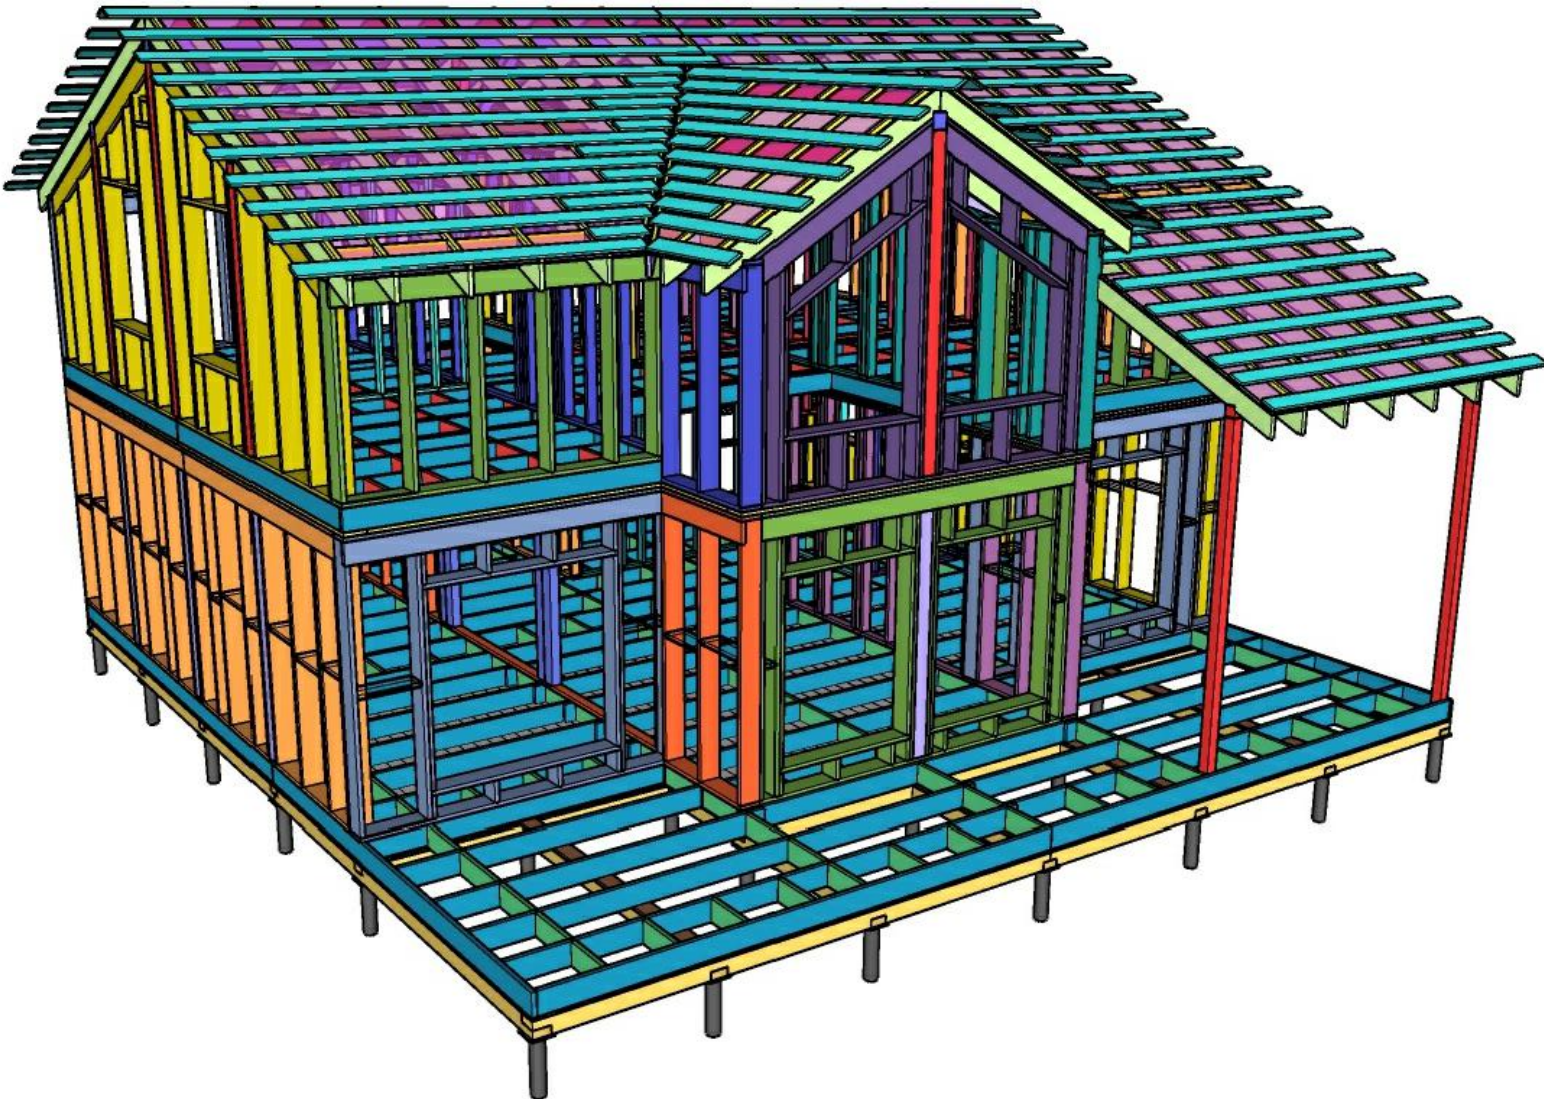


Изм.	Кол. уч.	Лист	№ док.	Подп.	Дата

Крыша. Общий вид.

Стропильная система. Схема раскладки.

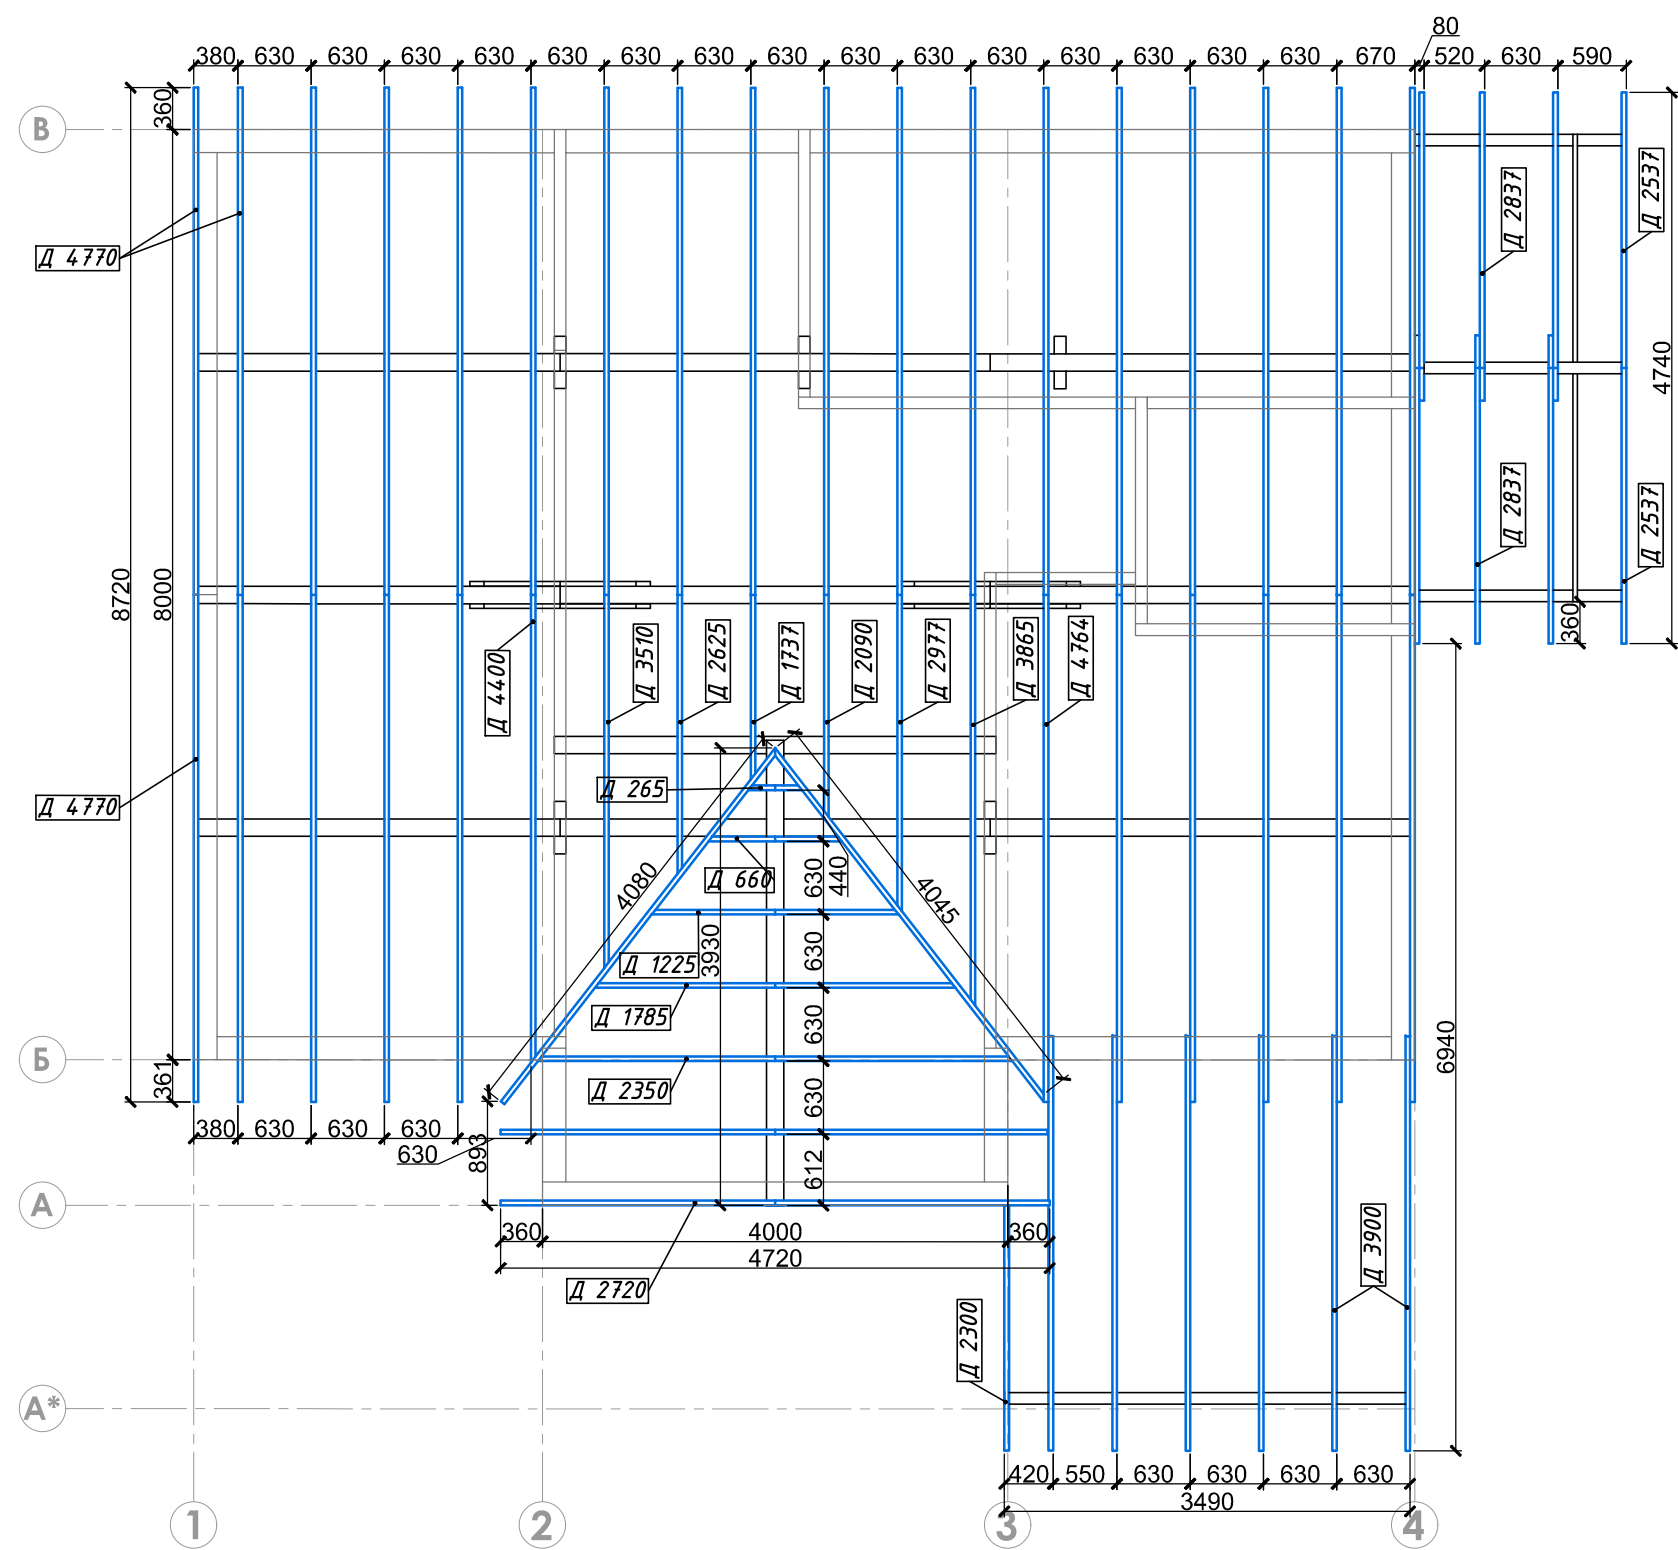







Стропильная система. Общий вид.

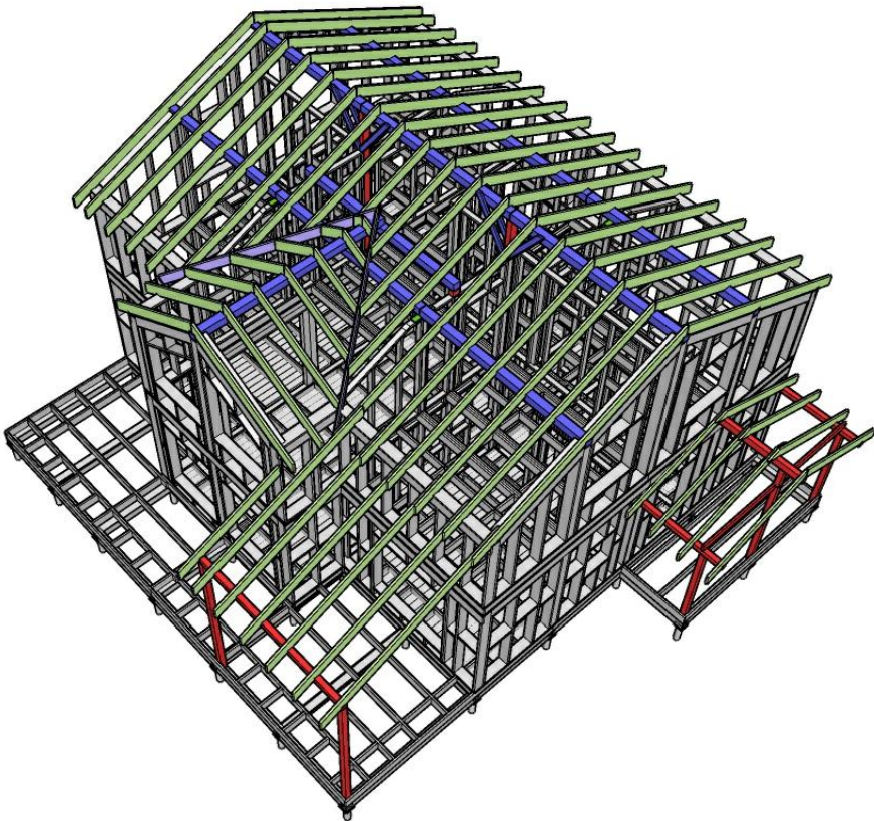

Экспликация:


Маркировка	Длина	Ширина	Толщина	Кол-во
Д 4770	4770	200	40	28
Д 4764	4764	200	40	1
Д 4400	4400	200	40	1
Д 4045	4045	200	40	1
Д 4080	4080	200	40	1
Д 3900	3900	200	40	6
Д 3865	3865	200	40	1
Д 3510	3510	200	40	1
Д 2977	2977	200	40	1
Д 2837	2837	200	40	6
Д 2720	2720	200	40	4
Д 2625	2625	200	40	1
Д 2537	2537	200	40	2
Д 2350	2350	200	40	2
Д 2300	2300	200	40	1
Д 2090	2090	200	40	1
Д 1785	1785	200	40	2
Д 1737	1737	200	40	1
Д 1225	1225	200	40	2
Д 660	660	200	40	2
Д 265	265	200	40	2

Стропильная система. Схема раскладки.

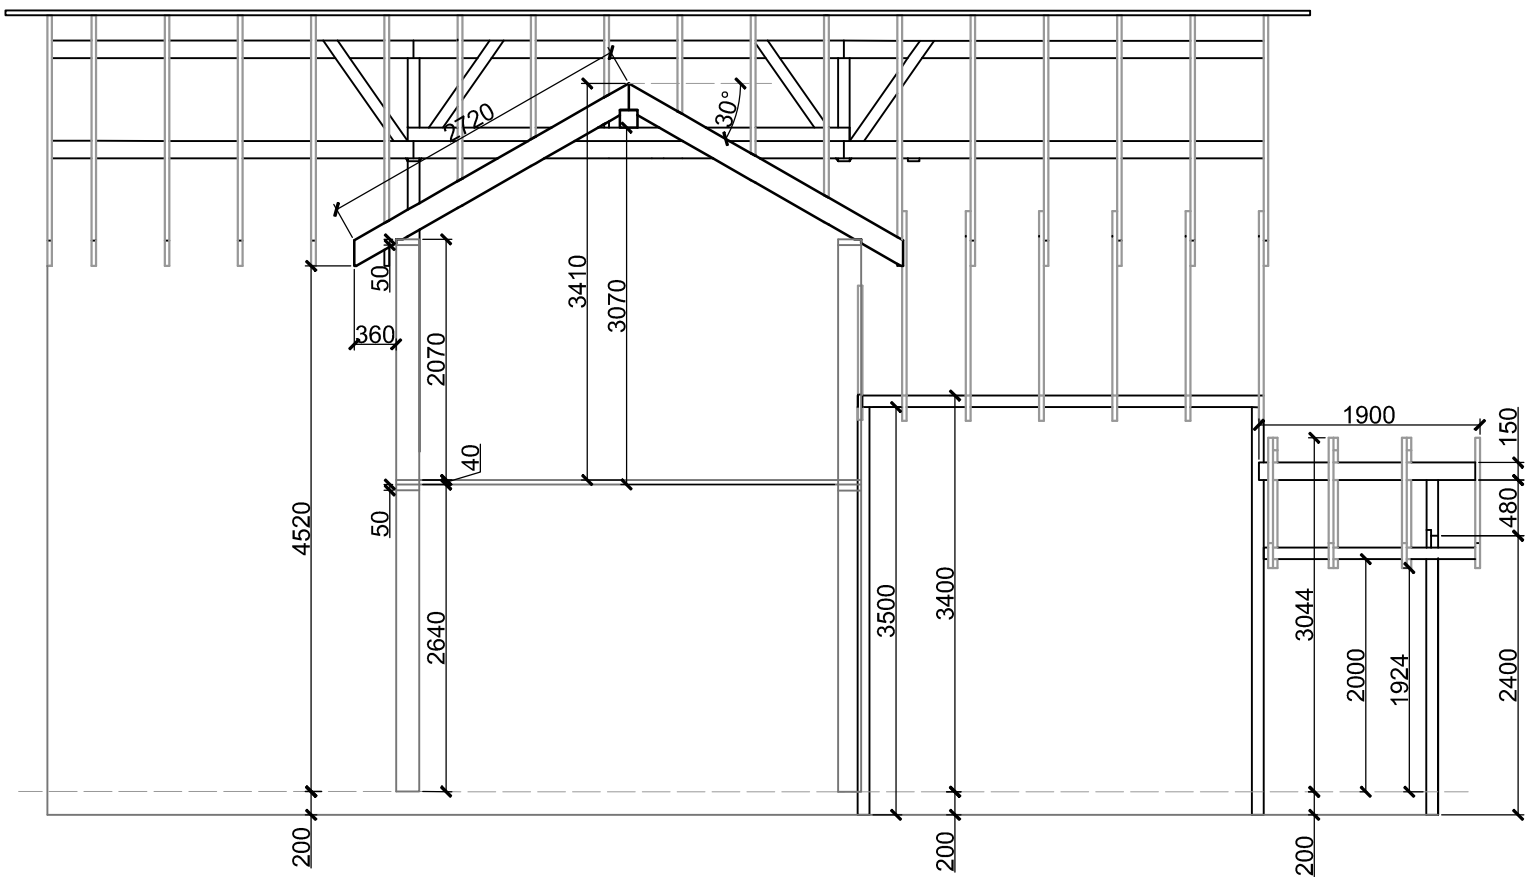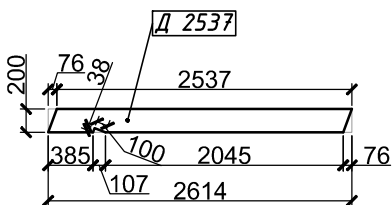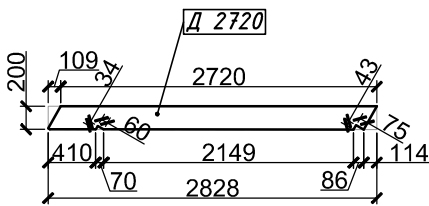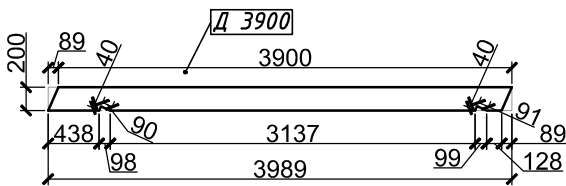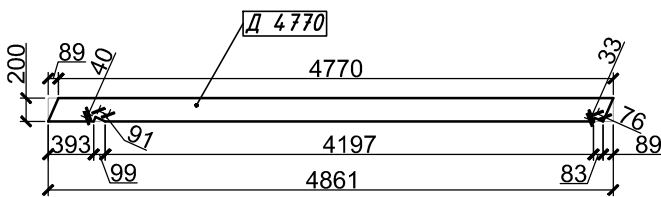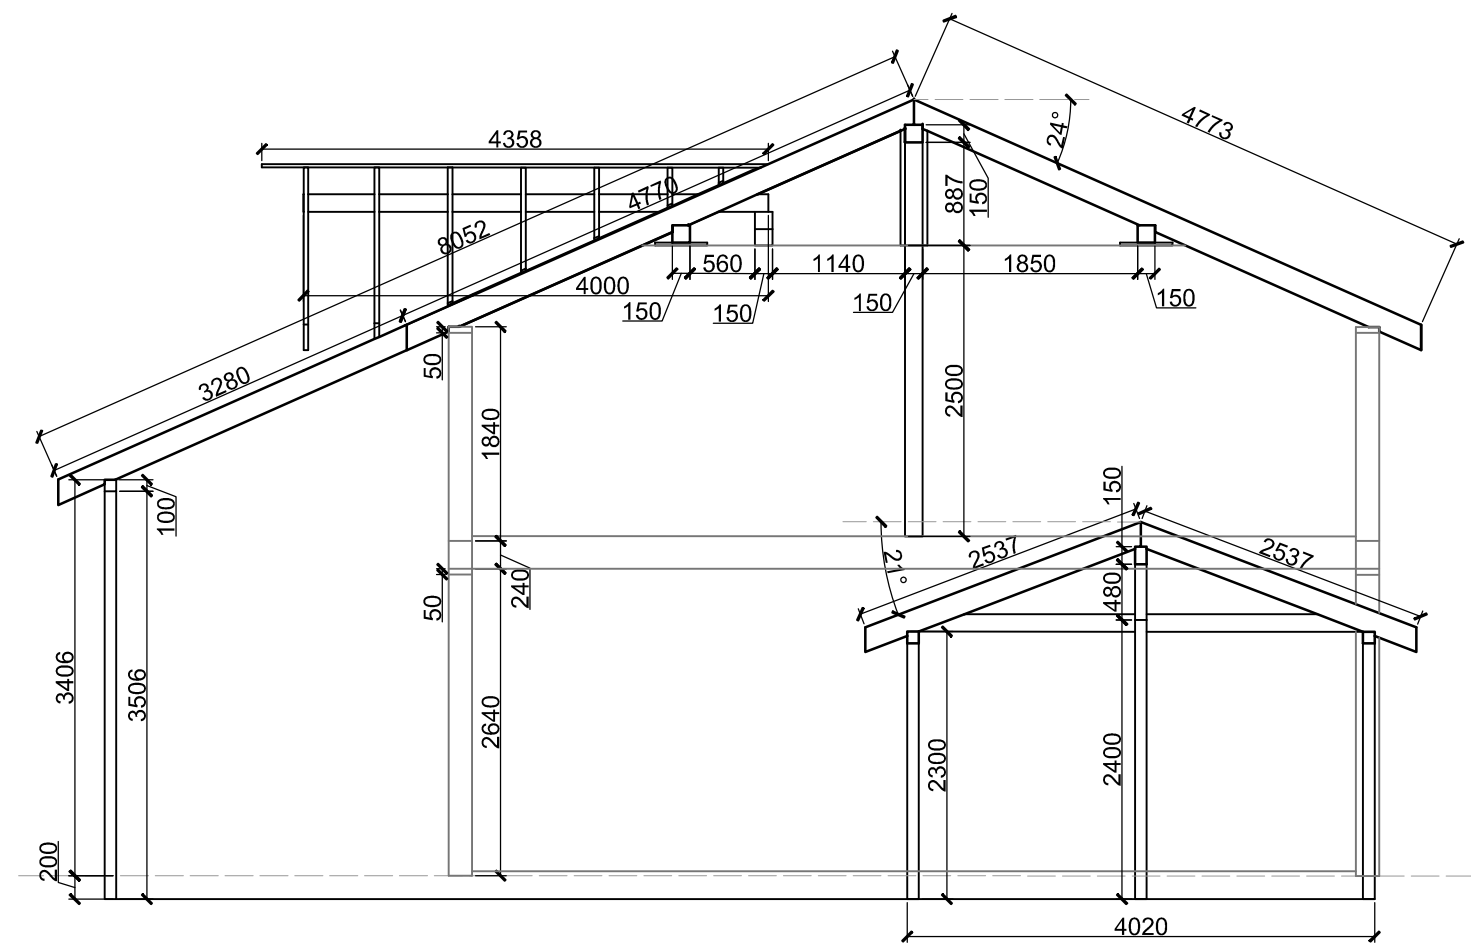

Изм.	Кол. уч.	Лист	№ док.	Подп.	Дата	Стропильная система. Схема раскладки.	Лист
							43

Затяжки стропил (чердачные балки). Лобовая доска.

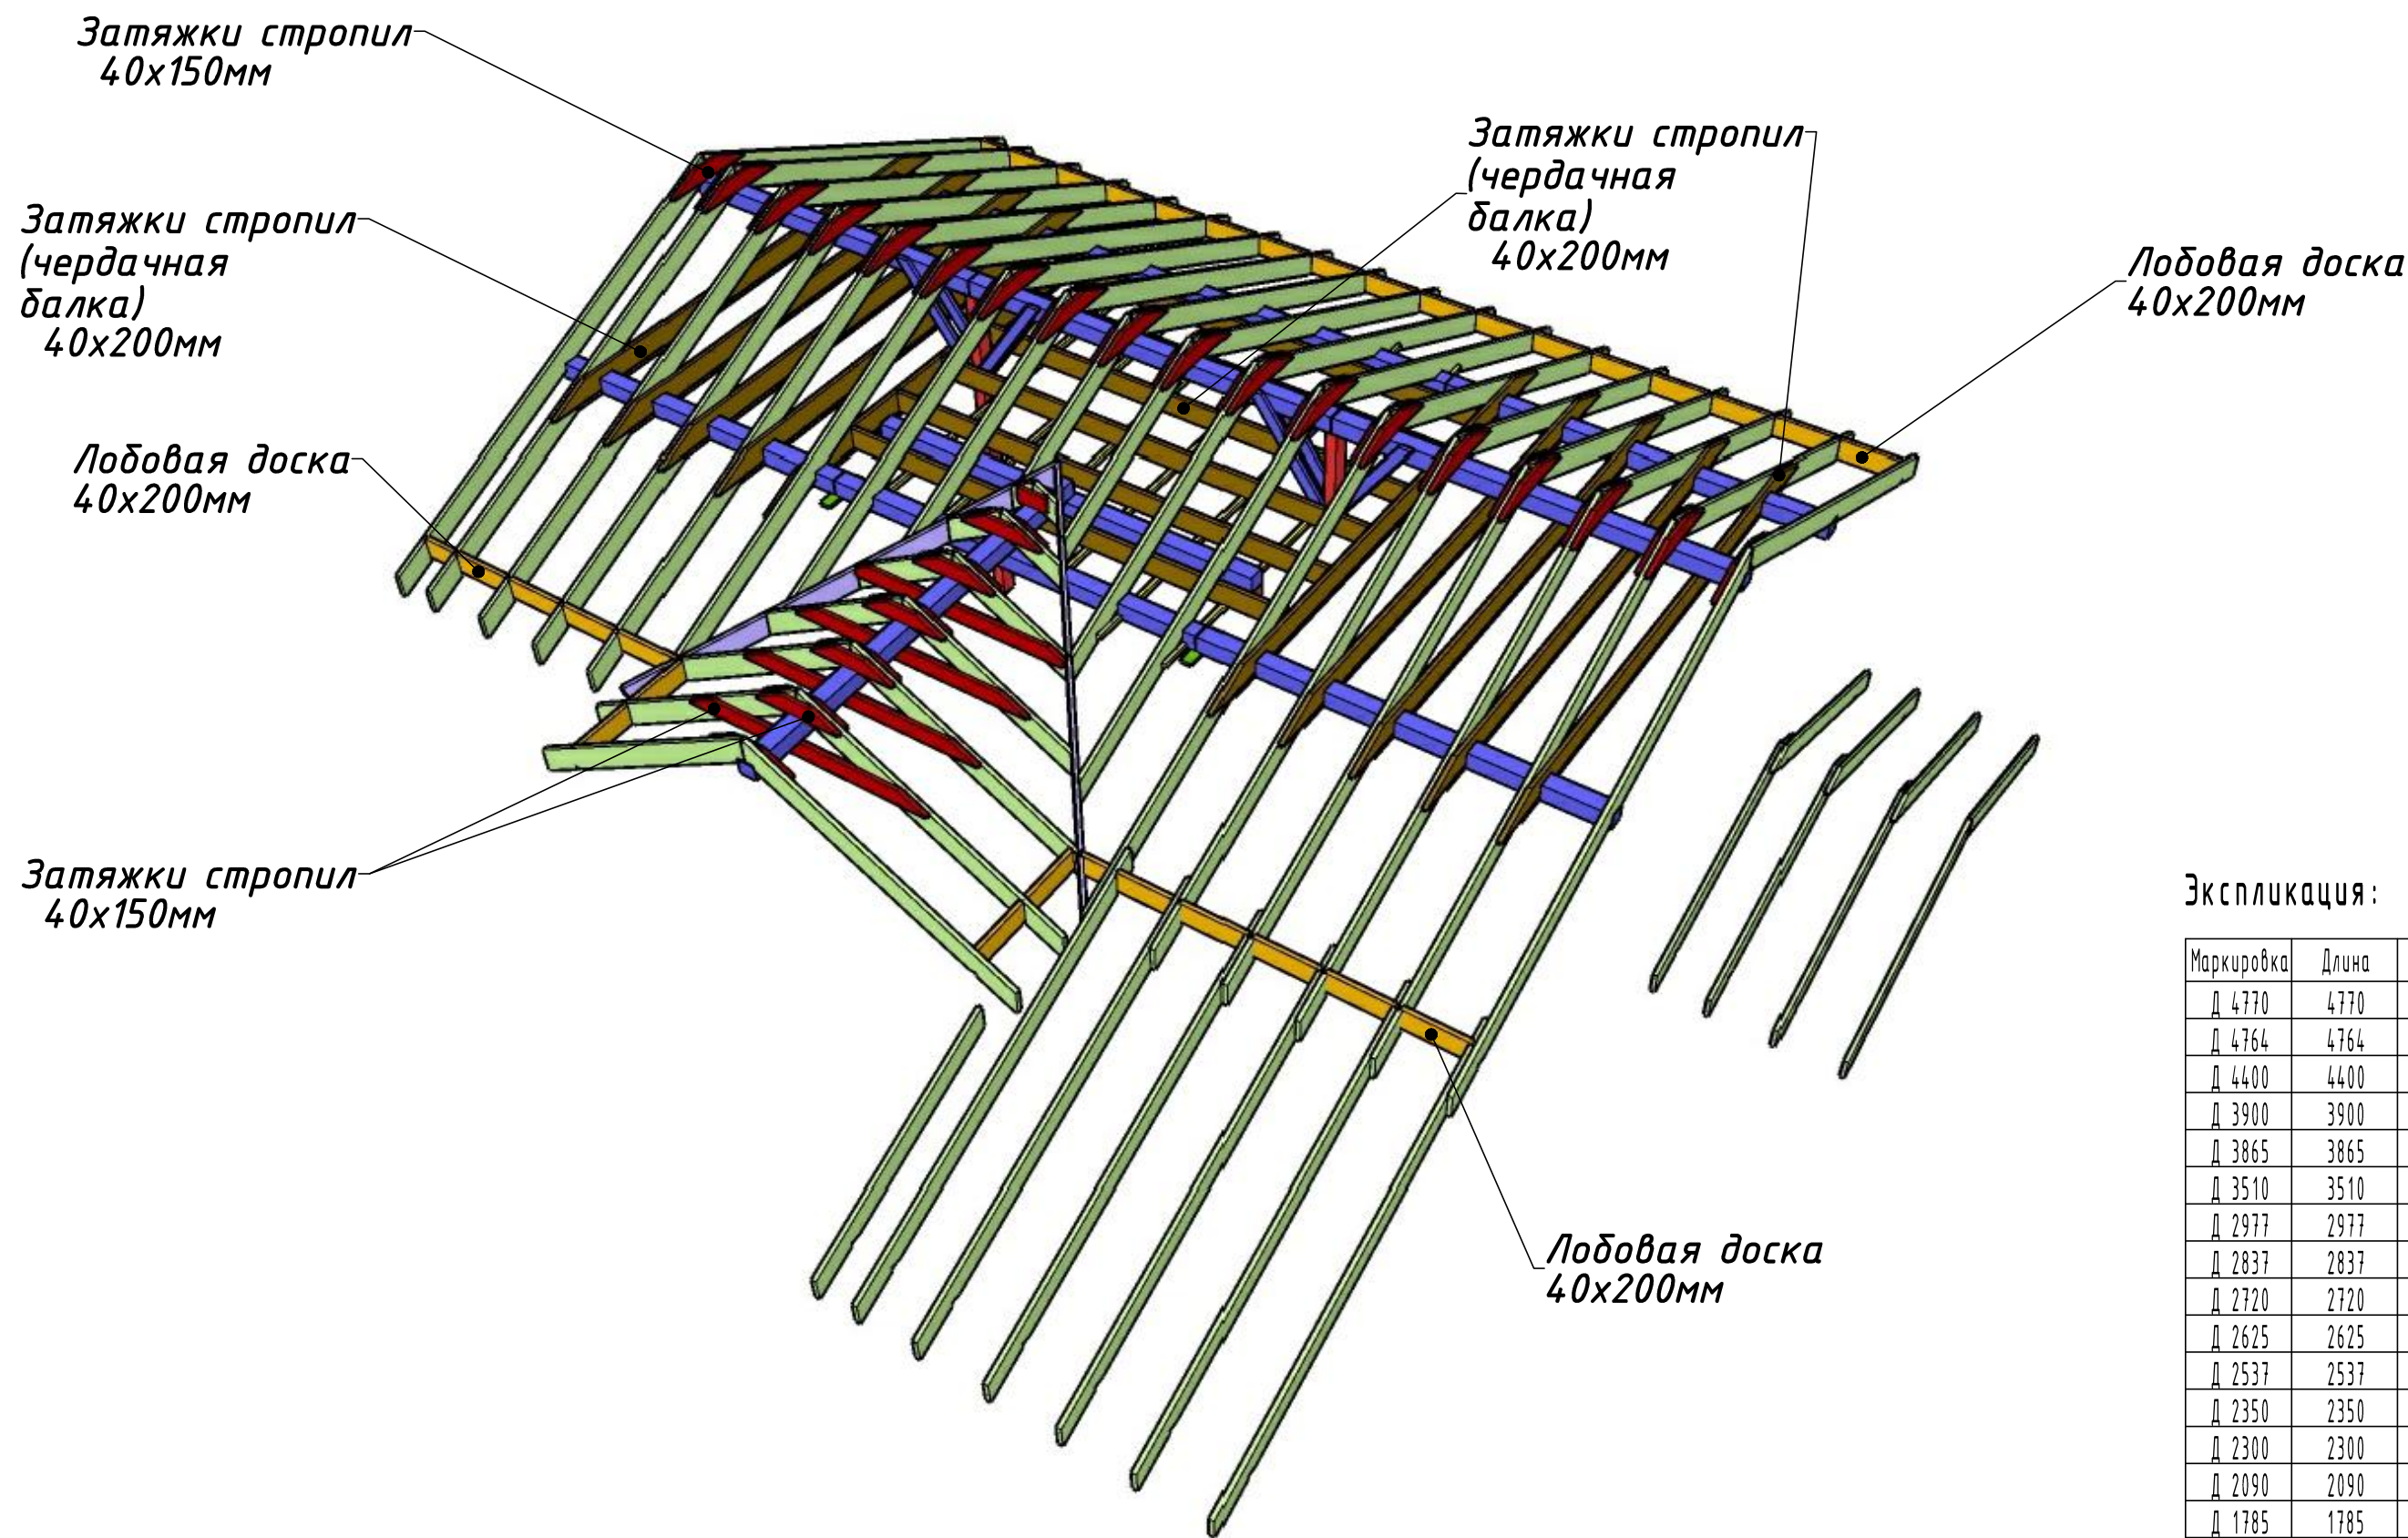


Экспликация:

Маркировка	Длина	Ширина	Толщина	Кол-во
Д 4770	4770	200	40	28
Д 4764	4764	200	40	1
Д 4400	4400	200	40	1
Д 3900	3900	200	40	6
Д 3865	3865	200	40	1
Д 3510	3510	200	40	1
Д 2977	2977	200	40	1
Д 2837	2837	200	40	6
Д 2720	2720	200	40	4
Д 2625	2625	200	40	1
Д 2537	2537	200	40	2
Д 2350	2350	200	40	2
Д 2300	2300	200	40	1
Д 2090	2090	200	40	1
Д 1785	1785	200	40	2
Д 1737	1737	200	40	1
Д 1225	1225	200	40	2
Д 660	660	200	40	2
Д 265	265	200	40	2


Изм.	Кол. уч.	Лист	№ док.	Подп.	Дата	Затяжки стропил. Чердачные балки. Лобовая доска.	Лист
							44

Кровельная мембрана и контробрешетка.

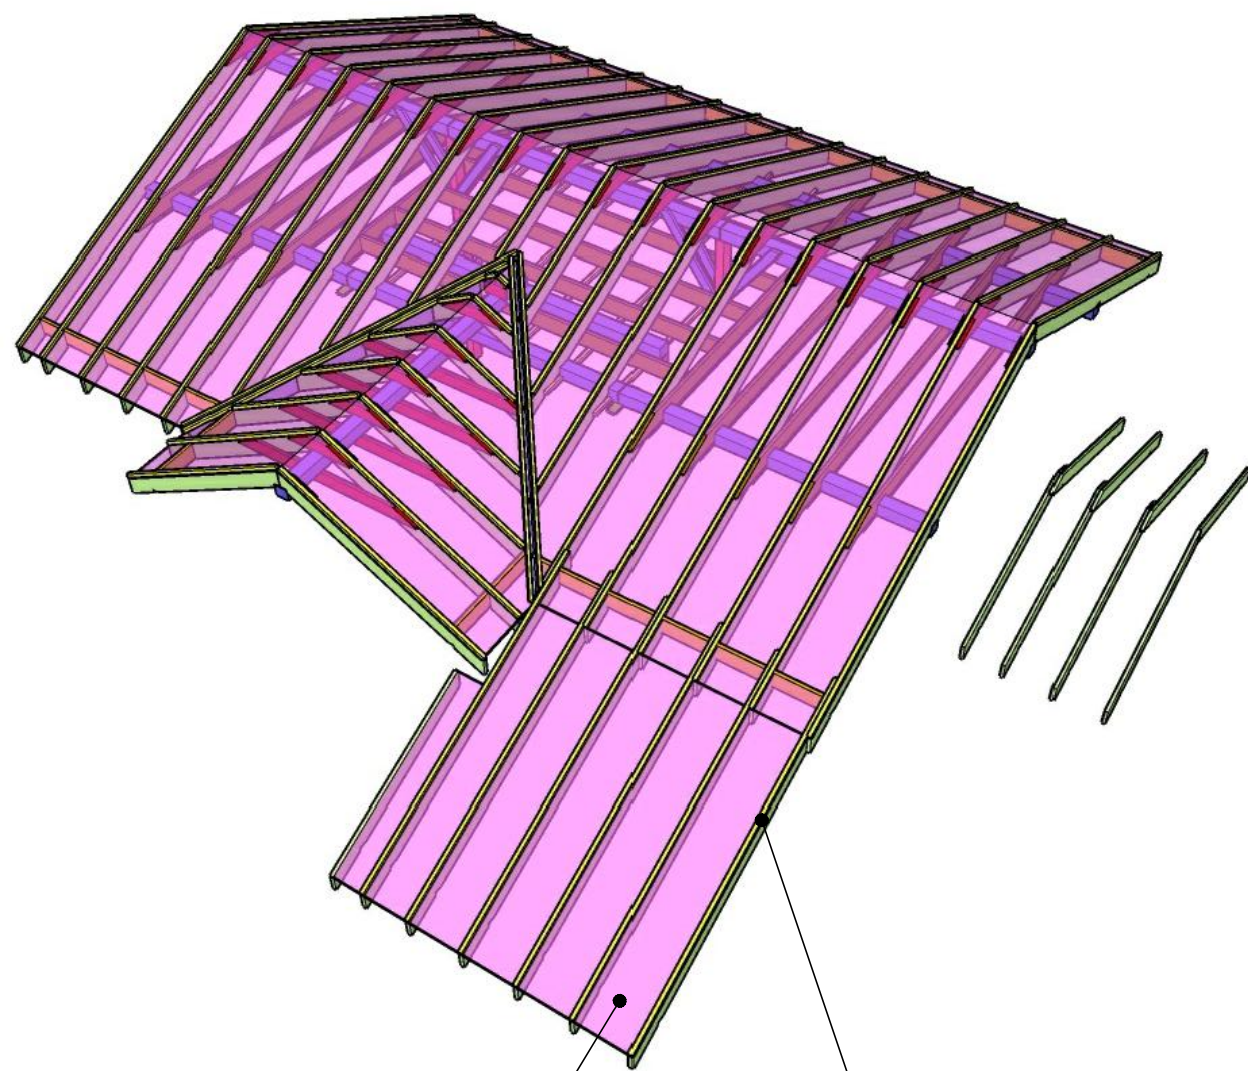

Диффузионная кровельная мембрана.

Контробрешетка 40x40мм.

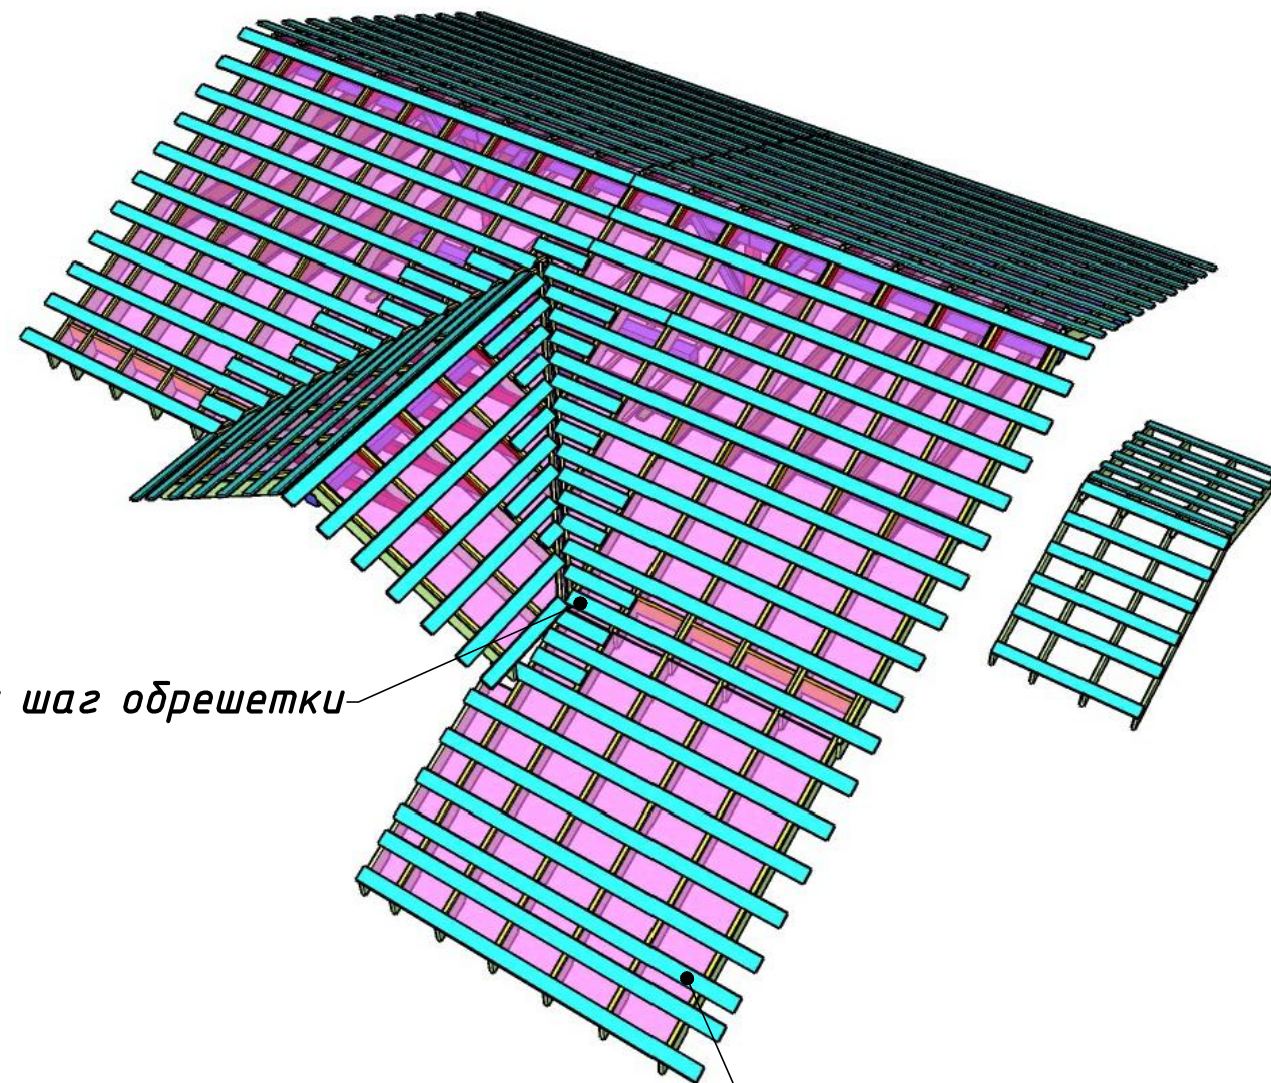

Учащенный шаг обрешетки у ендов

Обрешетка 25x150мм, шаг 300 мм.

Изм.	Кол. уч.	Лист	№ док.	Подп.	Дата	Кровельная мембрана и контробрешетка.	Лист
							45